

PLANOS PRO

Sistema Profesional de Generación de Planos

PROYECTO:

Habilitación Urbana Los Cedros

LOTE:

MZ-C-Lote14

DOCUMENTO: MEMORIA DESCRIPTIVA

FECHA: 24 de enero de 2026

MEMORIA DESCRIPTIVA

I. IDENTIFICACIÓN DEL PREDIO

Código Catastral:	MZ-C-Lote14
Nombre del Lote:	Habilitación Urbana Los Cedros - MZ-C-Lote14
Manzana:	C
Etapas:	Habilitación Urbana Los Cedros
Número de Lote:	14
Estado:	LIBRE

II. UBICACIÓN GEOGRÁFICA

Sistema de Coordenadas:	UTM WGS84 - Zona 18S
Datum:	WGS84
Hemisferio:	Sur

III. CARACTERÍSTICAS MÉTRICAS DEL PREDIO

ÁREA TOTAL:	200.00 m ²
PERÍMETRO TOTAL:	60.00 ml
Frente:	10.00 ml
Fondo:	10.00 ml
Lado Derecho:	20.00 ml
Lado Izquierdo:	20.00 ml

IV. LINDEROS Y COLINDANCIAS

El predio tiene los siguientes linderos y colindancias:

PLANOS PRO

Sistema Profesional de Generación de Planos

PROYECTO:

Habilitación Urbana Los Cedros

LOTE:

MZ-C-Lote14

DOCUMENTO: MEMORIA DESCRIPTIVA

FECHA: 24 de enero de 2026

Por el NORTE: Con calle "Av. Los Alamos"

Por el SUR: Con lote "Lote 05"

Por el OESTE: Con lote "Lote 13"

Por el ESTE: Con lote "Lote 15"

V. CUADRO DE DATOS TÉCNICOS - COORDENADAS UTM

VÉRTICE	LADO	ESTE (m)	NORTE (m)
V1	V1-V2	284500.00	8670100.00
V2	V2-V3	284510.00	8670100.00
V3	V3-V4	284510.00	8670080.00
V4	V4-V1	284500.00	8670080.00

PROPIETARIO


Firma y Sello

PROFESIONAL RESPONSABLE

Ing. Civil / Arquitecto

Este documento ha sido generado automáticamente por el sistema PLANOS PRO

Código de Verificación: MZ-C-Lote14-MKT4RUIS

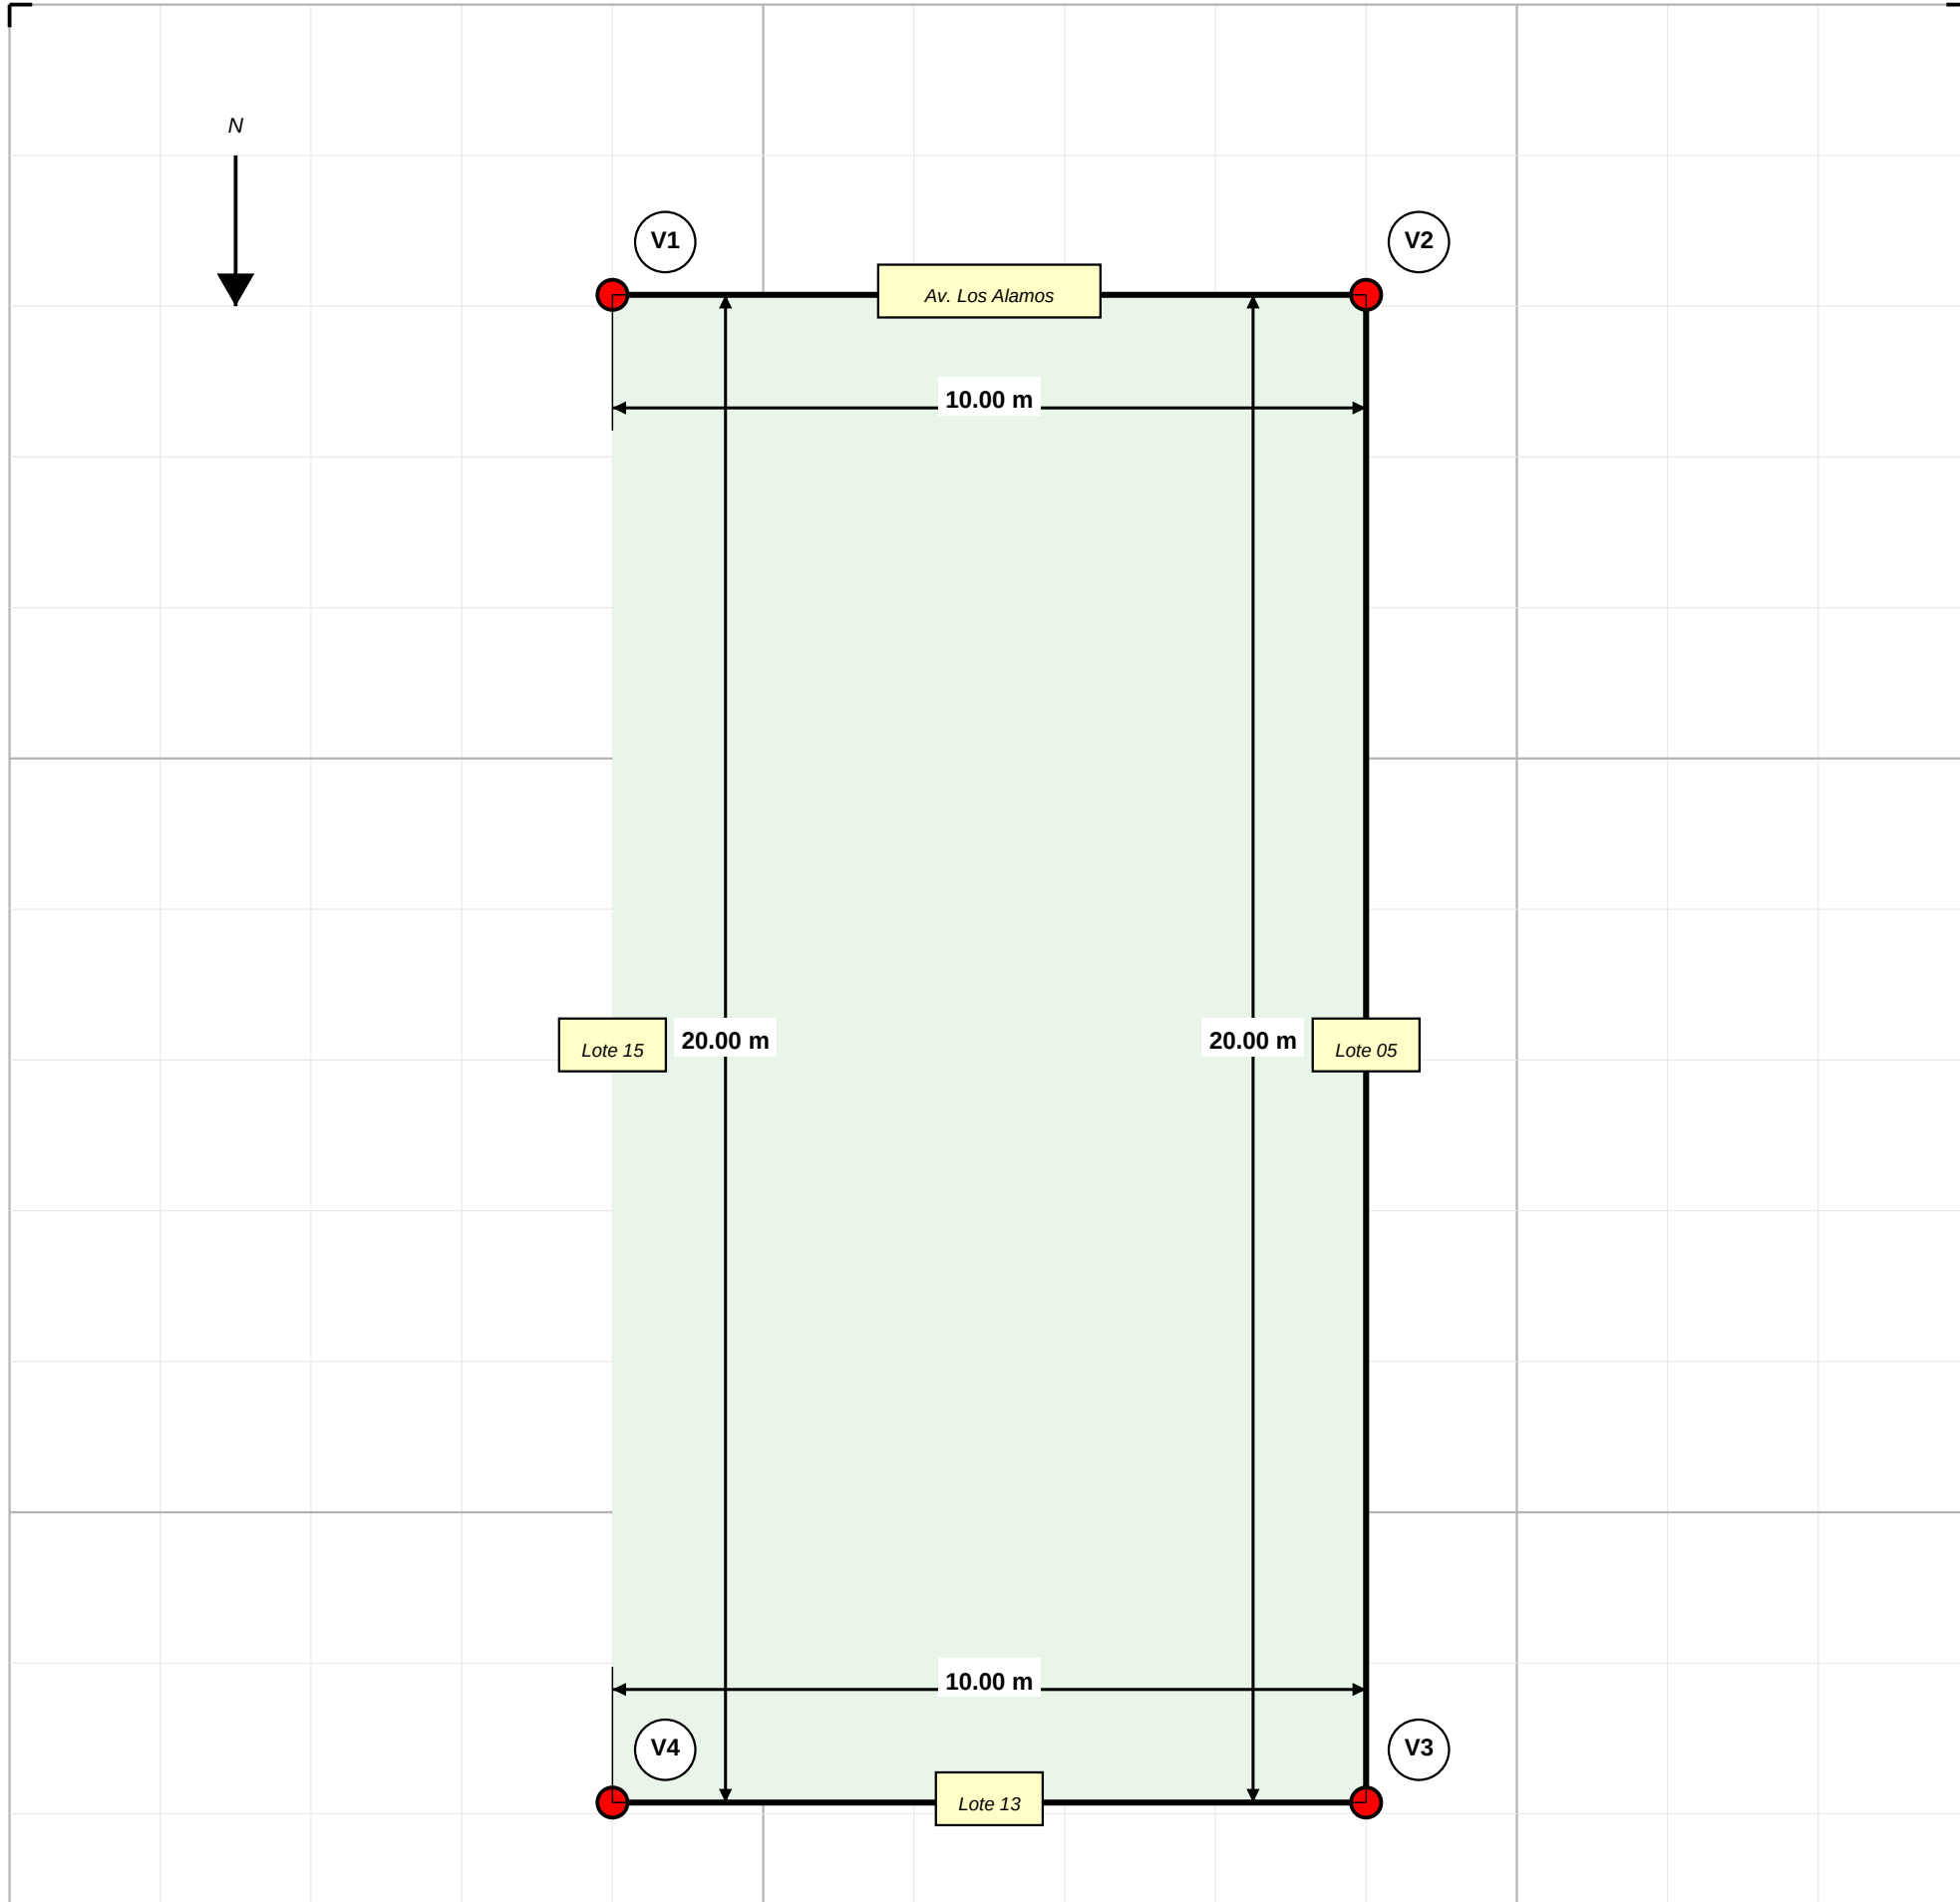

CUADRO TÉCNICO DE COORDENADAS				
SISTEMA:				
UTM - Universal Transversa de Mercator				
DATUM:				
WGS84 - World Geodetic System 1984				

ZONA UTM:	ESCALA:
18 SUR	1:100

VÉRT.	LADO	ESTE (m)	NORTE (m)	ÁNGULO (°)
V1	V1-V2	284500.00	8670100.00	270°00'00"
V2	V2-V3	284510.00	8670100.00	270°00'00"
V3	V3-V4	284510.00	8670080.00	270°00'00"
V4	V4-V1	284500.00	8670080.00	270°00'00"

MEMBRETE TÉCNICO

PROYECTO:
Habilitación Urbana Los Cedros

LOTE:
MZ-C-Lote14

ÁREA TOTAL:
200.00 m²

PERÍMETRO:
60.00 m

LINDEROS Y COLINDANCIAS:

NORTE: Av. Los Alamos

SUR: Lote 05

OESTE: Lote 13

ESTE: Lote 15

FECHA:
24 de enero de 2026

PROFESIONAL RESPONSABLE:

Firma y Sello

PLANO DE UBICACIÓN

Habilitación Urbana Los Cedros - MZ-C-Lote14



MAPA DE UBICACIÓN

(Requiere integración con servicio de mapas)

Lat: -76.979386°
Lng: -12.023339°
UTM: 284505.00, 8670090.00

DATOS DE UBICACIÓN

Departamento: Lima
Provincia: Lima
Distrito: Habilitación Urbana Los Cedros
Zona UTM: 18S