

PLANOS PRO

Sistema Profesional de Generación de Planos

PROYECTO:

Habilitación Urbana Los Cedros

LOTE:

MZ-C-Lote14

DOCUMENTO: MEMORIA DESCRIPTIVA

FECHA: 24 de enero de 2026

MEMORIA DESCRIPTIVA

I. IDENTIFICACIÓN DEL PREDIO

Código Catastral:	MZ-C-Lote14
Nombre del Lote:	Habilitación Urbana Los Cedros - MZ-C-Lote14
Manzana:	C
Etapas:	Habilitación Urbana Los Cedros
Número de Lote:	14
Estado:	LIBRE

II. UBICACIÓN GEOGRÁFICA

Sistema de Coordenadas:	UTM WGS84 - Zona 18S
Datum:	WGS84
Hemisferio:	Sur

III. CARACTERÍSTICAS MÉTRICAS DEL PREDIO

ÁREA TOTAL:	200.00 m ²
PERÍMETRO TOTAL:	46.42 ml
Frente:	10.00 ml
Fondo:	10.00 ml
Lado Derecho:	20.00 ml
Lado Izquierdo:	20.00 ml

IV. LINDEROS Y COLINDANCIAS

El predio tiene los siguientes linderos y colindancias:

PLANOS PRO

Sistema Profesional de Generación de Planos

PROYECTO:

Habilitación Urbana Los Cedros

LOTE:

MZ-C-Lote14

DOCUMENTO: MEMORIA DESCRIPTIVA

FECHA: 24 de enero de 2026

Por el NORTE: Con calle "Av. Los Alamos"

Por el SUR: Con lote "Lote 05"

Por el OESTE: Con lote "Lote 13"

Por el ESTE: Con lote "Lote 15"

V. CUADRO DE DATOS TÉCNICOS - COORDENADAS UTM

VÉRTICE	LADO	ESTE (m)	NORTE (m)
V1	V1-V2	284504.34	8670097.19
V2	V2-V3	284504.79	8670088.33
V3	V3-V4	284510.00	8670080.00
V4	V4-V1	284500.00	8670080.00

PROPIETARIO


Firma y Sello

PROFESIONAL RESPONSABLE

Ing. Civil / Arquitecto

Este documento ha sido generado automáticamente por el sistema PLANOS PRO

Código de Verificación: MZ-C-Lote14-MKT5JUKG

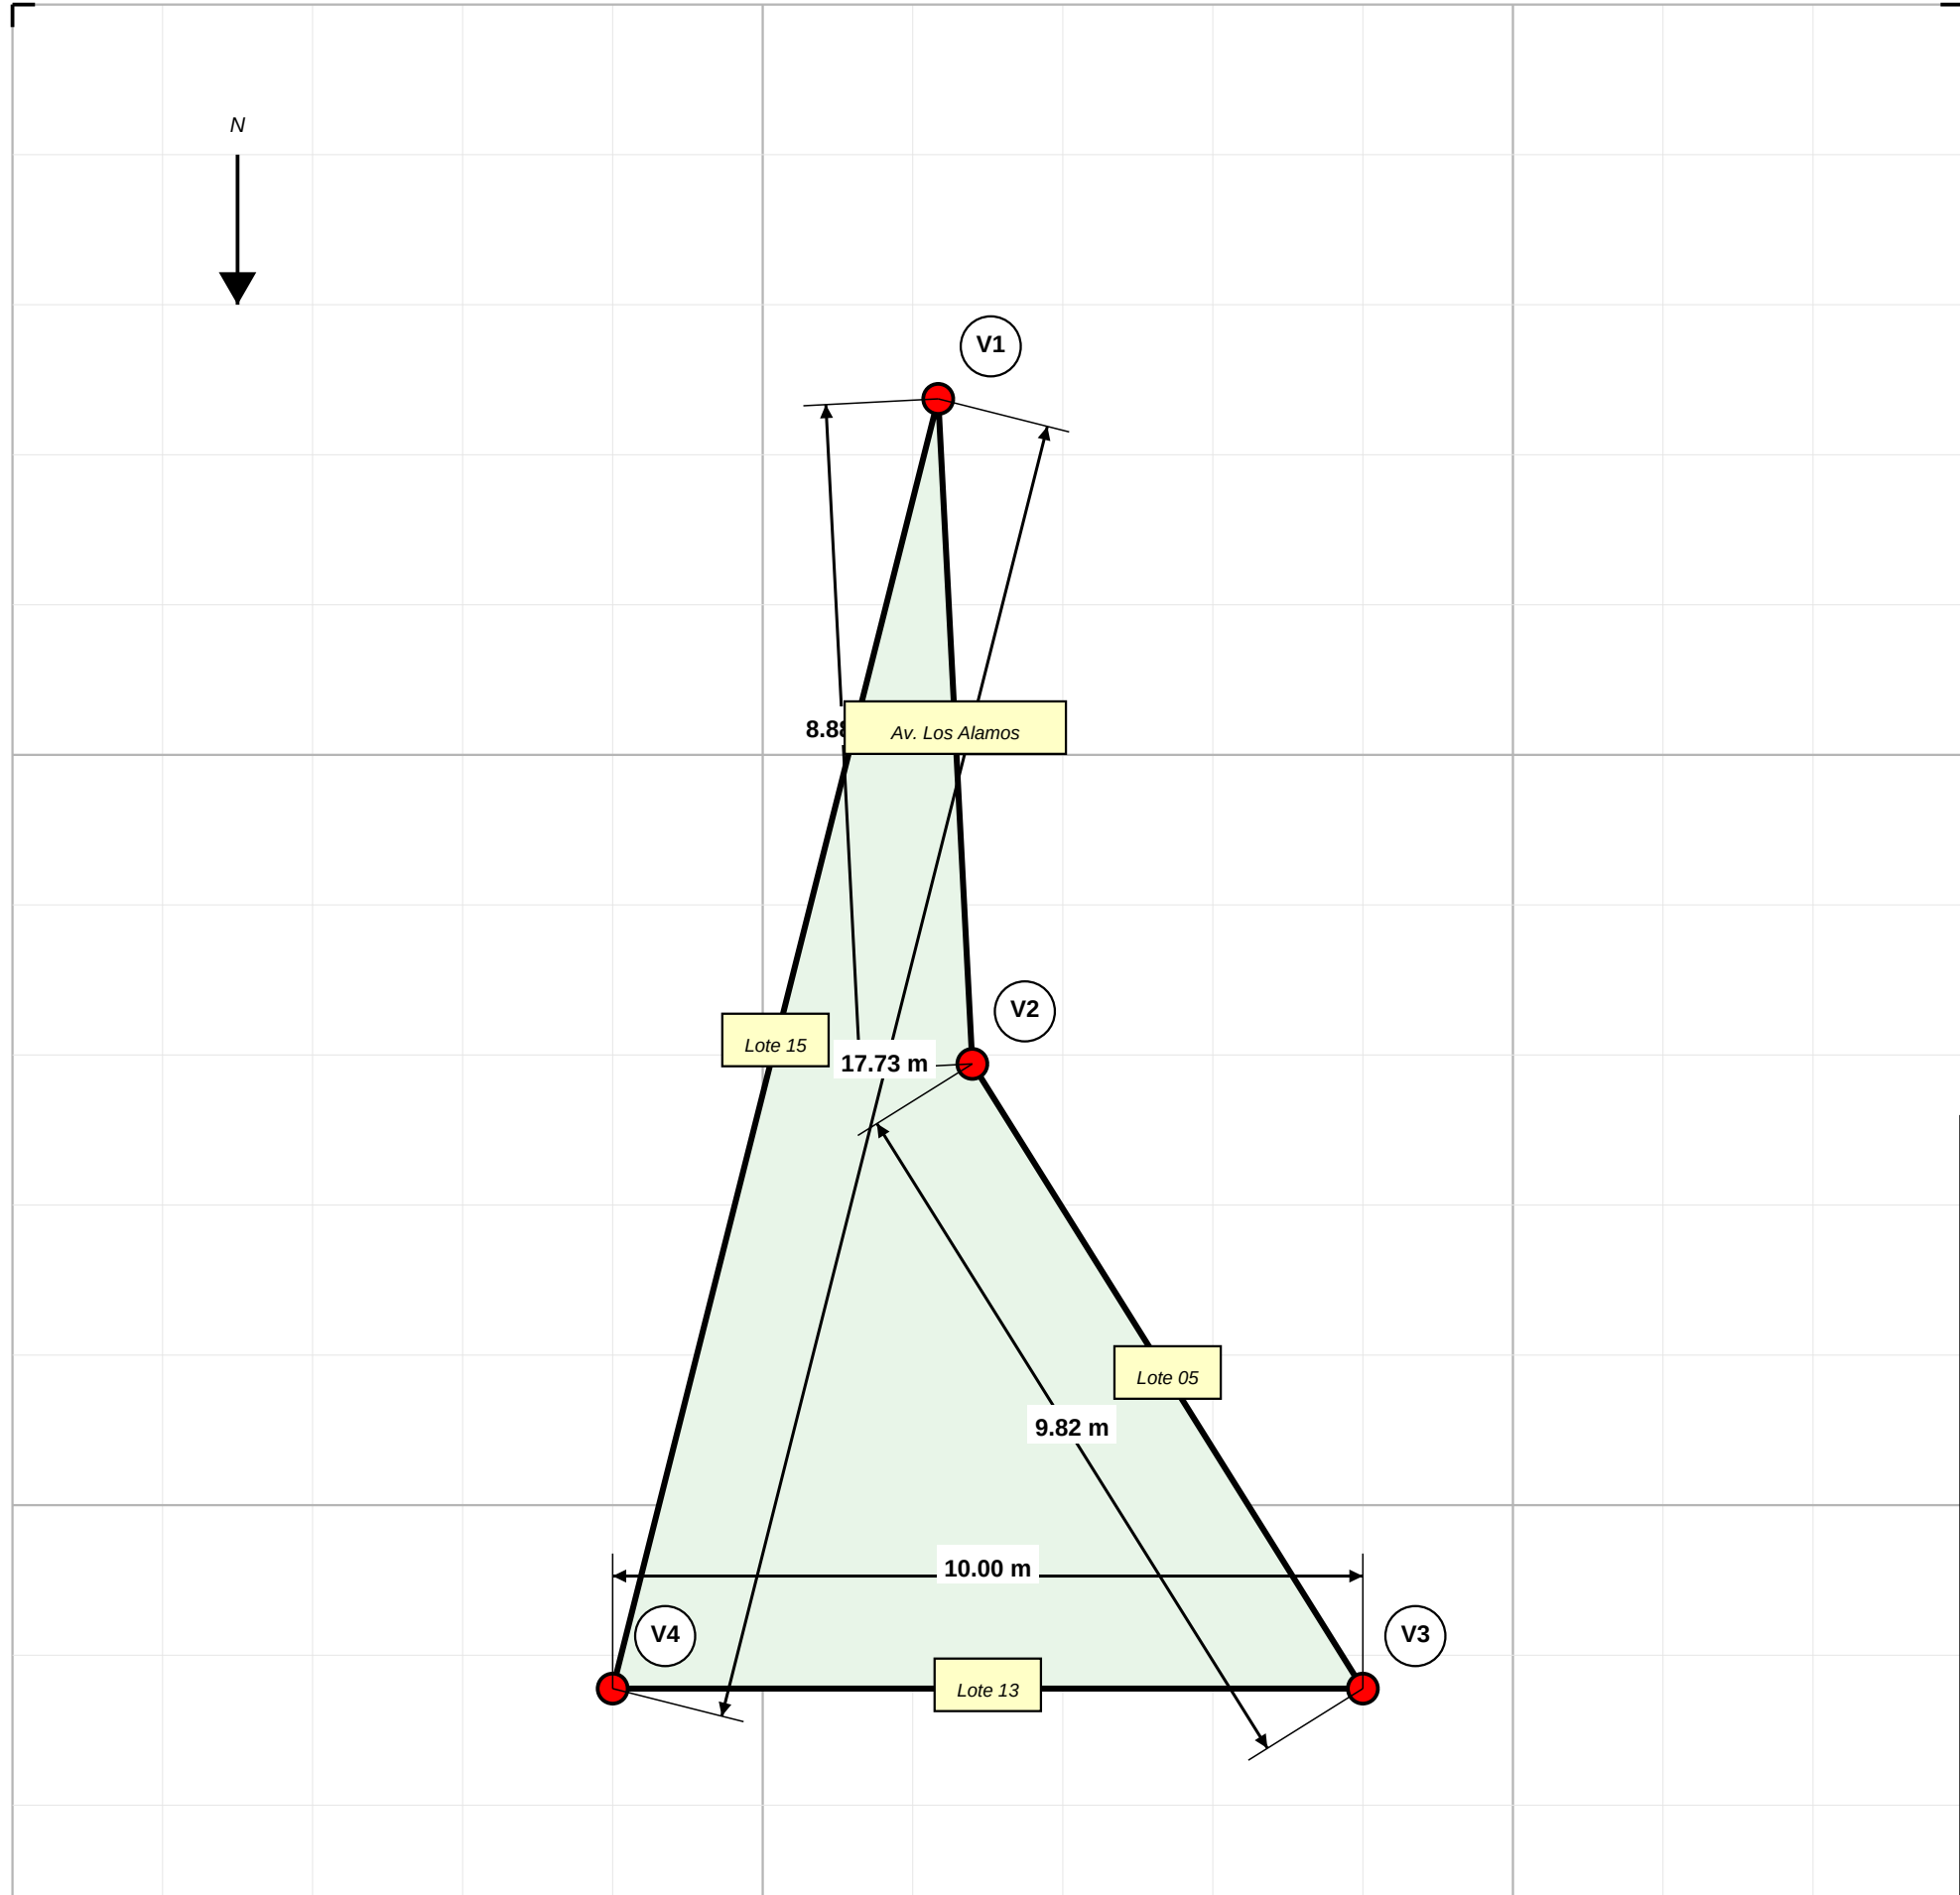

CUADRO TÉCNICO DE COORDENADAS					
SISTEMA: UTM - Universal Transversa de Mercator					
DATUM: WGS84 - World Geodetic System 1984					
ZONA UTM: 18 SUR				ESCALA: 1:100	
VÉRT.	LADO	DIST. LADO	ANG. INT	ESTE (m)	NORTE (m)
V1	V1-V2	8.88	342°53'43"	284504.34	8670097.19
V2	V2-V3	9.82	150°55'16"	284504.79	8670088.33
V3	V3-V4	10.00	302°00'52"	284510.00	8670080.00
V4	V4-V1	17.73	284°10'08"	284500.00	8670080.00

CAJETÍN TÉCNICO	
DATOS DEL PROYECTO	
PROYECTO:	Habilitación Urbana Los Cedr
UBICACIÓN:	Lima - Perú
CÓDIGO LOTE:	MZ-C-Lote14
CARACTERÍSTICAS TÉCNICAS	
ÁREA TOTAL:	200.00 m²
PERÍMETRO:	46.42 ml
FRENTE:	10.00 ml
FONDO:	10.00 ml
LINDEROS Y COLINDANCIAS	
NORTE:	Av. Los Alamos
SUR:	Lote 05
OESTE:	Lote 13
ESTE:	Lote 15
INFORMACIÓN LEGAL	
FECHA:	24 de enero de 2026
ESCALA:	Ver indicación

PLANO DE UBICACIÓN

Habilitación Urbana Los Cedros - MZ-C-Lote14



MAPA DE UBICACIÓN

(Requiere integración con servicio de mapas)

Lat: -76.979388°
Lng: -12.023371°
UTM: 284504.78, 8670086.38

DATOS DE UBICACIÓN

Departamento: Lima
Provincia: Lima
Distrito: Habilitación Urbana Los Cedros
Zona UTM: 18S