

# PLANOS PRO

Sistema Profesional de Generación de Planos

## PROYECTO:

Habilitación Urbana Los Cedros

## LOTE:

MZ-C-Lote14

DOCUMENTO: MEMORIA DESCRIPTIVA

FECHA: 24 de enero de 2026

## MEMORIA DESCRIPTIVA

### I. IDENTIFICACIÓN DEL PREDIO

|                   |                                              |
|-------------------|----------------------------------------------|
| Código Catastral: | MZ-C-Lote14                                  |
| Nombre del Lote:  | Habilitación Urbana Los Cedros - MZ-C-Lote14 |
| Manzana:          | C                                            |
| Etapas:           | Habilitación Urbana Los Cedros               |
| Número de Lote:   | 14                                           |
| Estado:           | LIBRE                                        |

### II. UBICACIÓN GEOGRÁFICA

|                         |                      |
|-------------------------|----------------------|
| Sistema de Coordenadas: | UTM WGS84 - Zona 18S |
| Datum:                  | WGS84                |
| Hemisferio:             | Sur                  |

### III. CARACTERÍSTICAS MÉTRICAS DEL PREDIO

|                  |                       |
|------------------|-----------------------|
| ÁREA TOTAL:      | 200.00 m <sup>2</sup> |
| PERÍMETRO TOTAL: | 53.33 ml              |
| Frente:          | 10.00 ml              |
| Fondo:           | 10.00 ml              |
| Lado Derecho:    | 20.00 ml              |
| Lado Izquierdo:  | 20.00 ml              |

### IV. LINDEROS Y COLINDANCIAS

El predio tiene los siguientes linderos y colindancias:

# PLANOS PRO

Sistema Profesional de Generación de Planos

## PROYECTO:

Habilitación Urbana Los Cedros

## LOTE:

MZ-C-Lote14

DOCUMENTO: MEMORIA DESCRIPTIVA

FECHA: 24 de enero de 2026

Por el NORTE: Con calle "Av. Los Alamos"

Por el SUR: Con lote "Lote 05"

Por el OESTE: Con lote "Lote 13"

Por el ESTE: Con lote "Lote 15"

## V. CUADRO DE DATOS TÉCNICOS - COORDENADAS UTM

| VÉRTICE | LADO  | ESTE (m)  | NORTE (m)  |
|---------|-------|-----------|------------|
| V1      | V1-V2 | 284500.00 | 8670100.00 |
| V2      | V2-V3 | 284508.23 | 8670090.98 |
| V3      | V3-V4 | 284510.00 | 8670080.00 |
| V4      | V4-V1 | 284500.00 | 8670080.00 |

PROPIETARIO



Firma y Sello

PROFESIONAL RESPONSABLE

Ing. Civil / Arquitecto

Este documento ha sido generado automáticamente por el sistema PLANOS PRO

Código de Verificación: MZ-C-Lote14-MKT8M8K9

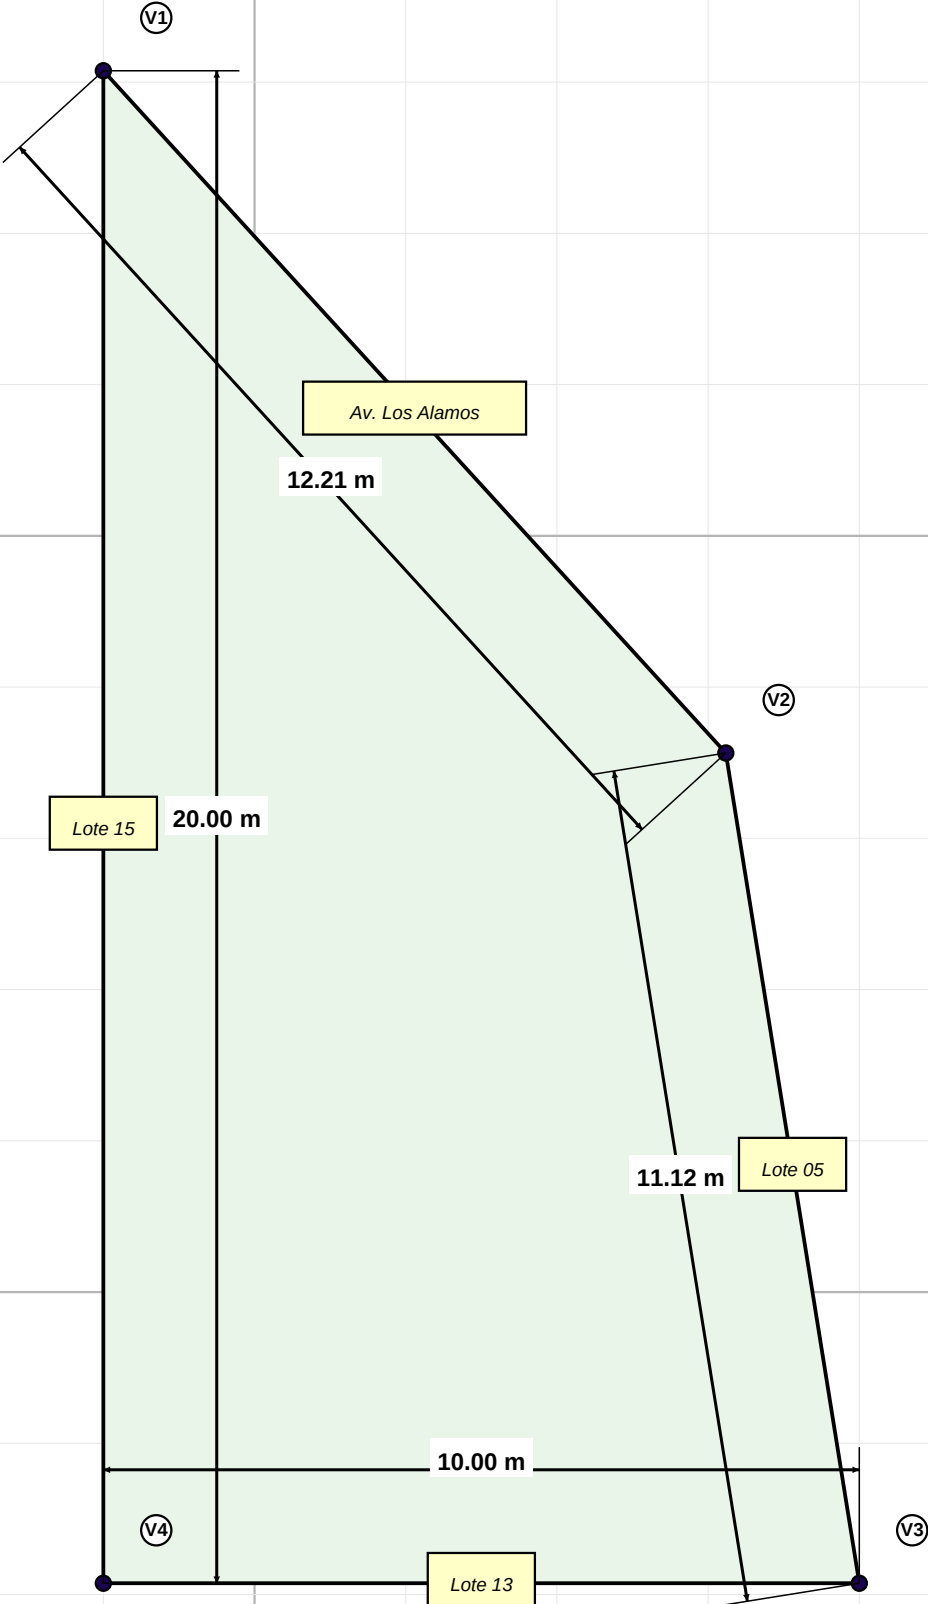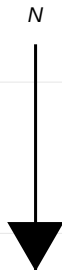

### CUADRO TÉCNICO DE COORDENADAS

**SISTEMA:**  
UTM - Universal Transversa de Mercator  
**DATUM:**  
WGS84 - World Geodetic System 1984

**ZONA UTM:**  
18 SUR

**ESCALA:**  
1:100

| VÉRT. | LADO  | DIST. LADO | ANG. INT   | ESTE (m)  | NORTE (m)  |
|-------|-------|------------|------------|-----------|------------|
| V1    | V1-V2 | 12.21      | 317°36'43" | 284500.00 | 8670100.00 |
| V2    | V2-V3 | 11.12      | 213°15'02" | 284508.23 | 8670090.98 |
| V3    | V3-V4 | 10.00      | 279°08'13" | 284510.00 | 8670080.00 |
| V4    | V4-V1 | 20.00      | 270°00'00" | 284500.00 | 8670080.00 |

### CAJETÍN TÉCNICO

#### DATOS DEL PROYECTO

**PROYECTO:** Rehabilitación Urbana Los Cedr  
**UBICACIÓN:** Lima - Perú  
**CÓDIGO LOTE:** MZ-C-Lote14

#### CARACTERÍSTICAS TÉCNICAS

**ÁREA TOTAL:** 200.00 m<sup>2</sup>  
**PERÍMETRO:** 53.33 ml  
**FRENTE:** 10.00 ml  
**FONDO:** 10.00 ml

#### LINDEROS Y COLINDANCIAS

**NORTE:** Av. Los Alamos  
**SUR:** Lote 05  
**OESTE:** Lote 13  
**ESTE:** Lote 15

#### INFORMACIÓN LEGAL

**FECHA:** 24 de enero de 2026  
**ESCALA:** Ver indicación

### PLANO PERIMÉTRICO

Habilitación Urbana Los Cedros - MZ-C-Lote14

PLANO DE UBICACIÓN

Habilitación Urbana Los Cedros - MZ-C-Lote14



MAPA DE UBICACIÓN

(Requiere integración con servicio de mapas)

Lat: -76.979390°  
Lng: -12.023359°  
UTM: 284504.56, 8670087.74

DATOS DE UBICACIÓN

Departamento: Lima  
Provincia: Lima  
Distrito: Habilitación Urbana Los Cedros  
Zona UTM: 18S