

PLANOS PRO

Sistema Profesional de Generación de Planos

PROYECTO:

Habilitación Urbana Los Cedros

LOTE:

MZ-C-Lote14

DOCUMENTO: MEMORIA DESCRIPTIVA

FECHA: 24 de enero de 2026

MEMORIA DESCRIPTIVA

I. IDENTIFICACIÓN DEL PREDIO

Código Catastral:	MZ-C-Lote14
Nombre del Lote:	Habilitación Urbana Los Cedros - MZ-C-Lote14
Manzana:	C
Etapas:	Habilitación Urbana Los Cedros
Número de Lote:	14
Estado:	LIBRE

II. UBICACIÓN GEOGRÁFICA

Sistema de Coordenadas:	UTM WGS84 - Zona 18S
Datum:	WGS84
Hemisferio:	Sur

III. CARACTERÍSTICAS MÉTRICAS DEL PREDIO

ÁREA TOTAL:	200.00 m ²
PERÍMETRO TOTAL:	53.33 ml
Frente:	10.00 ml
Fondo:	10.00 ml
Lado Derecho:	20.00 ml
Lado Izquierdo:	20.00 ml

IV. LINDEROS Y COLINDANCIAS

El predio tiene los siguientes linderos y colindancias:

PLANOS PRO

Sistema Profesional de Generación de Planos

PROYECTO:

Habilitación Urbana Los Cedros

LOTE:

MZ-C-Lote14

DOCUMENTO: MEMORIA DESCRIPTIVA

FECHA: 24 de enero de 2026

Por el NORTE: Con calle "Av. Los Alamos"

Por el SUR: Con lote "Lote 05"

Por el OESTE: Con lote "Lote 13"

Por el ESTE: Con lote "Lote 15"

V. CUADRO DE DATOS TÉCNICOS - COORDENADAS UTM

VÉRTICE	LADO	ESTE (m)	NORTE (m)
V1	V1-V2	284500.00	8670100.00
V2	V2-V3	284508.23	8670090.98
V3	V3-V4	284510.00	8670080.00
V4	V4-V1	284500.00	8670080.00

PROPIETARIO



Firma y Sello

PROFESIONAL RESPONSABLE

Ing. Civil / Arquitecto

Este documento ha sido generado automáticamente por el sistema PLANOS PRO

Código de Verificación: MZ-C-Lote14-MKT8QVFS

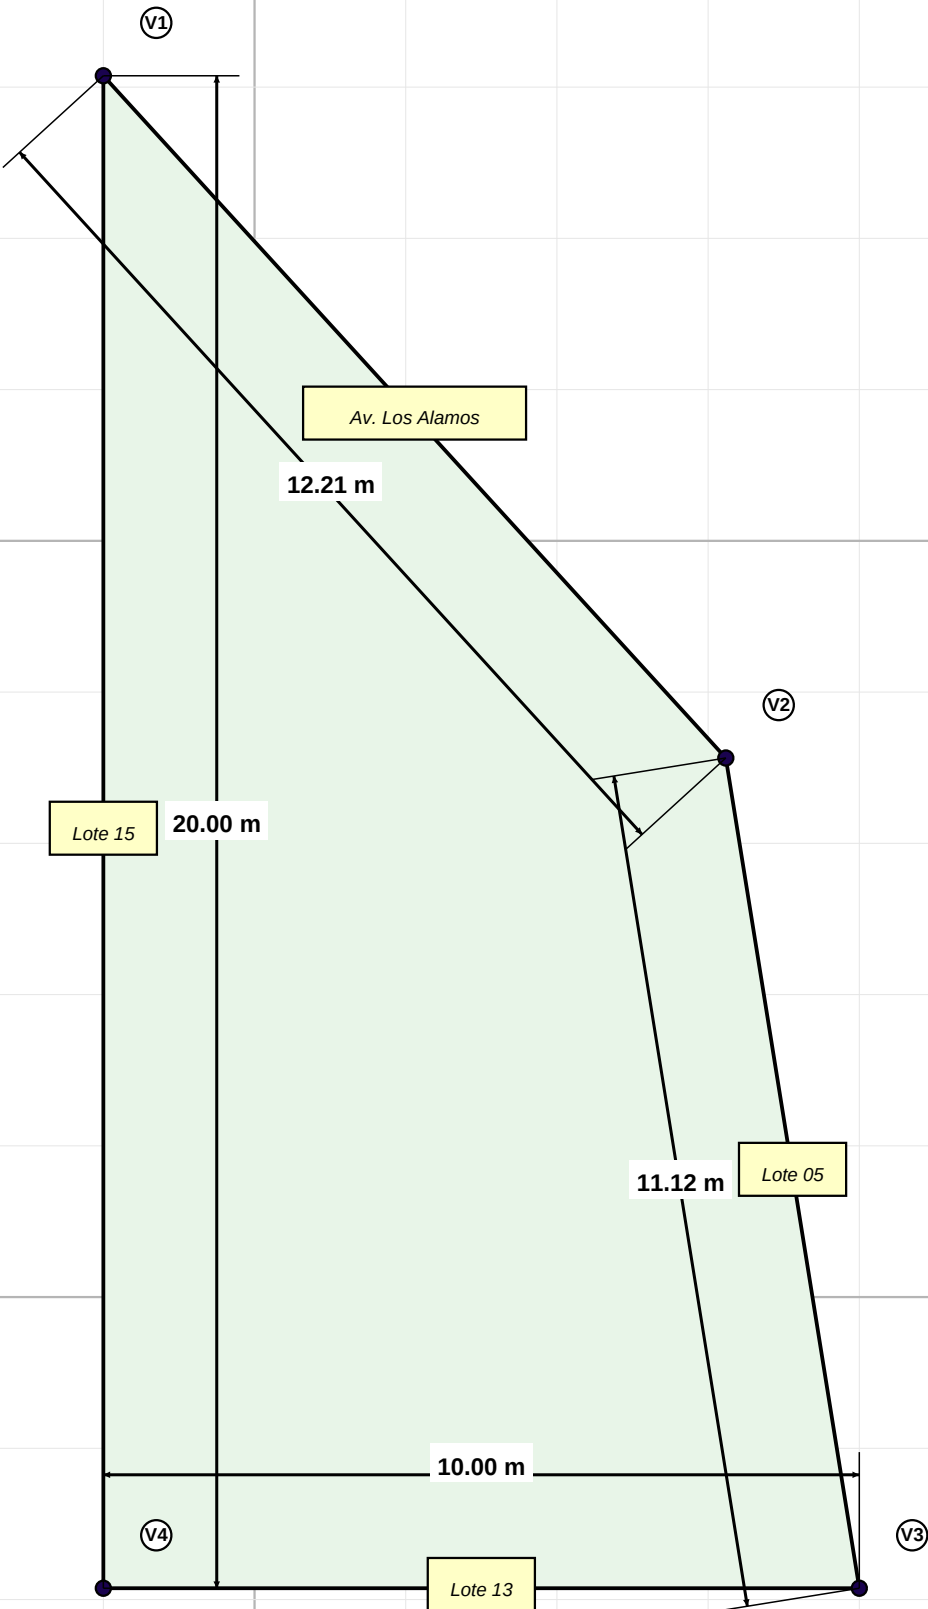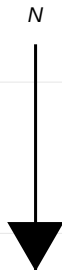

CUADRO TÉCNICO DE COORDENADAS

SISTEMA:

UTM - Universal Transversa de Mercator

DATUM:

WGS84 - World Geodetic System 1984

ZONA UTM:

18 SUR

ESCALA:

1:100

VÉRT.	LADO	DIST. LADO	ANG. INT	ESTE (m)	NORTE (m)
V1	V1-V2	12.21	317°36'43"	284500.00	8670100.00
V2	V2-V3	11.12	213°15'02"	284508.23	8670090.98
V3	V3-V4	10.00	279°08'13"	284510.00	8670080.00
V4	V4-V1	20.00	270°00'00"	284500.00	8670080.00

CAJETÍN TÉCNICO

DATOS DEL PROYECTO

PROYECTO: Rehabilitación Urbana Los Cedr

UBICACIÓN: Lima - Perú

CÓDIGO LOTE: MZ-C-Lote14

CARACTERÍSTICAS TÉCNICAS

ÁREA TOTAL: 200.00 m²

PERÍMETRO: 53.33 ml

FRENTE: 10.00 ml

FONDO: 10.00 ml

LINDEROS Y COLINDANCIAS

NORTE: Av. Los Alamos

SUR: Lote 05

OESTE: Lote 13

ESTE: Lote 15

INFORMACIÓN LEGAL

FECHA: 24 de enero de 2026

ESCALA: Ver indicación

PLANO PERIMÉTRICO

Habilitación Urbana Los Cedros - MZ-C-Lote14

PLANO DE UBICACIÓN

Habilitación Urbana Los Cedros - MZ-C-Lote14



MAPA DE UBICACIÓN

(Requiere integración con servicio de mapas)

Lat: -76.979390°
Lng: -12.023359°
UTM: 284504.56, 8670087.74

DATOS DE UBICACIÓN

Departamento: Lima
Provincia: Lima
Distrito: Habilitación Urbana Los Cedros
Zona UTM: 18S