

PLANOS PRO

Sistema Profesional de Generación de Planos

PROYECTO:

Habilitación Urbana Los Cedros

LOTE:

MZ-C-Lote14

DOCUMENTO: MEMORIA DESCRIPTIVA

FECHA: 25 de enero de 2026

MEMORIA DESCRIPTIVA

I. IDENTIFICACIÓN DEL PREDIO

Código Catastral:	MZ-C-Lote14
Nombre del Lote:	Habilitación Urbana Los Cedros - MZ-C-Lote14
Manzana:	C
Etapas:	Habilitación Urbana Los Cedros
Número de Lote:	14
Estado:	LIBRE

II. UBICACIÓN GEOGRÁFICA

Sistema de Coordenadas:	UTM WGS84 - Zona 18S
Datum:	WGS84
Hemisferio:	Sur

III. CARACTERÍSTICAS MÉTRICAS DEL PREDIO

ÁREA TOTAL:	200.00 m ²
PERÍMETRO TOTAL:	26.62 ml
Frente:	10.00 ml
Fondo:	10.00 ml
Lado Derecho:	20.00 ml
Lado Izquierdo:	20.00 ml

IV. LINDEROS Y COLINDANCIAS

El predio tiene los siguientes linderos y colindancias:

PLANOS PRO

Sistema Profesional de Generación de Planos

PROYECTO:

Habilitación Urbana Los Cedros

LOTE:

MZ-C-Lote14

DOCUMENTO: MEMORIA DESCRIPTIVA

FECHA: 25 de enero de 2026

Por el NORTE: Con calle "Av. Los Alamos"

Por el SUR: Con lote "Lote 05"

Por el OESTE: Con lote "Lote 13"

Por el ESTE: Con lote "Lote 15"

V. CUADRO DE DATOS TÉCNICOS - COORDENADAS UTM

VÉRTICE	LADO	ESTE (m)	NORTE (m)
V1	V1-V2	284504.99	8670082.10
V2	V2-V3	284503.93	8670085.16
V3	V3-V4	284510.00	8670080.00
V4	V4-V1	284500.00	8670080.00

PROPIETARIO


Firma y Sello

PROFESIONAL RESPONSABLE

Ing. Civil / Arquitecto

Este documento ha sido generado automáticamente por el sistema PLANOS PRO

Código de Verificación: MZ-C-Lote14-MKTW8VVL

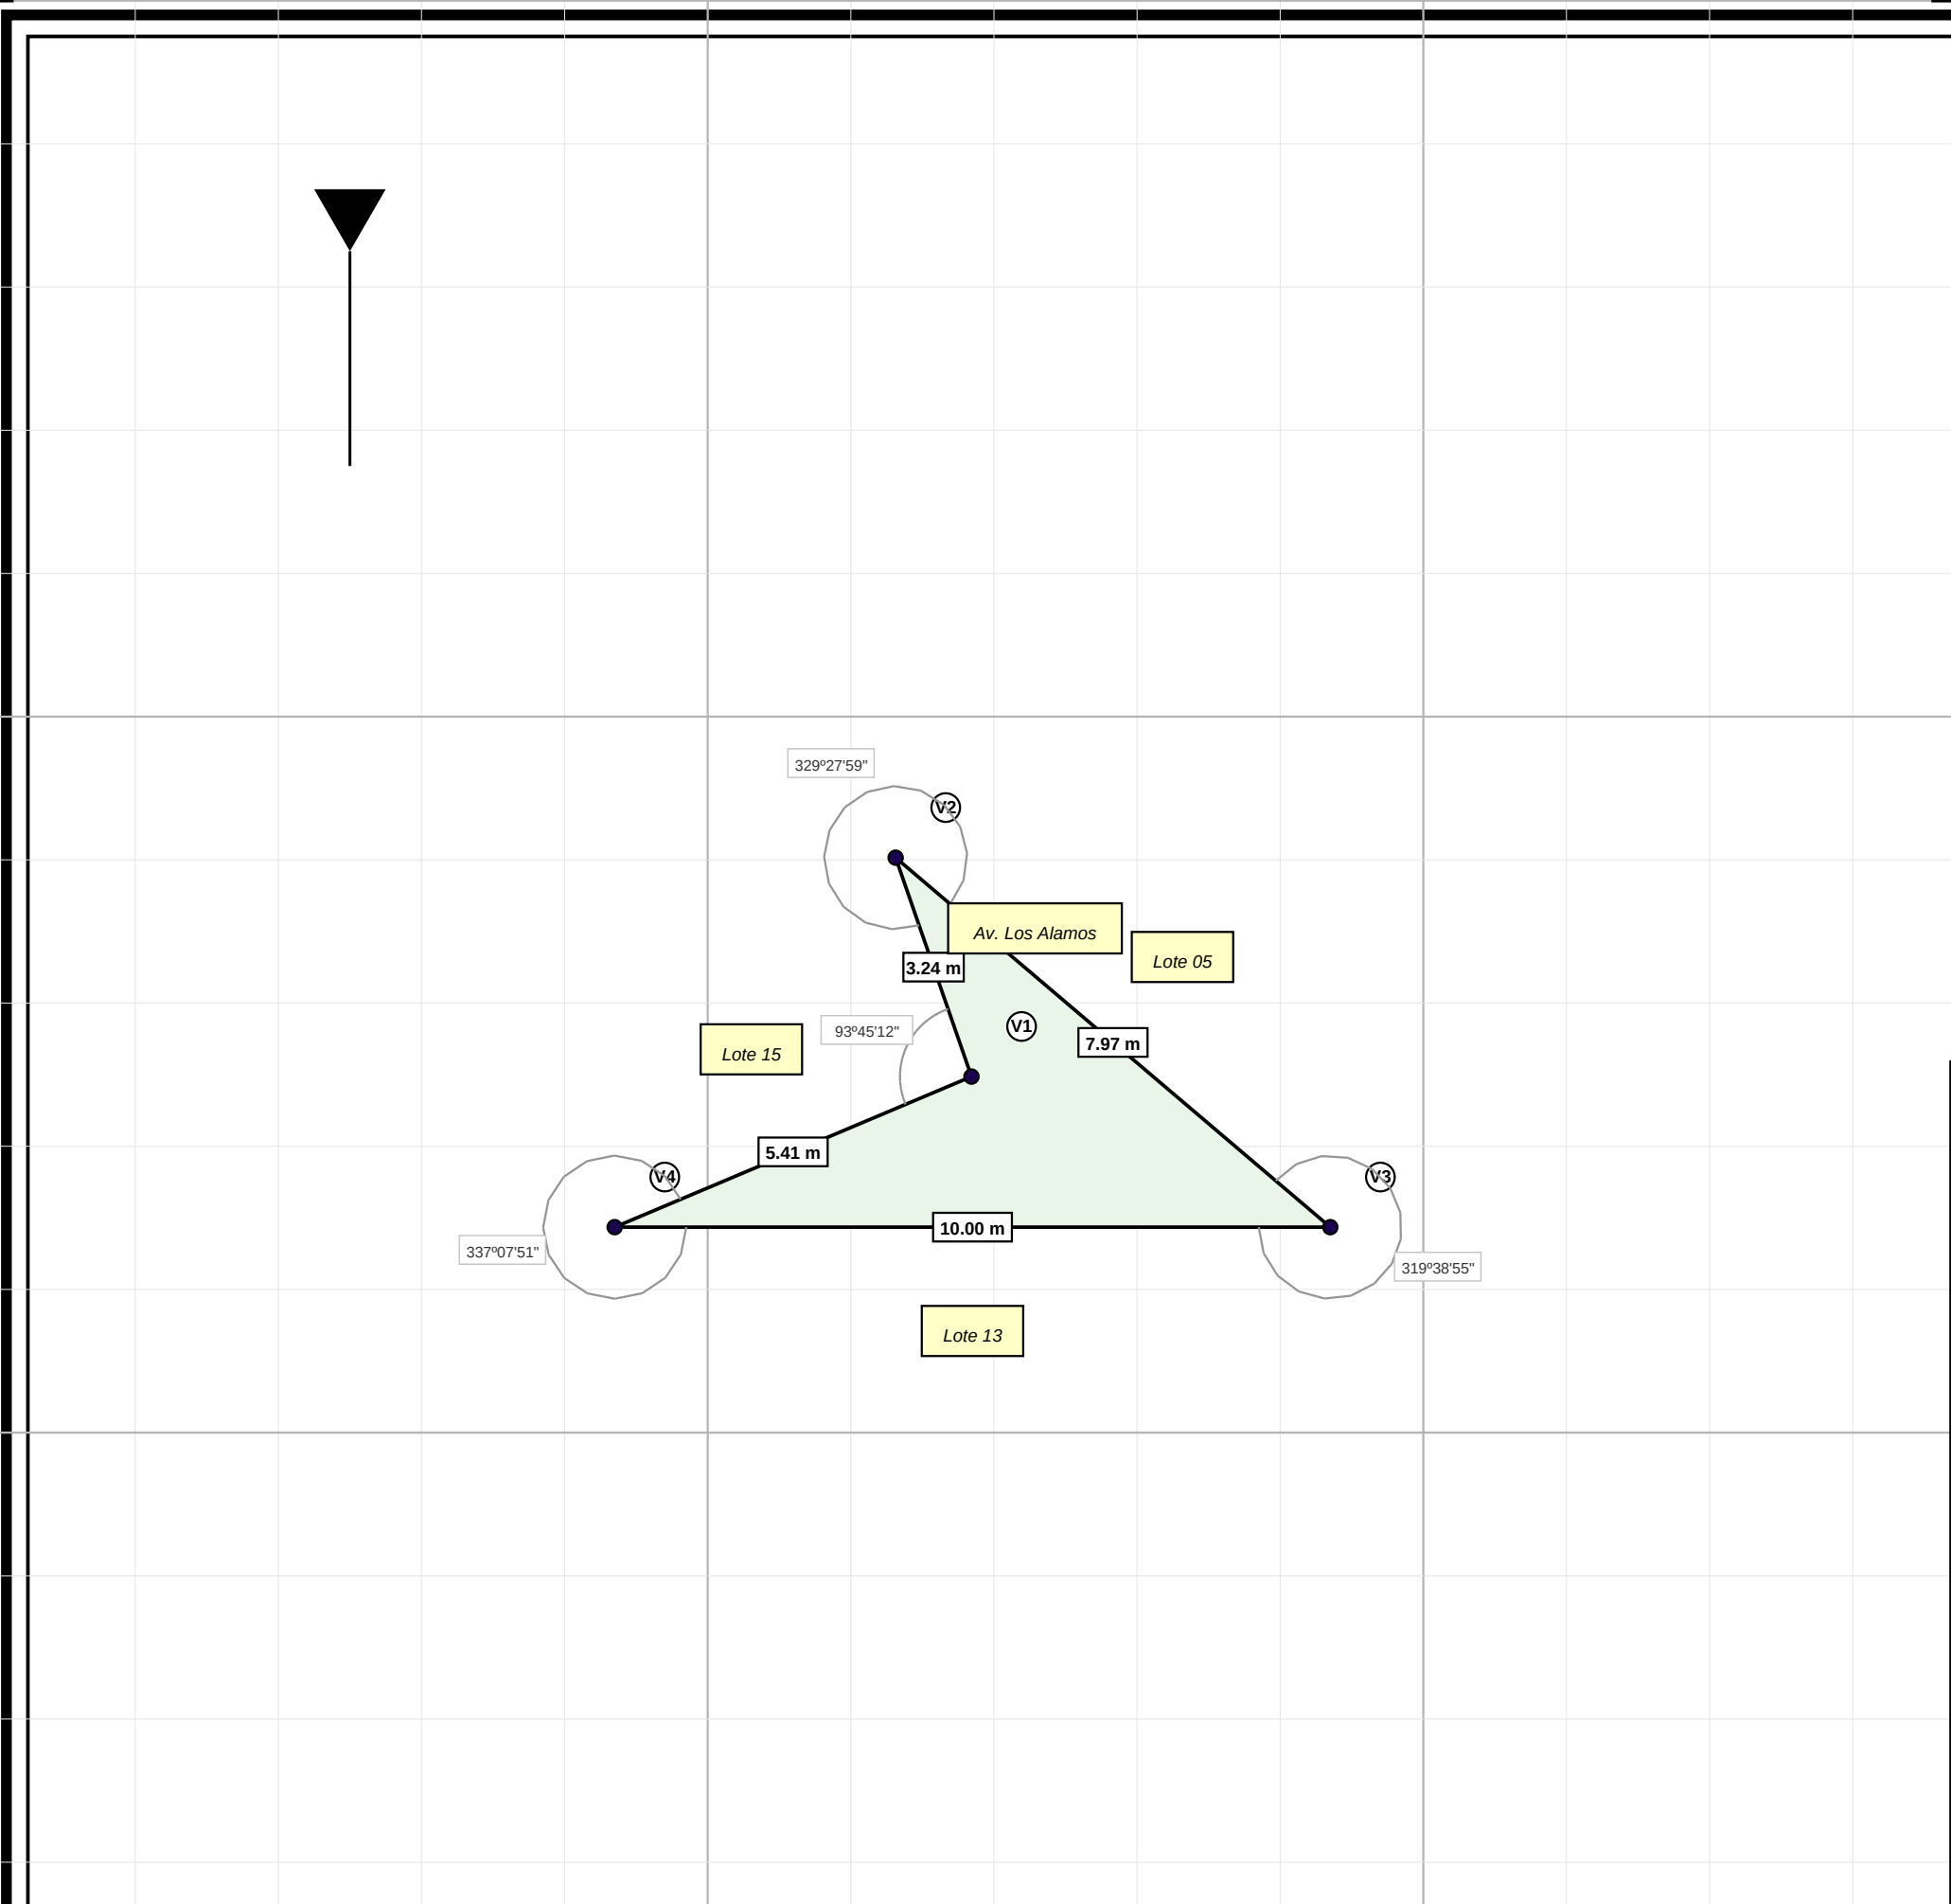

CUADRO TECNICO DE COORDENADAS UTM WGS84					
VÉRT.	LADO	DIST. LADO	ANG. INT	ESTE (m)	NORTE (m)
V1	V1-V2	3.24	93°45'12"	284504.99	8670082.10
V2	V2-V3	7.97	329°27'59"	284503.93	8670085.16
V3	V3-V4	10.00	319°38'55"	284510.00	8670080.00
V4	V4-V1	5.41	337°07'51"	284500.00	8670080.00

ESCALA:

1:100

PLANO PERIMETRICO	
DATOS DEL PROYECTO	
PROYECTO:	Habilitación Urbana Los Cedros
CÓDIGO:	MZ-C-Lote14
MANZANA:	C
ÁREA:	200.00 m²
LOTE:	14
PERÍM:	26.62 m
INFORMACIÓN LEGAL	
FECHA:	25 de enero de 2026
PROFESIONAL:	Ing. Responsable
REGISTRO:	CIP/CAP
Firma y Sello del Profesional	

PLANO PERIMÉTRICO

Habilitación Urbana Los Cedros - MZ-C-Lote14

PLANO DE UBICACIÓN

Habilitación Urbana Los Cedros - MZ-C-Lote14



MAPA DE UBICACIÓN

(Requiere integración con servicio de mapas)

Lat: -76.979389°
Lng: -12.023413°
UTM: 284504.73, 8670081.82

DATOS DE UBICACIÓN

Departamento: Lima
Provincia: Lima
Distrito: Habilitación Urbana Los Cedros
Zona UTM: 18S