

PLANOS PRO

Sistema Profesional de Generación de Planos

PROYECTO:

Habilitación Urbana Los Cedros

LOTE:

MZ-C-Lote14

DOCUMENTO: MEMORIA DESCRIPTIVA

FECHA: 25 de enero de 2026

MEMORIA DESCRIPTIVA

I. IDENTIFICACIÓN DEL PREDIO

Código Catastral:	MZ-C-Lote14
Nombre del Lote:	Habilitación Urbana Los Cedros - MZ-C-Lote14
Manzana:	C
Etapas:	Habilitación Urbana Los Cedros
Número de Lote:	14
Estado:	LIBRE

II. UBICACIÓN GEOGRÁFICA

Sistema de Coordenadas:	UTM WGS84 - Zona 18S
Datum:	WGS84
Hemisferio:	Sur

III. CARACTERÍSTICAS MÉTRICAS DEL PREDIO

ÁREA TOTAL:	200.00 m ²
PERÍMETRO TOTAL:	55.41 ml
Frente:	10.00 ml
Fondo:	10.00 ml
Lado Derecho:	20.00 ml
Lado Izquierdo:	20.00 ml

IV. LINDEROS Y COLINDANCIAS

El predio tiene los siguientes linderos y colindancias:

PLANOS PRO

Sistema Profesional de Generación de Planos

PROYECTO:

Habilitación Urbana Los Cedros

LOTE:

MZ-C-Lote14

DOCUMENTO: MEMORIA DESCRIPTIVA

FECHA: 25 de enero de 2026

Por el NORTE: Con calle "Av. Los Alamos"

Por el SUR: Con lote "Lote 05"

Por el OESTE: Con lote "Lote 13"

Por el ESTE: Con lote "Lote 15"

V. CUADRO DE DATOS TÉCNICOS - COORDENADAS UTM

VÉRTICE	LADO	ESTE (m)	NORTE (m)
V1	V1-V2	284500.00	8670100.00
V2	V2-V3	284511.27	8670090.77
V3	V3-V4	284510.00	8670080.00
V4	V4-V1	284500.00	8670080.00

PROPIETARIO

Firma y Sello


PROFESIONAL RESPONSABLE

Ing. Civil / Arquitecto

Este documento ha sido generado automáticamente por el sistema PLANOS PRO

Código de Verificación: MZ-C-Lote14-MKU0LQW7

PLANO PERIMÉTRICO

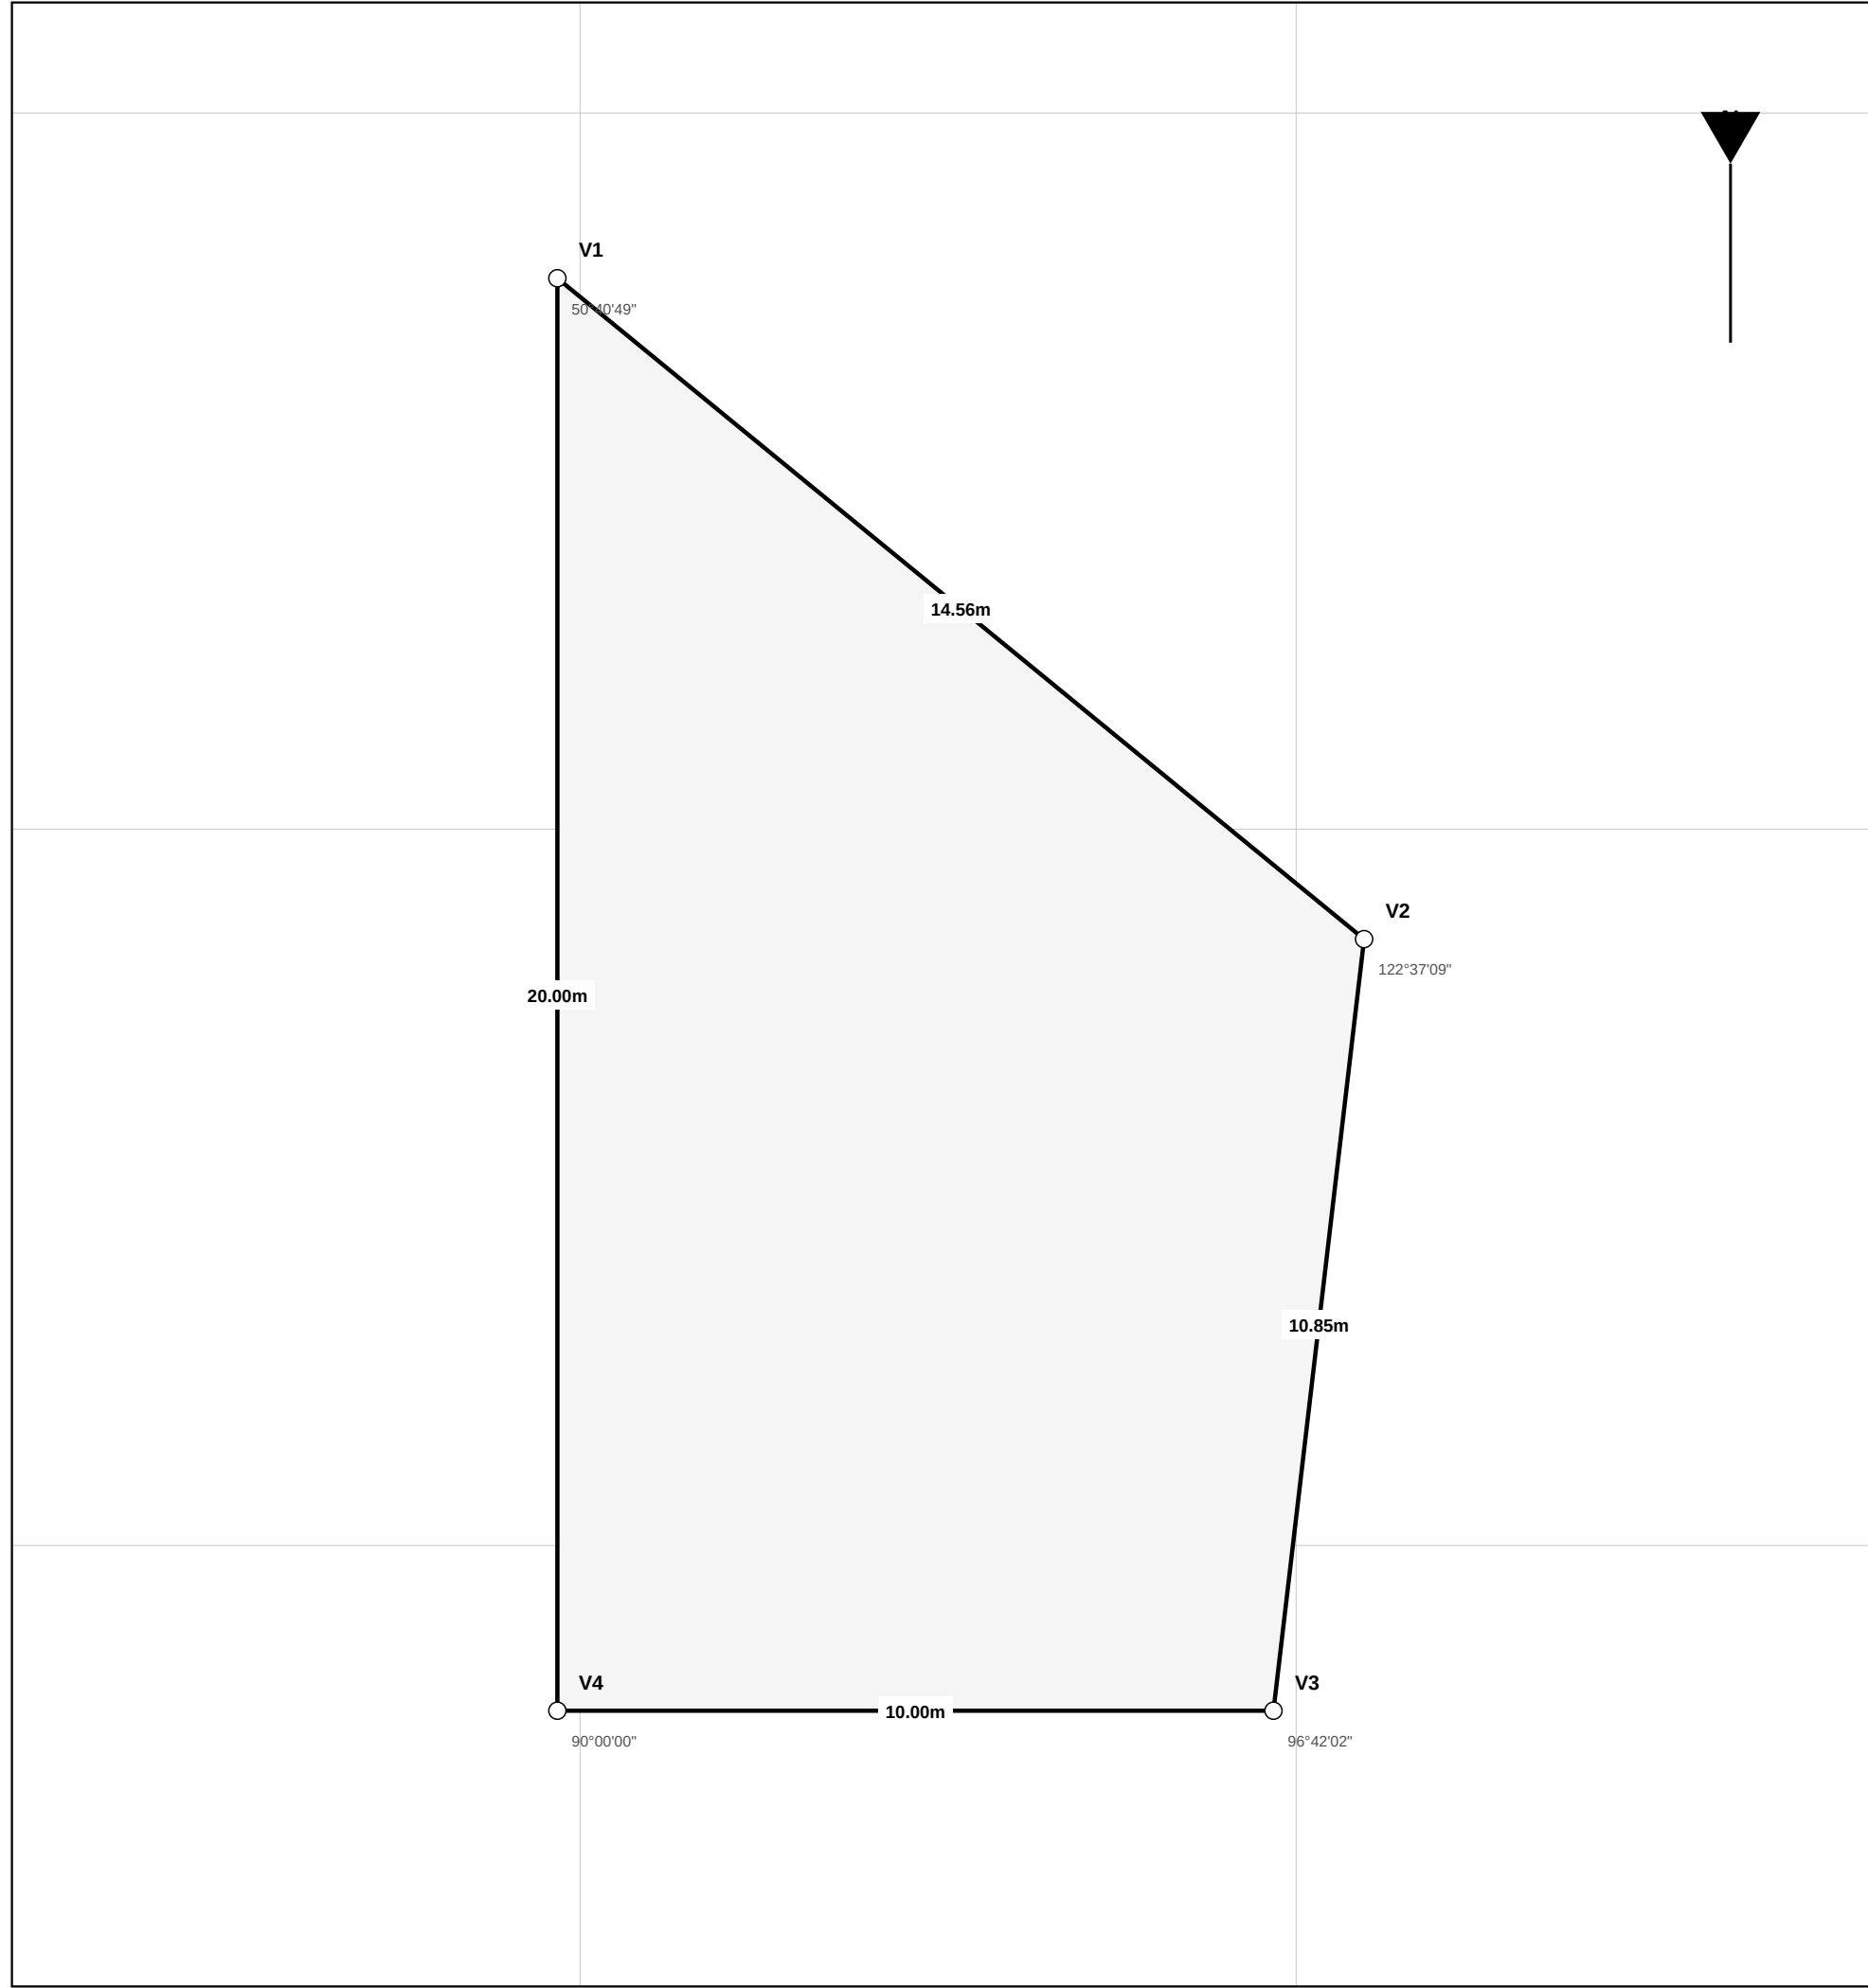

CUADRO DE DATOS TÉCNICOS - UTM WGS84					
VÉRTICE	LADO	DIST (m)	ÁNGULO INT.	ESTE (X)	NORTE (Y)
V-1	V1-V2	14.56	50°40'49"	284500.000	8670100.000
V-2	V2-V3	10.85	122°37'09"	284511.266	8670090.773
V-3	V3-V4	10.00	96°42'02"	284510.000	8670080.000
V-4	V4-V1	20.00	90°00'00"	284500.000	8670080.000

PLANO
PERIMÉTRICO

PROYECTO: Habitación Urbana Los Cedros

MANZANA: C LOTE: 14

ÁREA: 200.00 m²

PERÍMETRO: 55.41 ml

ESCALA: 1:100

FIRMA Y SELLO PROFESIONAL:

FECHA: 25/1/2026

PLANO DE UBICACIÓN

Habilitación Urbana Los Cedros - MZ-C-Lote14



MAPA DE UBICACIÓN

(Requiere integración con servicio de mapas)

Lat: -76.979383°
Lng: -12.023359°
UTM: 284505.32, 8670087.69

DATOS DE UBICACIÓN

Departamento: Lima
Provincia: Lima
Distrito: Habilitación Urbana Los Cedros
Zona UTM: 18S