

PLANOS PRO

Sistema Profesional de Generación de Planos

PROYECTO:

Habilitación Urbana Los Cedros

LOTE:

MZ-C-Lote14

DOCUMENTO: MEMORIA DESCRIPTIVA

FECHA: 25 de enero de 2026

MEMORIA DESCRIPTIVA

I. IDENTIFICACIÓN DEL PREDIO

Código Catastral:	MZ-C-Lote14
Nombre del Lote:	Habilitación Urbana Los Cedros - MZ-C-Lote14
Manzana:	C
Etapas:	Habilitación Urbana Los Cedros
Número de Lote:	14
Estado:	LIBRE

II. UBICACIÓN GEOGRÁFICA

Sistema de Coordenadas:	UTM WGS84 - Zona 18S
Datum:	WGS84
Hemisferio:	Sur

III. CARACTERÍSTICAS MÉTRICAS DEL PREDIO

ÁREA TOTAL:	200.00 m ²
PERÍMETRO TOTAL:	61.00 ml
Frente:	10.00 ml
Fondo:	10.00 ml
Lado Derecho:	20.00 ml
Lado Izquierdo:	20.00 ml

IV. LINDEROS Y COLINDANCIAS

El predio tiene los siguientes linderos y colindancias:

PLANOS PRO

Sistema Profesional de Generación de Planos

PROYECTO:

Habilitación Urbana Los Cedros

LOTE:

MZ-C-Lote14

DOCUMENTO: MEMORIA DESCRIPTIVA

FECHA: 25 de enero de 2026

Por el NORTE: Con calle "Av. Los Alamos"

Por el SUR: Con lote "Lote 05"

Por el OESTE: Con lote "Lote 13"

Por el ESTE: Con lote "Lote 15"

V. CUADRO DE DATOS TÉCNICOS - COORDENADAS UTM

VÉRTICE	LADO	ESTE (m)	NORTE (m)
V1	V1-V2	284502.13	8670090.82
V2	V2-V3	284509.31	8670092.64
V3	V3-V4	284510.00	8670080.00
V4	V4-V5	284496.04	8670084.59
V5	V5-V6	284491.90	8670091.68
V6	V6-V1	284494.36	8670098.41

PROPIETARIO

Firma y Sello


PROFESIONAL RESPONSABLE

Ing. Civil / Arquitecto

Este documento ha sido generado automáticamente por el sistema PLANOS PRO

Código de Verificación: MZ-C-Lote14-MKU1GSL3

PLANO PERIMÉTRICO

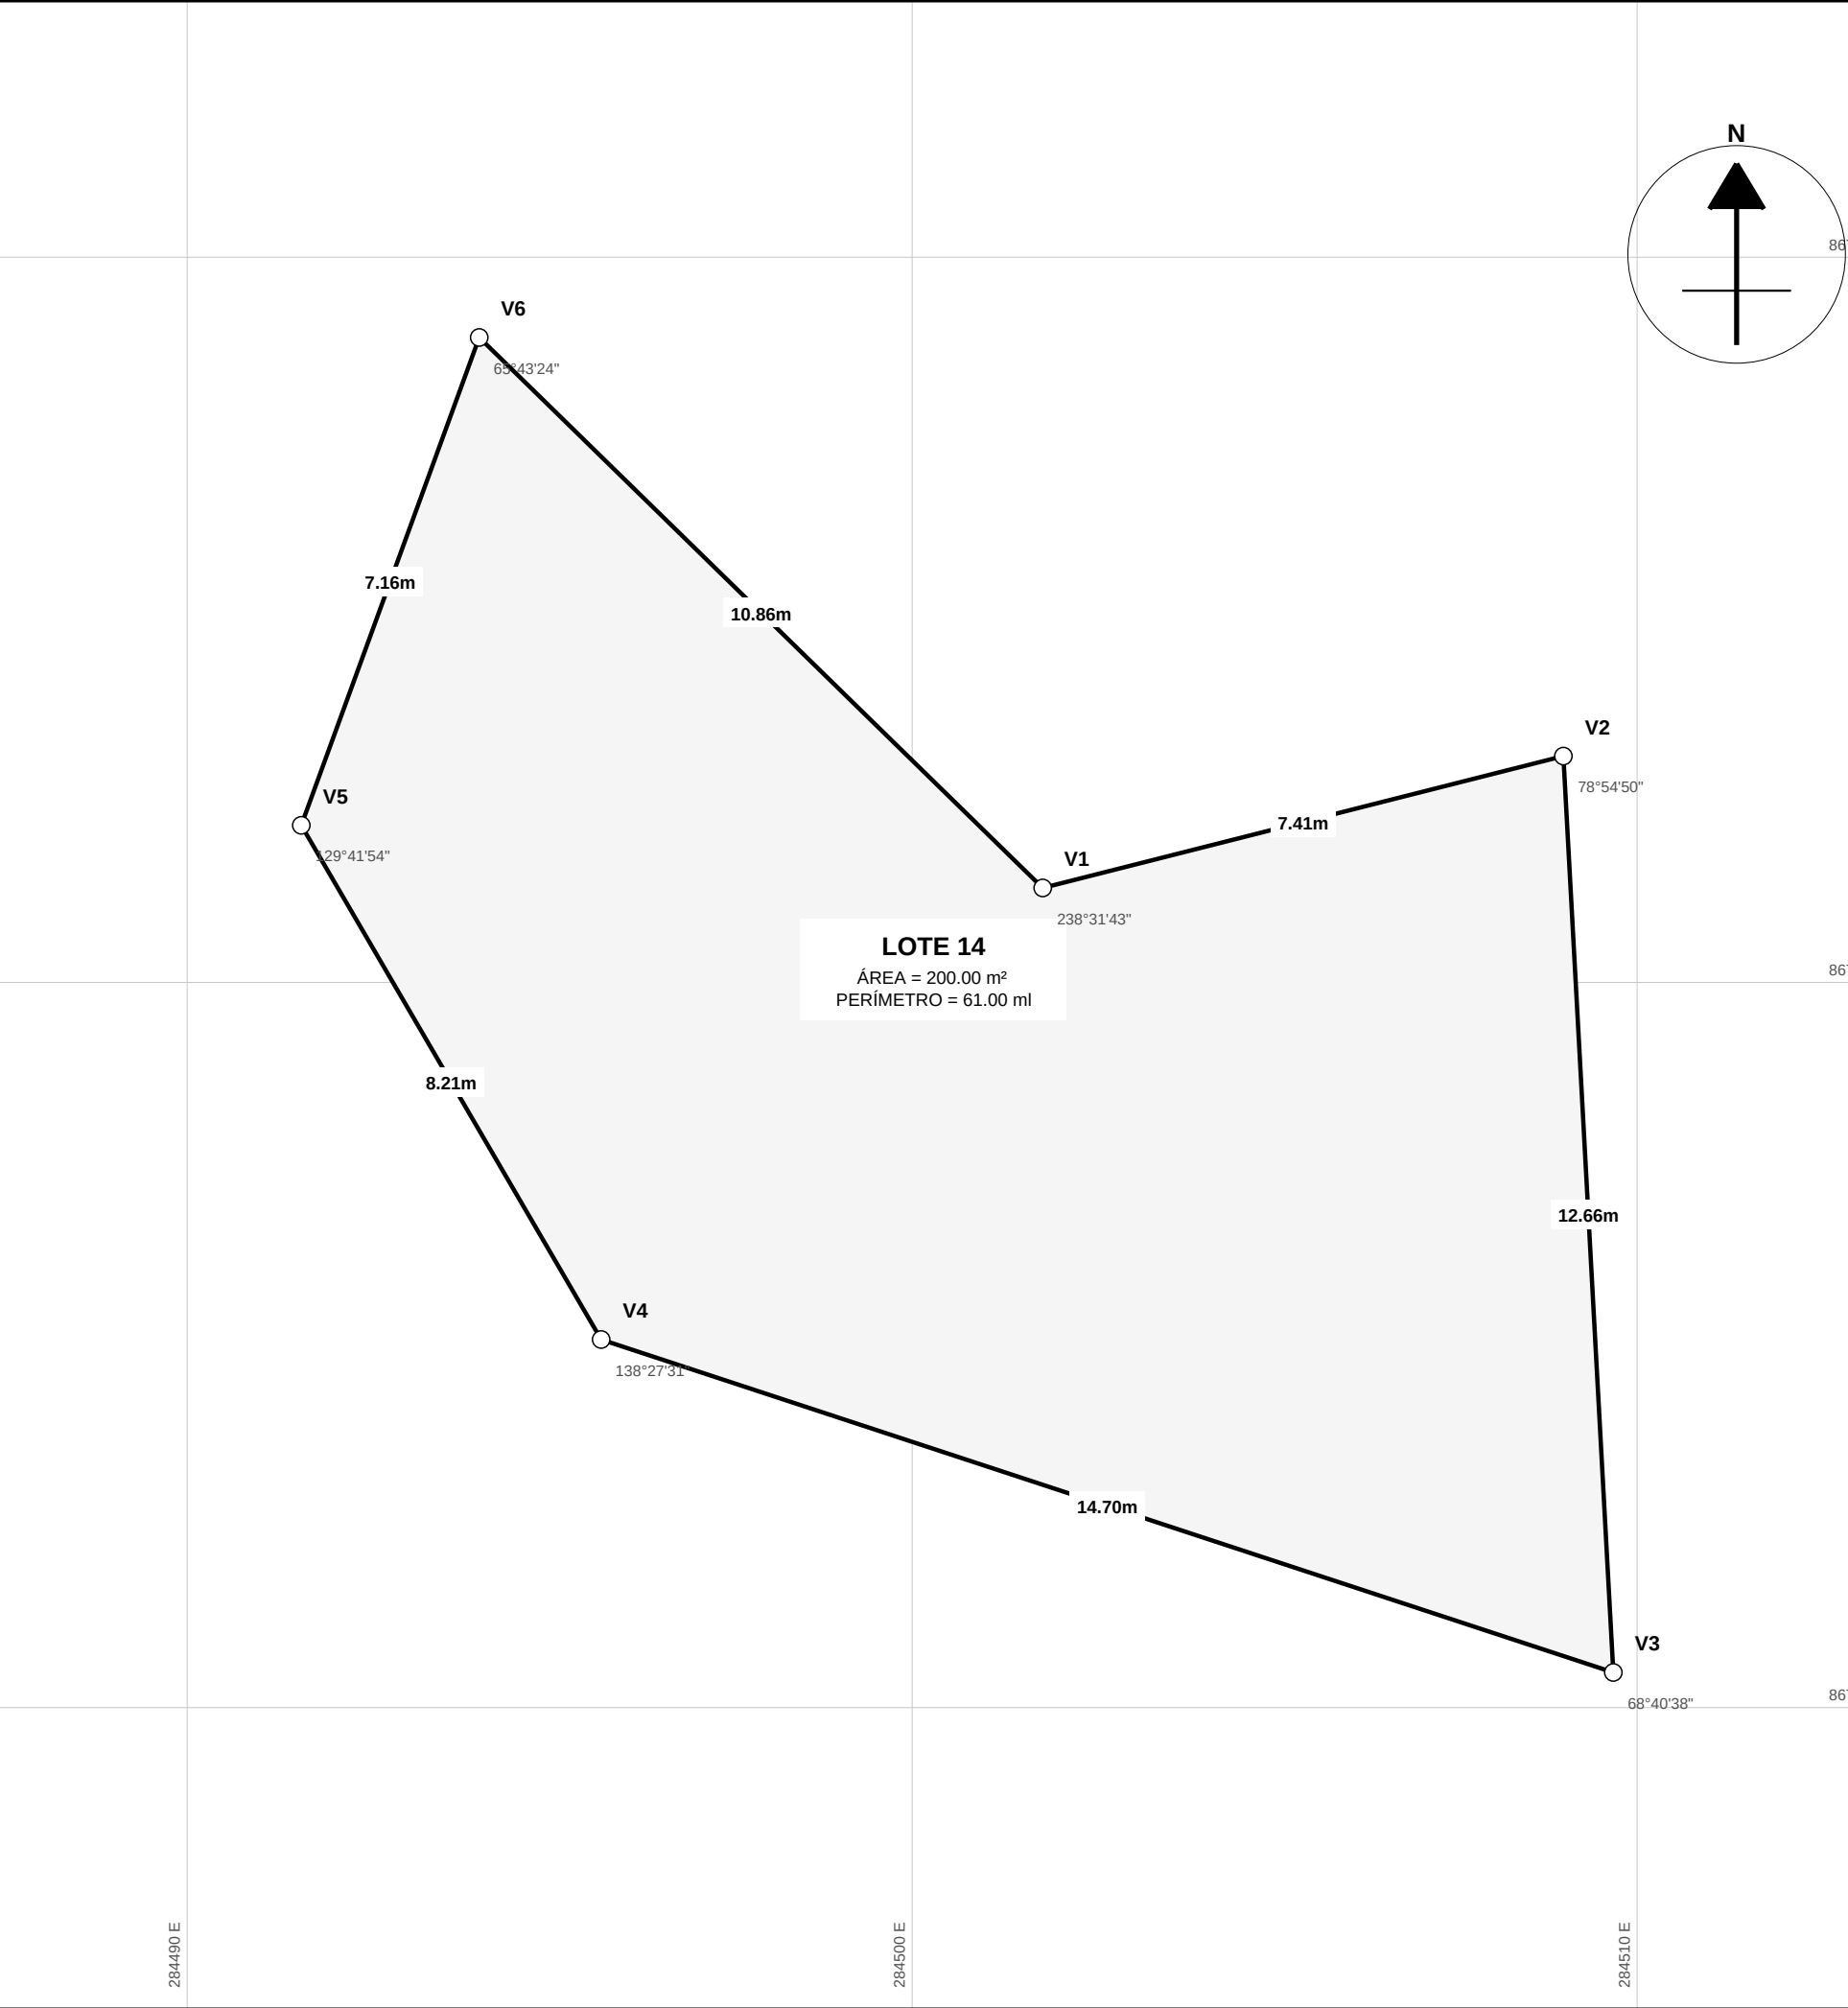

CUADRO DE DATOS TÉCNICOS - UTM WGS84					
VERTICE	LADO	DIST (m)	ÁNGULO INT.	ESTE (X)	NORTE (Y)
V-1	V1-V2	7.41	238°31'43"	284502.129	8670090.818
V-2	V2-V3	12.66	78°54'50"	284509.311	8670092.636
V-3	V3-V4	14.70	68°40'38"	284510.000	8670080.000
V-4	V4-V5	8.21	138°27'31"	284496.038	8670084.591
V-5	V5-V6	7.16	129°41'54"	284491.902	8670091.682
V-6	V6-V1	10.86	65°43'24"	284494.357	8670098.409

PLANO PERIMÉTRICO		FIRMA Y SELLO PROFESIONAL:
PROPIETARIO / PROYECTO: Habilitación Urbana Los Cedros		
UBICACIÓN: Mina. C - Lote 14		
ÁREA TERRENO: 200.00 m² PERÍMETRO: 61.00 ml		
ESCALA: 1:100		FECHA: 25/1/2026

PLANO DE UBICACIÓN

Habilitación Urbana Los Cedros - MZ-C-Lote14



MAPA DE UBICACIÓN

(Requiere integración con servicio de mapas)

Lat: -76.979426°
Lng: -12.023341°
UTM: 284500.62, 8670089.69

DATOS DE UBICACIÓN

Departamento: Lima
Provincia: Lima
Distrito: Habilitación Urbana Los Cedros
Zona UTM: 18S