

PLANOS PRO

Sistema Profesional de Generación de Planos

PROYECTO:

Habilitación Urbana Los Cedros

LOTE:

MZ-C-Lote14

DOCUMENTO: MEMORIA DESCRIPTIVA

FECHA: 25 de enero de 2026

MEMORIA DESCRIPTIVA

I. IDENTIFICACIÓN DEL PREDIO

Código Catastral:	MZ-C-Lote14
Nombre del Lote:	Habilitación Urbana Los Cedros - MZ-C-Lote14
Manzana:	C
Etapas:	Habilitación Urbana Los Cedros
Número de Lote:	14
Estado:	LIBRE

II. UBICACIÓN GEOGRÁFICA

Sistema de Coordenadas:	UTM WGS84 - Zona 18S
Datum:	WGS84
Hemisferio:	Sur

III. CARACTERÍSTICAS MÉTRICAS DEL PREDIO

ÁREA TOTAL:	200.00 m ²
PERÍMETRO TOTAL:	61.64 ml
Frente:	10.00 ml
Fondo:	10.00 ml
Lado Derecho:	20.00 ml
Lado Izquierdo:	20.00 ml

IV. LINDEROS Y COLINDANCIAS

El predio tiene los siguientes linderos y colindancias:

PLANOS PRO

Sistema Profesional de Generación de Planos

PROYECTO:

Habilitación Urbana Los Cedros

LOTE:

MZ-C-Lote14

DOCUMENTO: MEMORIA DESCRIPTIVA

FECHA: 25 de enero de 2026

Por el NORTE: Con calle "Av. Los Alamos"

Por el SUR: Con lote "Lote 05"

Por el OESTE: Con lote "Lote 13"

Por el ESTE: Con lote "Lote 15"

V. CUADRO DE DATOS TÉCNICOS - COORDENADAS UTM

VÉRTICE	LADO	ESTE (m)	NORTE (m)
V1	V1-V2	284495.58	8670094.09
V2	V2-V3	284510.00	8670100.00
V3	V3-V4	284510.00	8670080.00
V4	V4-V5	284504.36	8670084.45
V5	V5-V1	284495.49	8670084.09

PROPIETARIO

Firma y Sello

PROFESIONAL RESPONSABLE

Ing. Civil / Arquitecto


Este documento ha sido generado automáticamente por el sistema PLANOS PRO

Código de Verificación: MZ-C-Lote14-MKU4WIWF

PLANO PERIMÉTRICO



PLANO DE UBICACIÓN
ESCALA 1/1000

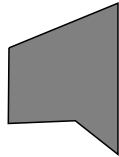

CUADRO DE DATOS TÉCNICOS - UTM WGS84

VÉRTICE	LADO	DIST (m)	ÁNGULO INT.	ESTE (X)	NORTE (Y)
V-1	V1-V2	15.58	112°48'33"	284495.584	8670094.091
V-2	V2-V3	20.00	67°42'42"	284510.000	8670100.000
V-3	V3-V4	7.19	51°42'54"	284510.000	8670080.000
V-4	V4-V5	8.87	220°38'03"	284504.357	8670084.455
V-5	V5-V1	10.00	87°07'48"	284495.493	8670084.091

PLANO
PERIMÉTRICO

PROPIETARIO / PROYECTO:
Habilitación Urbana Los Cedros

UBICACIÓN:
Mina. C - Lote 14


ÁREA TERRENO: 200.00 m²

PERIMETRO: 61.64 ml

ESCALA: 1:200

FIRMA Y SELLO PROFESIONAL:

FECHA: 25/1/2026

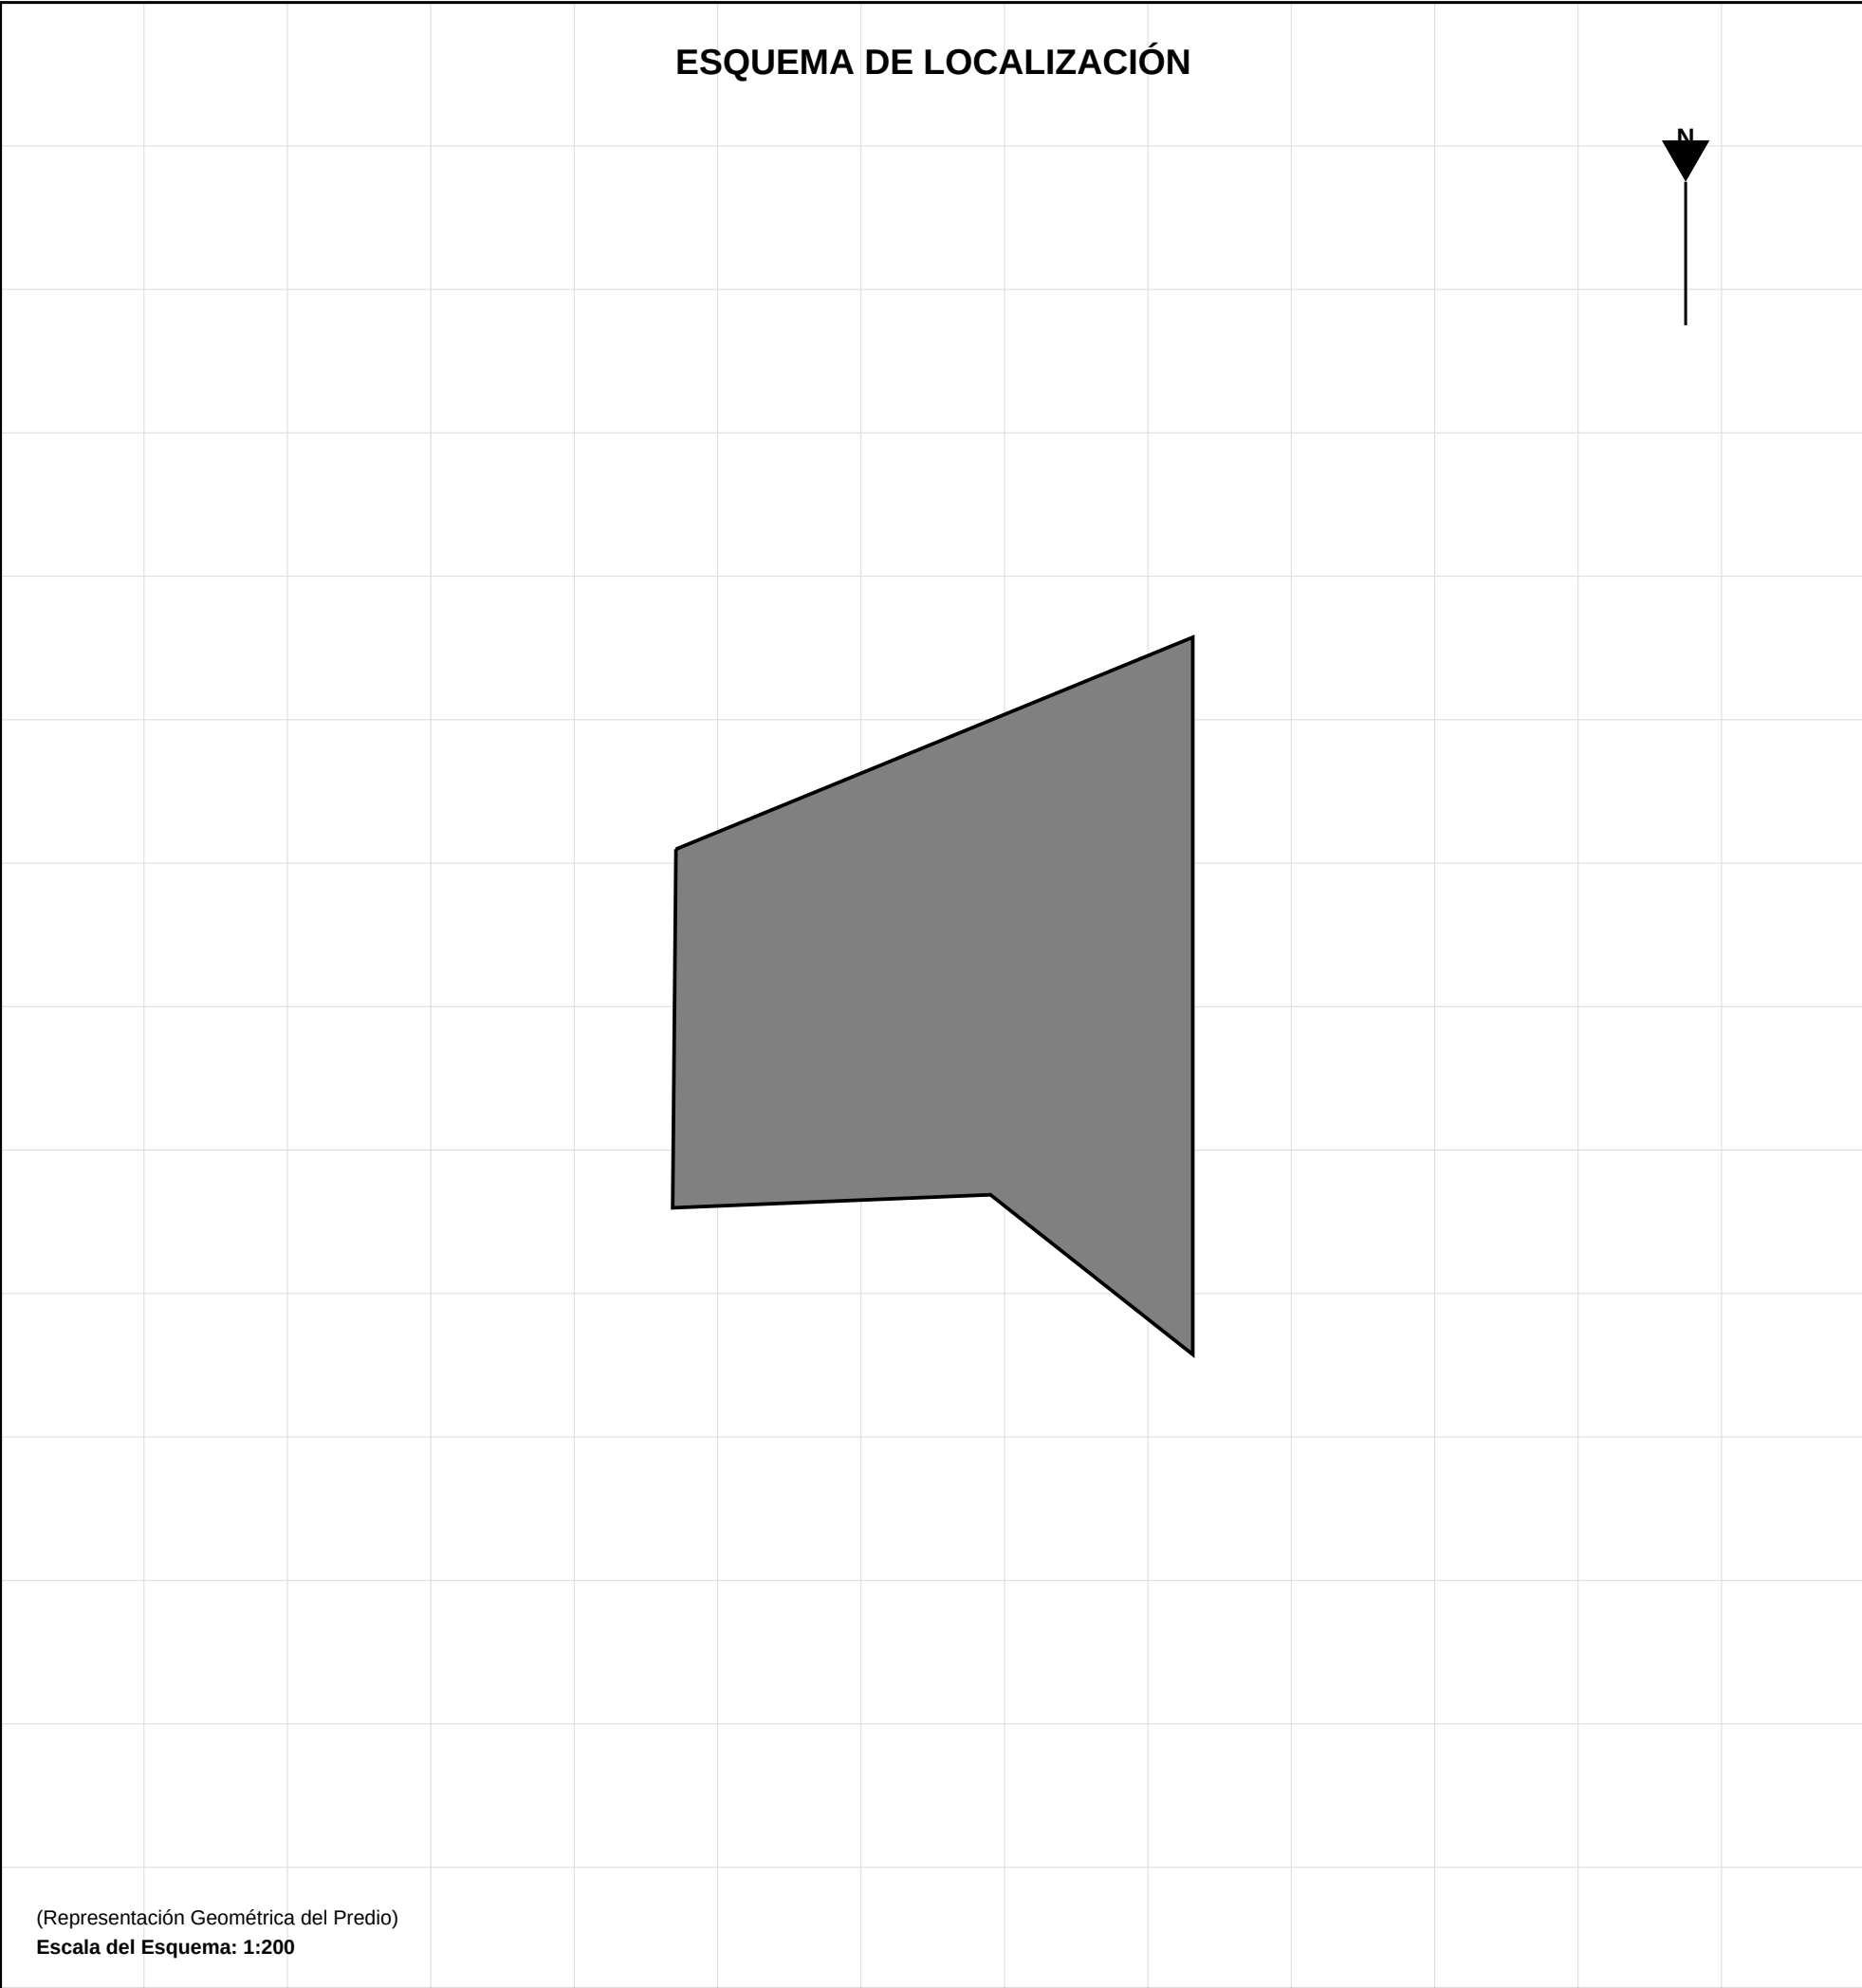

DATOS GENERALES Y NORMATIVOS	
Departamento:	Lima
Provincia:	Lima
Distrito:	Habilitación Urbana Los Cedros
Urbanización/Sector:	Habilitación Urbana Los Cedros - MZ-C-Lote14
Manzana:	C
Lote:	14
---	---
Zonificación:	RDM (Residencial Densidad Media)*
Usos Permisibles:	Unifamiliar / Multifamiliar*
Área Terreno:	200.00 m²
Perímetro:	61.64 ml

* Datos referenciales de zonificación. Verificar Certificado de Parámetros.

COORDENADAS DE LOCALIZACIÓN (CENTROIDE)	
SISTEMA DE REFERENCIA:	WGS-84 / ZONA 18S
COORDENADAS UTM:	
ESTE (X): 284503.087 m	NORTE (Y): 8670088.527 m
COORDENADAS GEOGRÁFICAS:	
LATITUD: -76.9794035°	LONGITUD: -12.0233518°

PLANO DE UBICACIÓN		FIRMA Y SELLO:
PROPIETARIO:	---	
UBICACIÓN:	Habilitación Urbana Los Cedros - Mz. C Lt. 14	
LÁMINA:	U-01	
FECHA: 25/1/2026	DIBUJO: AUTOMÁTICO	ESCALA: INDICADA