

PLANOS PRO

Sistema Profesional de Generación de Planos

PROYECTO:

Habilitación Urbana Los Cedros

LOTE:

MZ-C-Lote14

DOCUMENTO: MEMORIA DESCRIPTIVA

FECHA: 25 de enero de 2026

MEMORIA DESCRIPTIVA

I. IDENTIFICACIÓN DEL PREDIO

Código Catastral:	MZ-C-Lote14
Nombre del Lote:	Habilitación Urbana Los Cedros - MZ-C-Lote14
Manzana:	C
Etapas:	Habilitación Urbana Los Cedros
Número de Lote:	14
Estado:	LIBRE

II. UBICACIÓN GEOGRÁFICA

Sistema de Coordenadas:	UTM WGS84 - Zona 18S
Datum:	WGS84
Hemisferio:	Sur

III. CARACTERÍSTICAS MÉTRICAS DEL PREDIO

ÁREA TOTAL:	200.00 m²
PERÍMETRO TOTAL:	6866.63 ml
Frente:	10.00 ml
Fondo:	10.00 ml
Lado Derecho:	20.00 ml
Lado Izquierdo:	20.00 ml

IV. LINDEROS Y COLINDANCIAS

El predio tiene los siguientes linderos y colindancias:

Por el NORTE: Con calle "Av. Los Alamos"

Por el SUR: Con lote "Lote 05"

Por el OESTE: Con lote "Lote 13"

Por el ESTE: Con lote "Lote 15"

V. CUADRO DE DATOS TÉCNICOS - COORDENADAS UTM

VÉRTICE	LADO	ESTE (m)	NORTE (m)
V1	V1-V2	284081.25	8670566.25
V2	V2-V3	284781.11	8670559.09
V3	V3-V4	284795.31	8669784.55
V4	V4-V5	283567.12	8669768.18
V5	V5-V6	283588.10	8669948.86
V6	V6-V7	283140.20	8669990.91
V7	V7-V8	283144.89	8670111.70
V8	V8-V9	283667.61	8670207.16
V9	V9-V10	283644.89	8670329.89
V10	V10-V11	283194.89	8670366.25
V11	V11-V12	283044.89	8670507.16
V12	V12-V13	283158.52	8670598.07
V13	V13-V14	283335.80	8670484.43
V14	V14-V15	283649.43	8670520.80
V15	V15-V1	283353.98	8671011.70


PROPIETARIO

Firma y Sello


PROFESIONAL RESPONSABLE

Ing. Civil / Arquitecto

PLANO PERIMÉTRICO

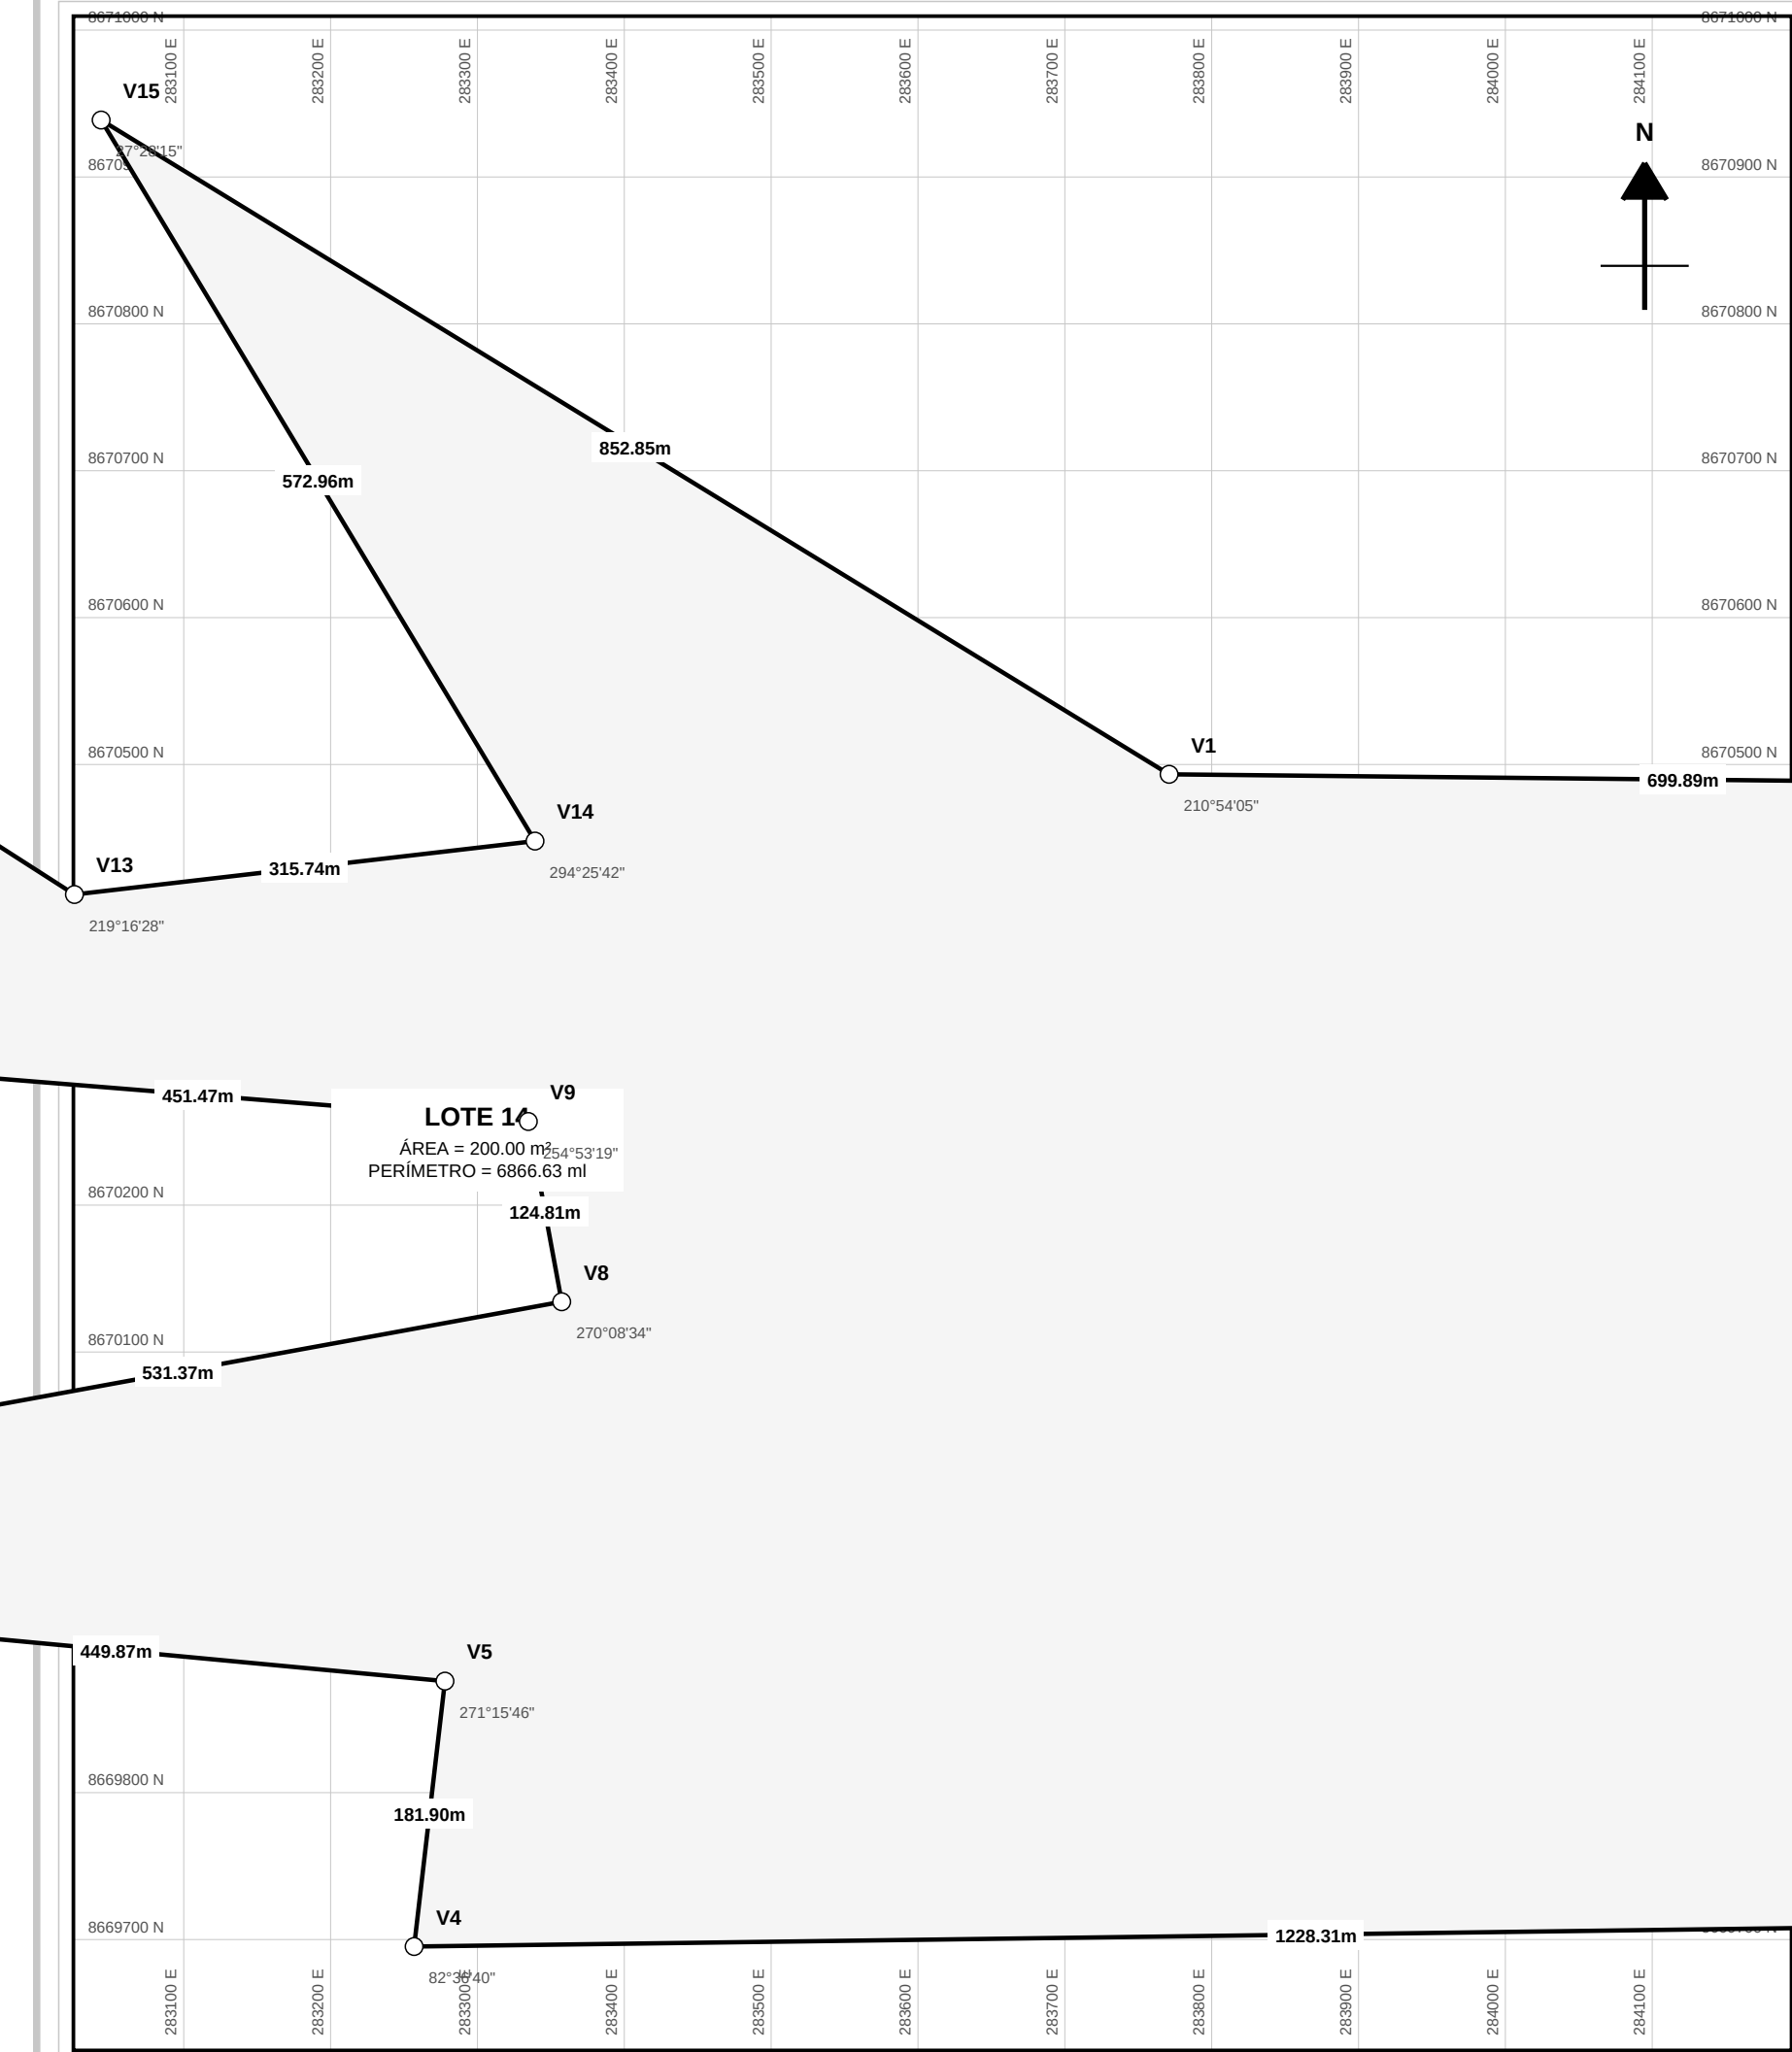


LOTE 14
ÁREA = 200.00 m²
PERÍMETRO = 6866.63 ml

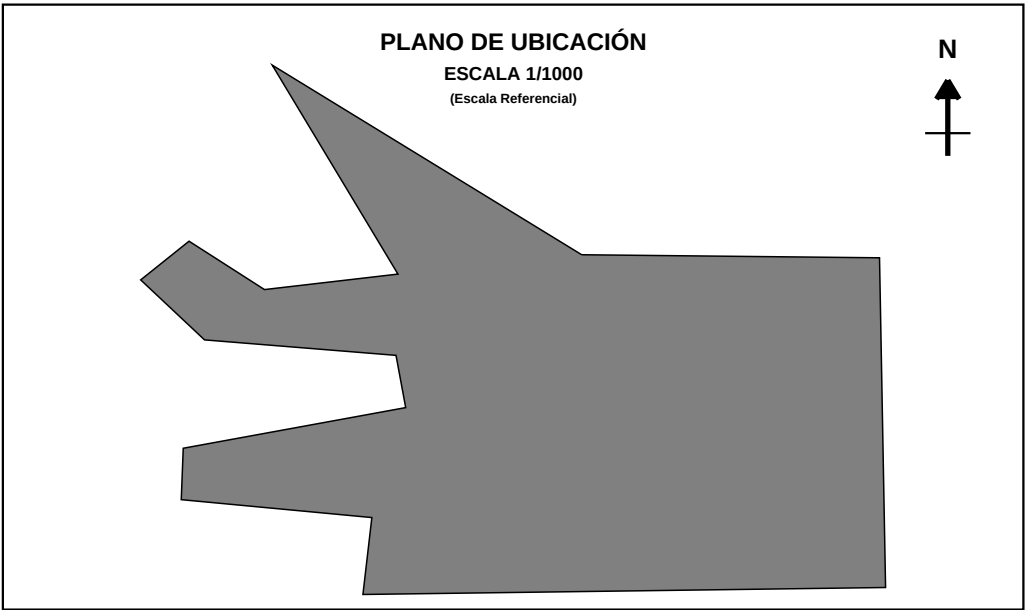

CUADRO DE DATOS TÉCNICOS - UTM WGS84					
VÉRTICE	LADO	DIST (m)	ÁNGULO INT.	ESTE (X)	NORTE (Y)
V-1	V1-V2	699.89	210°54'05"	284081.250	8670566.250
V-2	V2-V3	774.68	91°38'12"	284781.108	8670559.091
V-3	V3-V4	1228.31	89°42'46"	284795.313	8669784.545
V-4	V4-V5	181.90	82°36'40"	283567.116	8669768.182
V-5	V5-V6	449.87	271°15'46"	283588.104	8669948.864
V-6	V6-V7	120.89	93°08'26"	283140.199	8669990.909
V-7	V7-V8	531.37	102°34'15"	283144.886	8670111.705
V-8	V8-V9	124.81	270°08'34"	283667.614	8670207.159
V-9	V9-V10	451.47	254°53'19"	283644.886	8670329.886
V-10	V10-V11	205.80	141°24'35"	283194.886	8670366.250
V-11	V11-V12	145.53	81°52'12"	283044.886	8670507.159
V-12	V12-V13	210.57	108°40'45"	283158.523	8670598.068
V-13	V13-V14	315.74	219°16'28"	283335.795	8670484.432
V-14	V14-V15	572.96	294°25'42"	283649.432	8670520.795
V-15	V15-V1	852.85	27°28'15"	283353.977	8671011.705

PLANO PERIMÉTRICO		FIRMA Y SELLO PROFESIONAL:
PROPIETARIO / PROYECTO: Habilitación Urbana Los Cedros		
UBICACIÓN: Mina. C - Lote 14		
ÁREA TERRENO: 200.00 m ² 89°42'46"		
PERÍMETRO: 6866.63 ml		FECHA: 25/1/2026

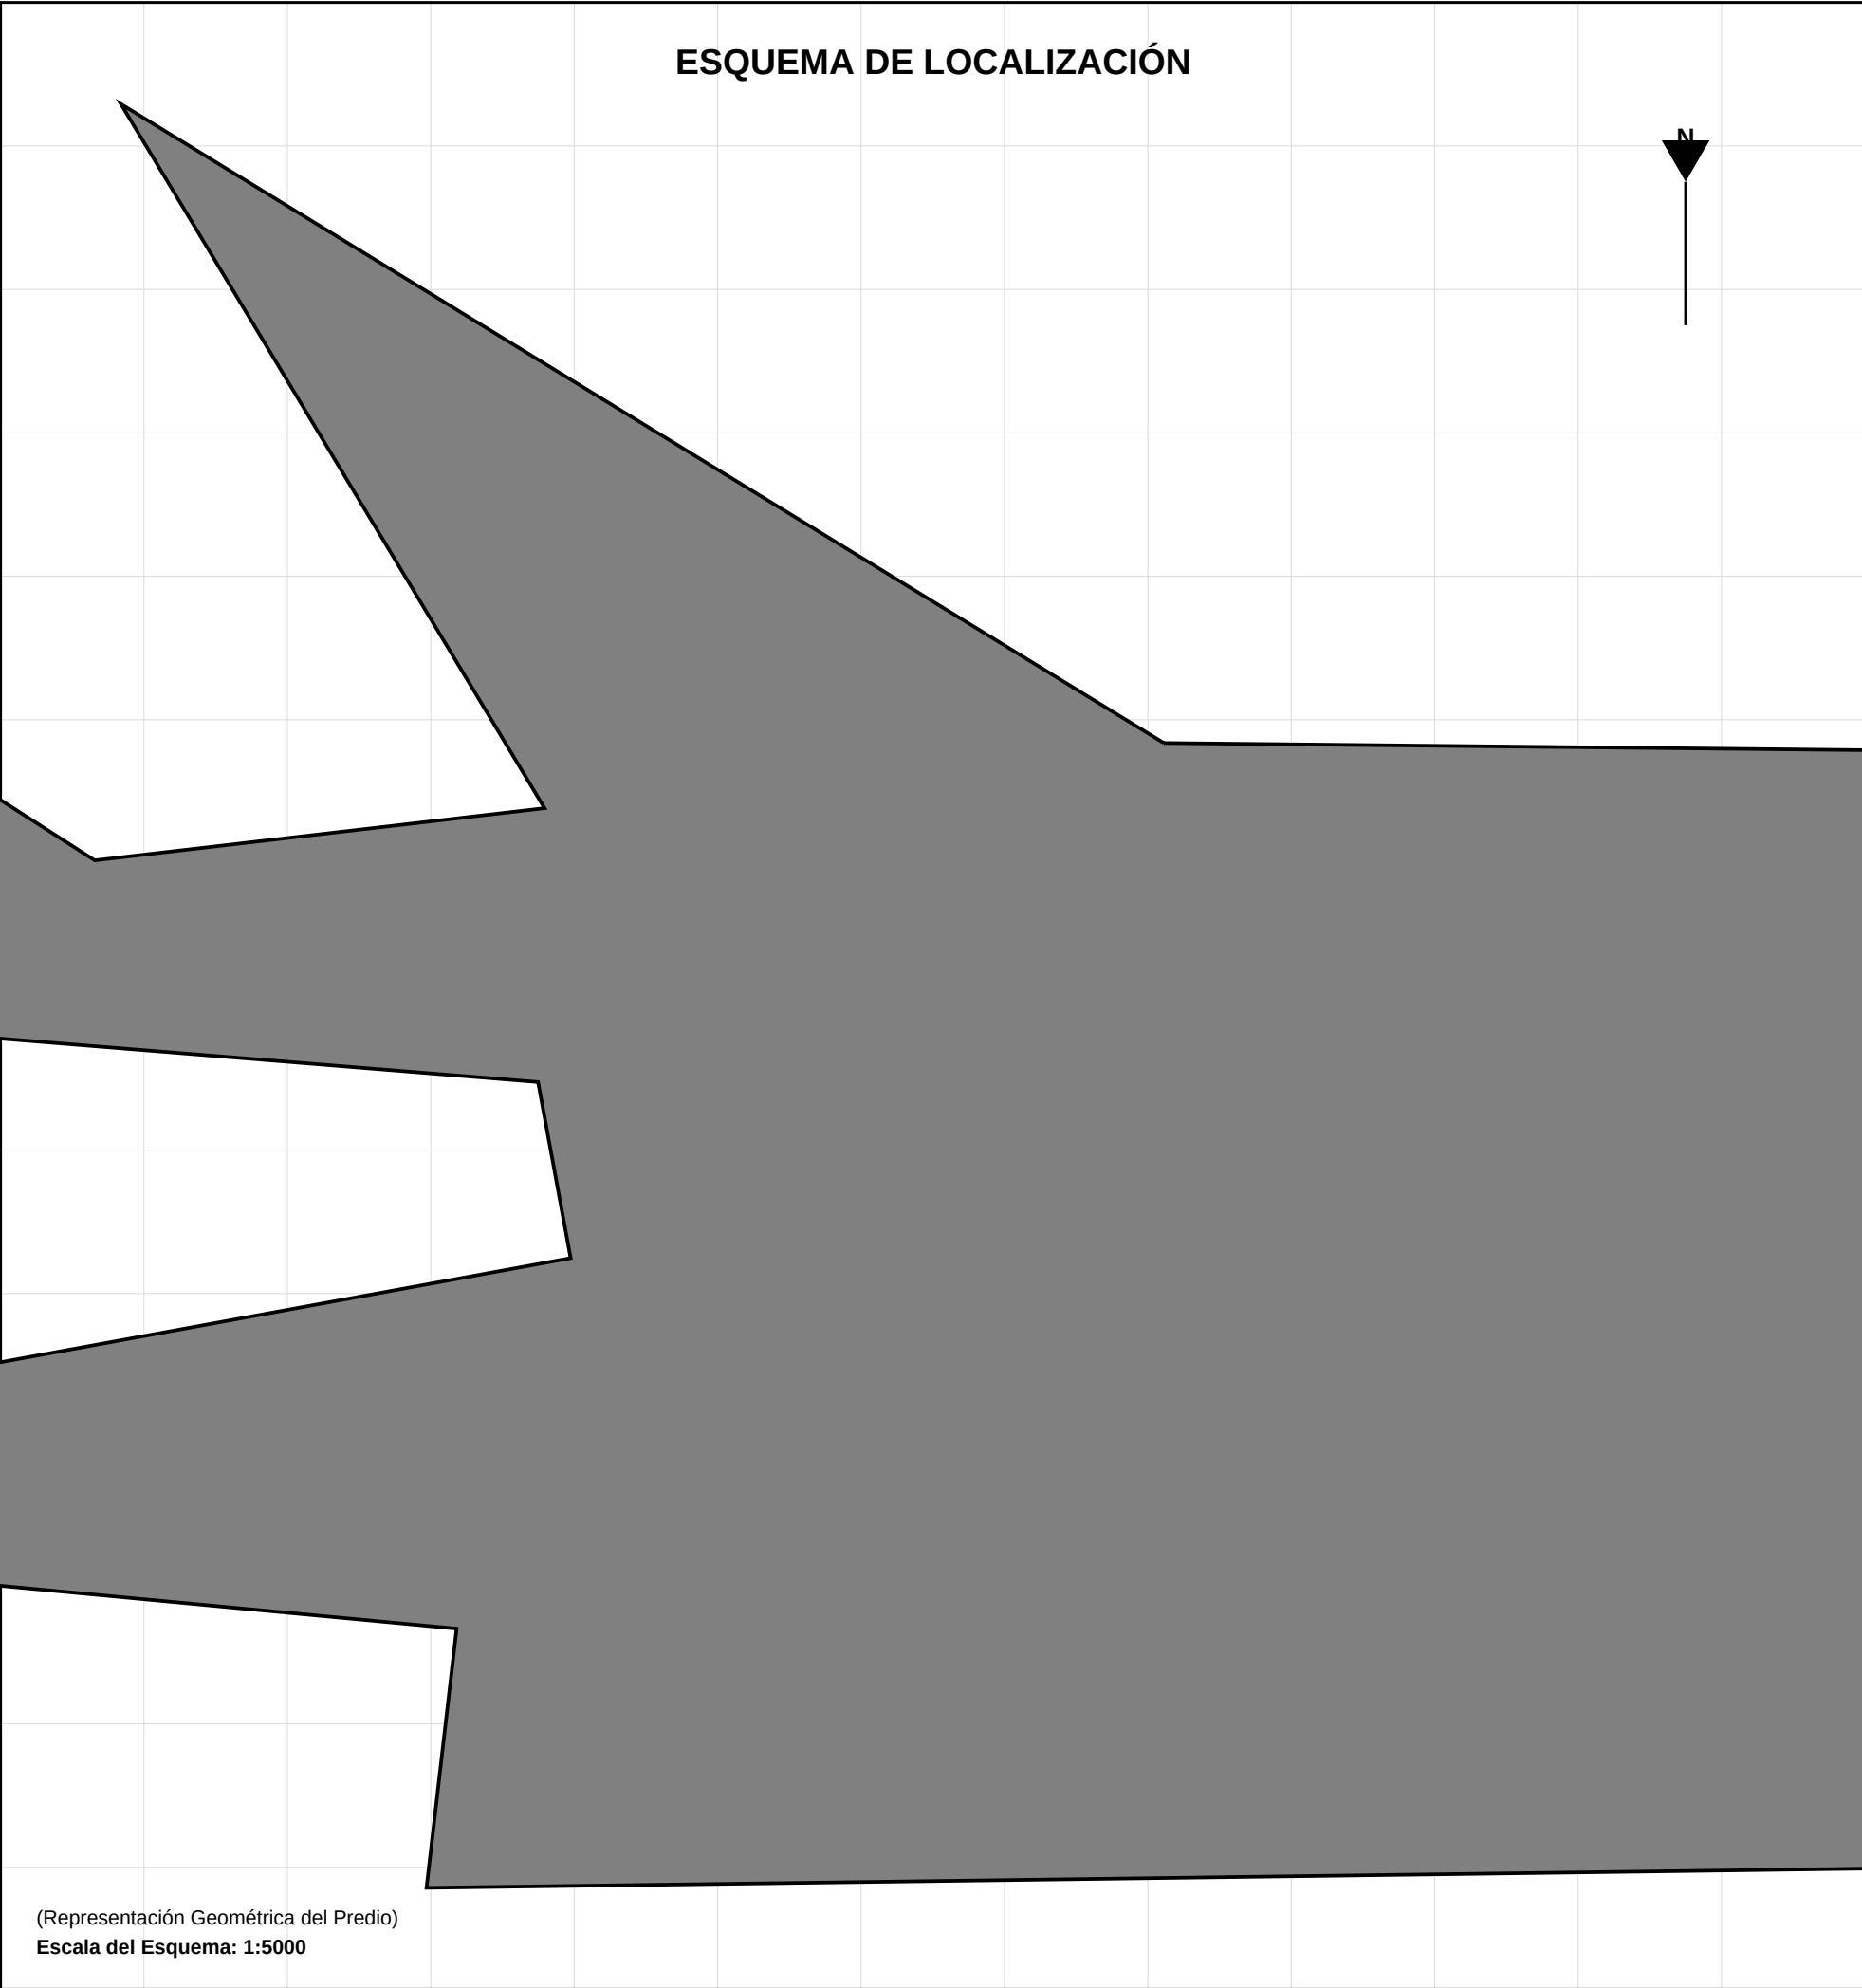

DATOS GENERALES Y NORMATIVOS		
Departamento:	Lima	
Provincia:	Lima	
Distrito:	Habilitación Urbana Los Cedros	
Urbanización/Sector:	Habilitación Urbana Los Cedros - MZ-C-Lote14	
Manzana:	C	
Lote:	14	
---	---	
Zonificación:	RDM (Residencial Densidad Media)*	
Usos Permisibles:	Unifamiliar / Multifamiliar*	
Área Terreno:	200.00 m²	
Perímetro:	6866.63 ml	
* Datos referenciales de zonificación. Verificar Certificado de Parámetros.		