

PLANOS PRO

Sistema Profesional de Generación de Planos

PROYECTO:

Habilitación Urbana Los Cedros

LOTE:

MZ-C-Lote14

DOCUMENTO: MEMORIA DESCRIPTIVA

FECHA: 25 de enero de 2026

MEMORIA DESCRIPTIVA

I. IDENTIFICACIÓN DEL PREDIO

Código Catastral:	MZ-C-Lote14
Nombre del Lote:	Habilitación Urbana Los Cedros - MZ-C-Lote14
Manzana:	C
Etapas:	Habilitación Urbana Los Cedros
Número de Lote:	14
Estado:	LIBRE

II. UBICACIÓN GEOGRÁFICA

Sistema de Coordenadas:	UTM WGS84 - Zona 18S
Datum:	WGS84
Hemisferio:	Sur

III. CARACTERÍSTICAS MÉTRICAS DEL PREDIO

ÁREA TOTAL:	200.00 m²
PERÍMETRO TOTAL:	3640.49 ml
Frente:	10.00 ml
Fondo:	10.00 ml
Lado Derecho:	20.00 ml
Lado Izquierdo:	20.00 ml

IV. LINDEROS Y COLINDANCIAS

El predio tiene los siguientes linderos y colindancias:

Por el NORTE: Con calle "Av. Los Alamos"

Por el SUR: Con lote "Lote 05"

Por el OESTE: Con lote "Lote 13"

Por el ESTE: Con lote "Lote 15"

V. CUADRO DE DATOS TÉCNICOS - COORDENADAS UTM

VÉRTICE	LADO	ESTE (m)	NORTE (m)
V1	V1-V2	283779.77	8670613.05
V2	V2-V3	284165.63	8670636.76
V3	V3-V4	284190.34	8670223.52
V4	V4-V5	283637.36	8670221.79
V5	V5-V6	283636.22	8670297.93
V6	V6-V7	283292.50	8670285.77
V7	V7-V8	283268.86	8670363.95
V8	V8-V9	283567.05	8670431.23
V9	V9-V10	283537.95	8670518.50
V10	V10-V11	283356.14	8670489.41
V11	V11-V12	283216.14	8670571.23
V12	V12-V13	283279.77	8670627.59
V13	V13-V14	283405.23	8670589.41
V14	V14-V15	283521.59	8670613.05
V15	V15-V1	283405.23	8670849.41


PROPIETARIO

Firma y Sello

PROFESIONAL RESPONSABLE


Ing. Civil / Arquitecto

PLANO PERIMÉTRICO

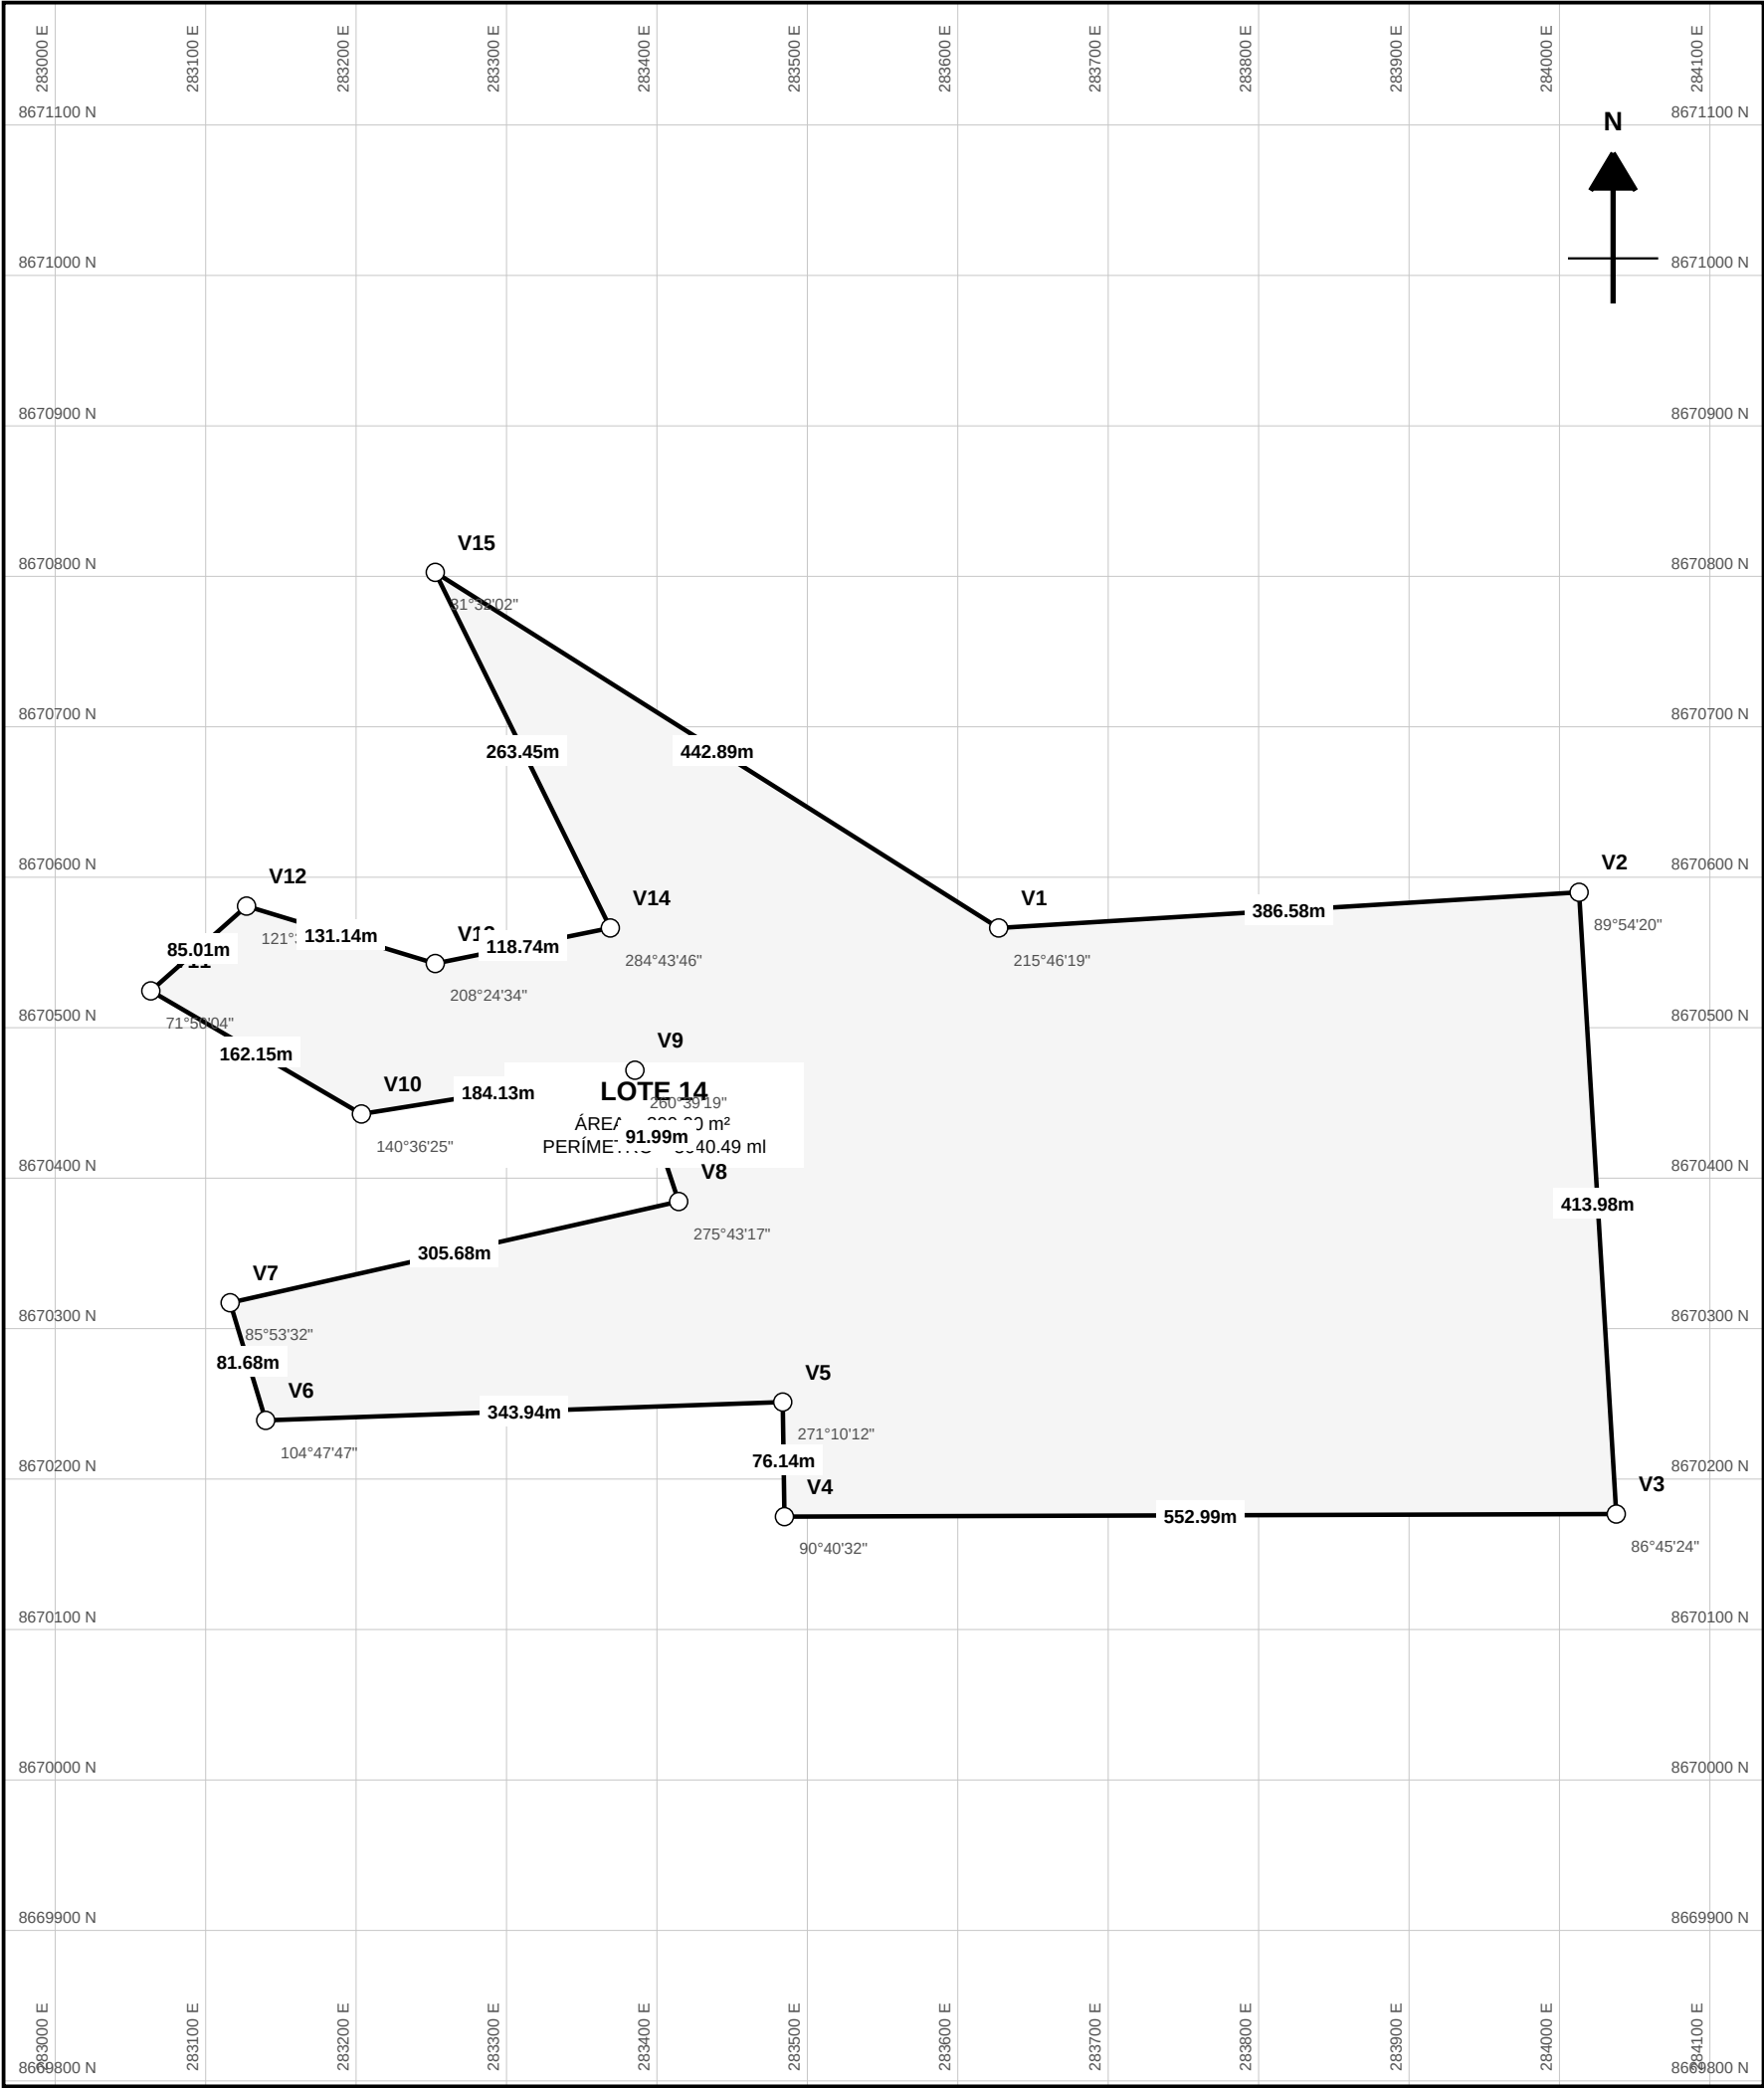

PLANO DE UBICACIÓN

ESCALA 1/1000
(Escala Ajustada: 1/20000)

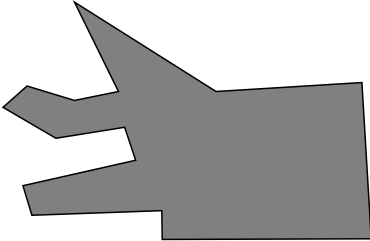

CUADRO DE DATOS TÉCNICOS - UTM WGS84

VÉRTICE	LADO	DIST (m)	ÁNGULO INT.	ESTE (X)	NORTE (Y)
V-1	V1-V2	386.58	215°46'19"	283779.773	8670613.045
V-2	V2-V3	413.98	89°54'20"	284165.625	8670636.761
V-3	V3-V4	552.99	86°45'24"	284190.341	8670223.523
V-4	V4-V5	76.14	90°40'32"	283637.358	8670221.790
V-5	V5-V6	343.94	271°10'12"	283636.222	8670297.926
V-6	V6-V7	81.68	104°47'47"	283292.500	8670285.773
V-7	V7-V8	305.68	85°53'32"	283268.864	8670363.955
V-8	V8-V9	91.99	275°43'17"	283567.045	8670431.227
V-9	V9-V10	184.13	260°39'19"	283537.955	8670518.500
V-10	V10-V11	162.15	140°36'25"	283356.136	8670489.409
V-11	V11-V12	85.01	71°50'04"	283216.136	8670571.227
V-12	V12-V13	131.14	121°32'27"	283279.773	8670627.591
V-13	V13-V14	118.74	208°24'34"	283405.227	8670589.409
V-14	V14-V15	263.45	284°43'46"	283521.591	8670613.045
V-15	V15-V1	442.89	31°32'02"	283405.227	8670849.409

PLANO
PERIMÉTRICO

PROPIETARIO / PROYECTO:

Habilitación Urbana Los Cedros

UBICACIÓN:

Mina. C - Lote 14

ÁREA TERRENO:

200.00 m²


PERIMETRO:

3640.49 ml

ESCALA: 1/5000

FIRMA Y SELLO PROFESIONAL:

FECHA: 25/1/2026

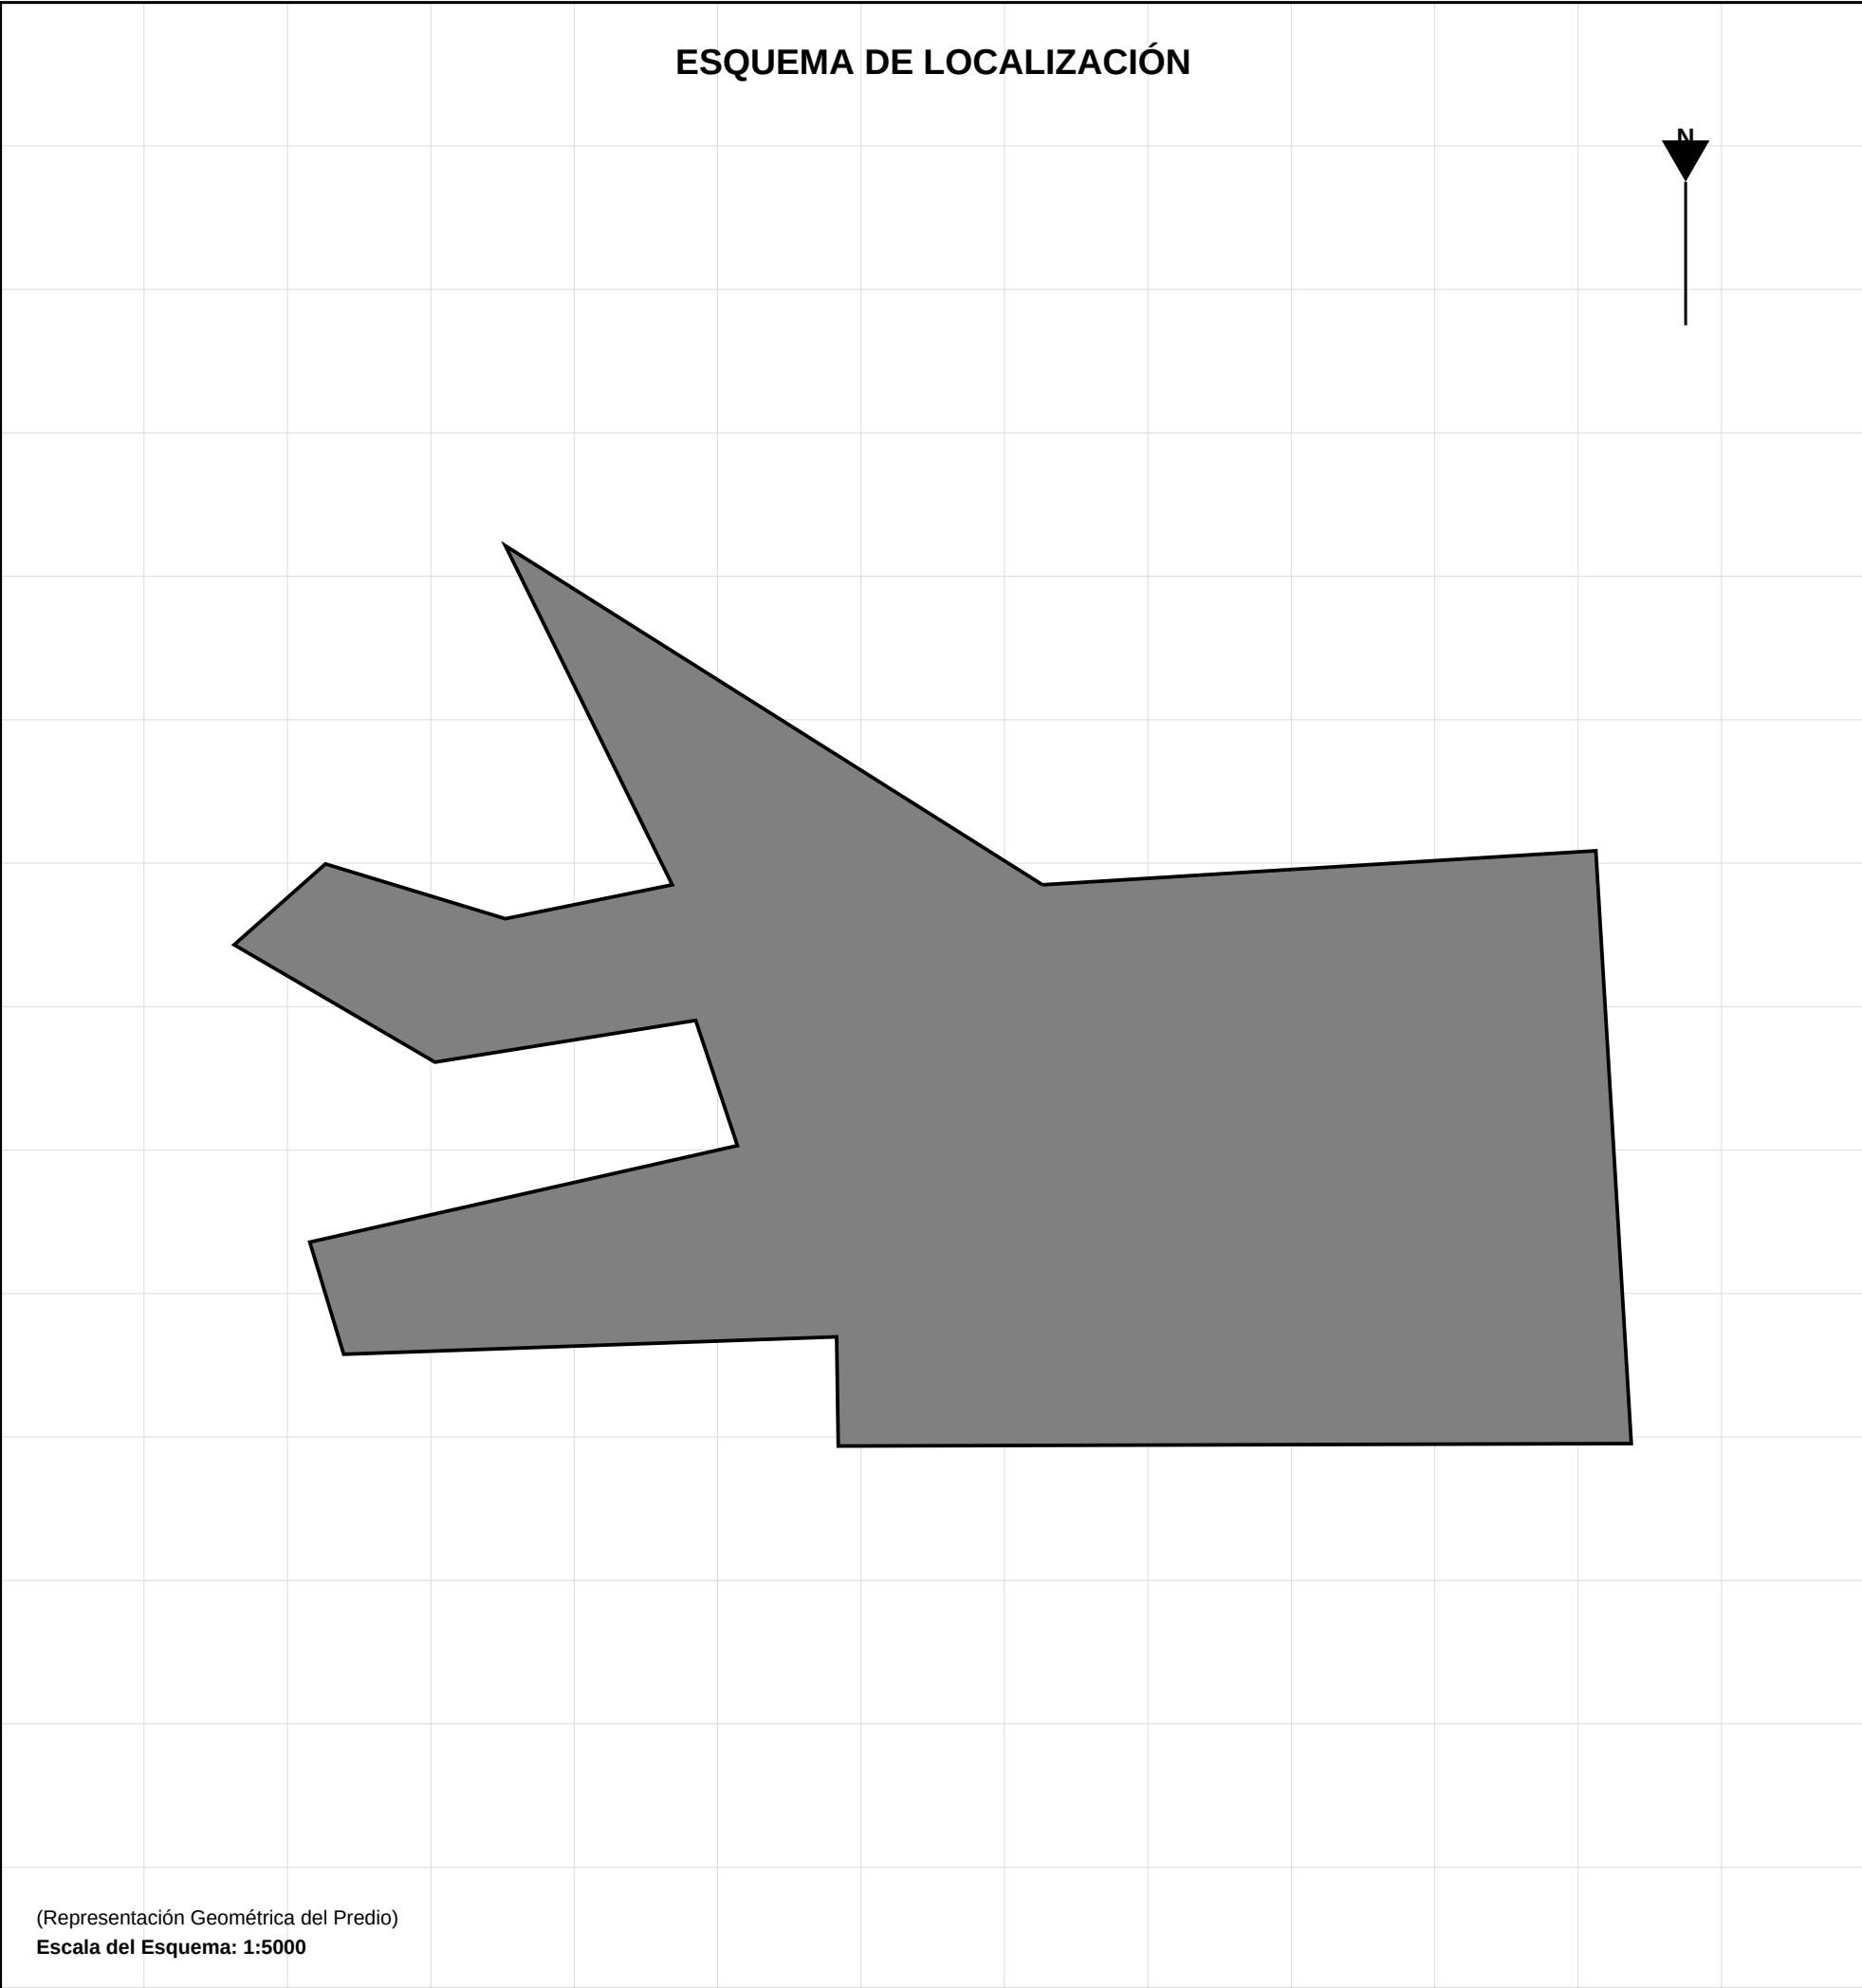

DATOS GENERALES Y NORMATIVOS	
Departamento:	Lima
Provincia:	Lima
Distrito:	Habilitación Urbana Los Cedros
Urbanización/Sector:	Habilitación Urbana Los Cedros - MZ-C-Lote14
Manzana:	C
Lote:	14
---	---
Zonificación:	RDM (Residencial Densidad Media)*
Usos Permisibles:	Unifamiliar / Multifamiliar*
Área Terreno:	200.00 m²
Perímetro:	3640.49 ml
* Datos referenciales de zonificación. Verificar Certificado de Parámetros.	

COORDENADAS DE LOCALIZACIÓN (CENTROIDE)	
SISTEMA DE REFERENCIA:	WGS-84 / ZONA 18S
COORDENADAS UTM:	
ESTE (X): 283550.652 m	NORTE (Y): 8670488.839 m
COORDENADAS GEOGRÁFICAS:	
LATITUD: -76.9881217°	LONGITUD: -12.0196717°

PLANO DE UBICACIÓN		FIRMA Y SELLO:
PROPIETARIO:	---	
UBICACIÓN:	Habilitación Urbana Los Cedros - Mz. C Lt. 14	
LÁMINA:	U-01	
FECHA: 25/1/2026	DIBUJO: AUTOMÁTICO	ESCALA: INDICADA