

PLANOS PRO

Sistema Profesional de Generación de Planos

PROYECTO:

Habilitación Urbana Los Cedros

LOTE:

MZ-C-Lote14

DOCUMENTO: MEMORIA DESCRIPTIVA

FECHA: 25 de enero de 2026

MEMORIA DESCRIPTIVA

I. IDENTIFICACIÓN DEL PREDIO

Código Catastral:	MZ-C-Lote14
Nombre del Lote:	Habilitación Urbana Los Cedros - MZ-C-Lote14
Manzana:	C
Etapas:	Habilitación Urbana Los Cedros
Número de Lote:	14
Estado:	LIBRE

II. UBICACIÓN GEOGRÁFICA

Sistema de Coordenadas:	UTM WGS84 - Zona 18S
Datum:	WGS84
Hemisferio:	Sur

III. CARACTERÍSTICAS MÉTRICAS DEL PREDIO

ÁREA TOTAL:	200.00 m²
PERÍMETRO TOTAL:	5763.78 ml
Frente:	10.00 ml
Fondo:	10.00 ml
Lado Derecho:	20.00 ml
Lado Izquierdo:	20.00 ml

IV. LINDEROS Y COLINDANCIAS

El predio tiene los siguientes linderos y colindancias:

Por el NORTE: Con calle "Av. Los Alamos"

Por el SUR: Con lote "Lote 05"

Por el OESTE: Con lote "Lote 13"

Por el ESTE: Con lote "Lote 15"

V. CUADRO DE DATOS TÉCNICOS - COORDENADAS UTM

VÉRTICE	LADO	ESTE (m)	NORTE (m)
V1	V1-V2	284044.89	8670491.70
V2	V2-V3	284453.98	8670537.16
V3	V3-V4	284490.16	8670071.12
V4	V4-V5	283822.16	8670032.61
V5	V5-V6	283799.43	8670209.89
V6	V6-V7	283108.52	8670150.80
V7	V7-V8	283063.07	8670291.70
V8	V8-V9	283531.25	8670355.34
V9	V9-V10	283508.52	8670478.07
V10	V10-V11	283235.80	8670423.52
V11	V11-V12	282944.89	8670532.61
V12	V12-V13	283022.16	8670650.80
V13	V13-V14	283272.16	8670528.07
V14	V14-V15	283526.70	8670559.89
V15	V15-V1	283235.80	8670882.61

PROPIETARIO

Firma y Sello

PROFESIONAL RESPONSABLE


Ing. Civil / Arquitecto

PLANO PERIMÉTRICO



PLANO DE UBICACIÓN

ESCALA 1/1000
(Escala Ajustada: 1/20000)

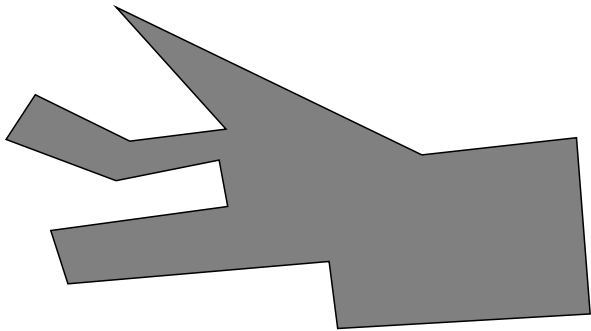

CUADRO DE DATOS TÉCNICOS - UTM WGS84

VÉRTICE	LADO	DIST (m)	ÁNGULO INT.	ESTE (X)	NORTE (Y)
V-1	V1-V2	411.61	212°07'39"	284044.886	8670491.705
V-2	V2-V3	467.44	88°05'57"	284453.977	8670537.159
V-3	V3-V4	669.11	88°51'36"	284490.159	8670071.123
V-4	V4-V5	178.72	94°00'23"	283822.159	8670032.614
V-5	V5-V6	693.43	267°34'58"	283799.432	8670209.886
V-6	V6-V7	148.06	102°59'25"	283108.523	8670150.795
V-7	V7-V8	472.49	79°51'42"	283063.068	8670291.705
V-8	V8-V9	124.81	272°45'04"	283531.250	8670355.341
V-9	V9-V10	278.13	270°49'06"	283508.523	8670478.068
V-10	V10-V11	310.69	148°08'02"	283235.795	8670423.523
V-11	V11-V12	141.20	77°22'39"	282944.886	8670532.614
V-12	V12-V13	278.50	97°01'54"	283022.159	8670650.795
V-13	V13-V14	256.53	213°16'19"	283272.159	8670528.068
V-14	V14-V15	434.49	304°54'24"	283526.705	8670559.886
V-15	V15-V1	898.58	22°10'51"	283235.795	8670882.614

PLANO
PERIMÉTRICO

PROPIETARIO / PROYECTO:
Habilitación Urbana Los Cedros


UBICACIÓN:
Mina. C - Lote 14

ÁREA TERRENO: 200.00 m²

PERIMETRO: 5763.78 ml
ESCALA: 1/7500

FIRMA Y SELLO PROFESIONAL:

FECHA: 25/1/2026

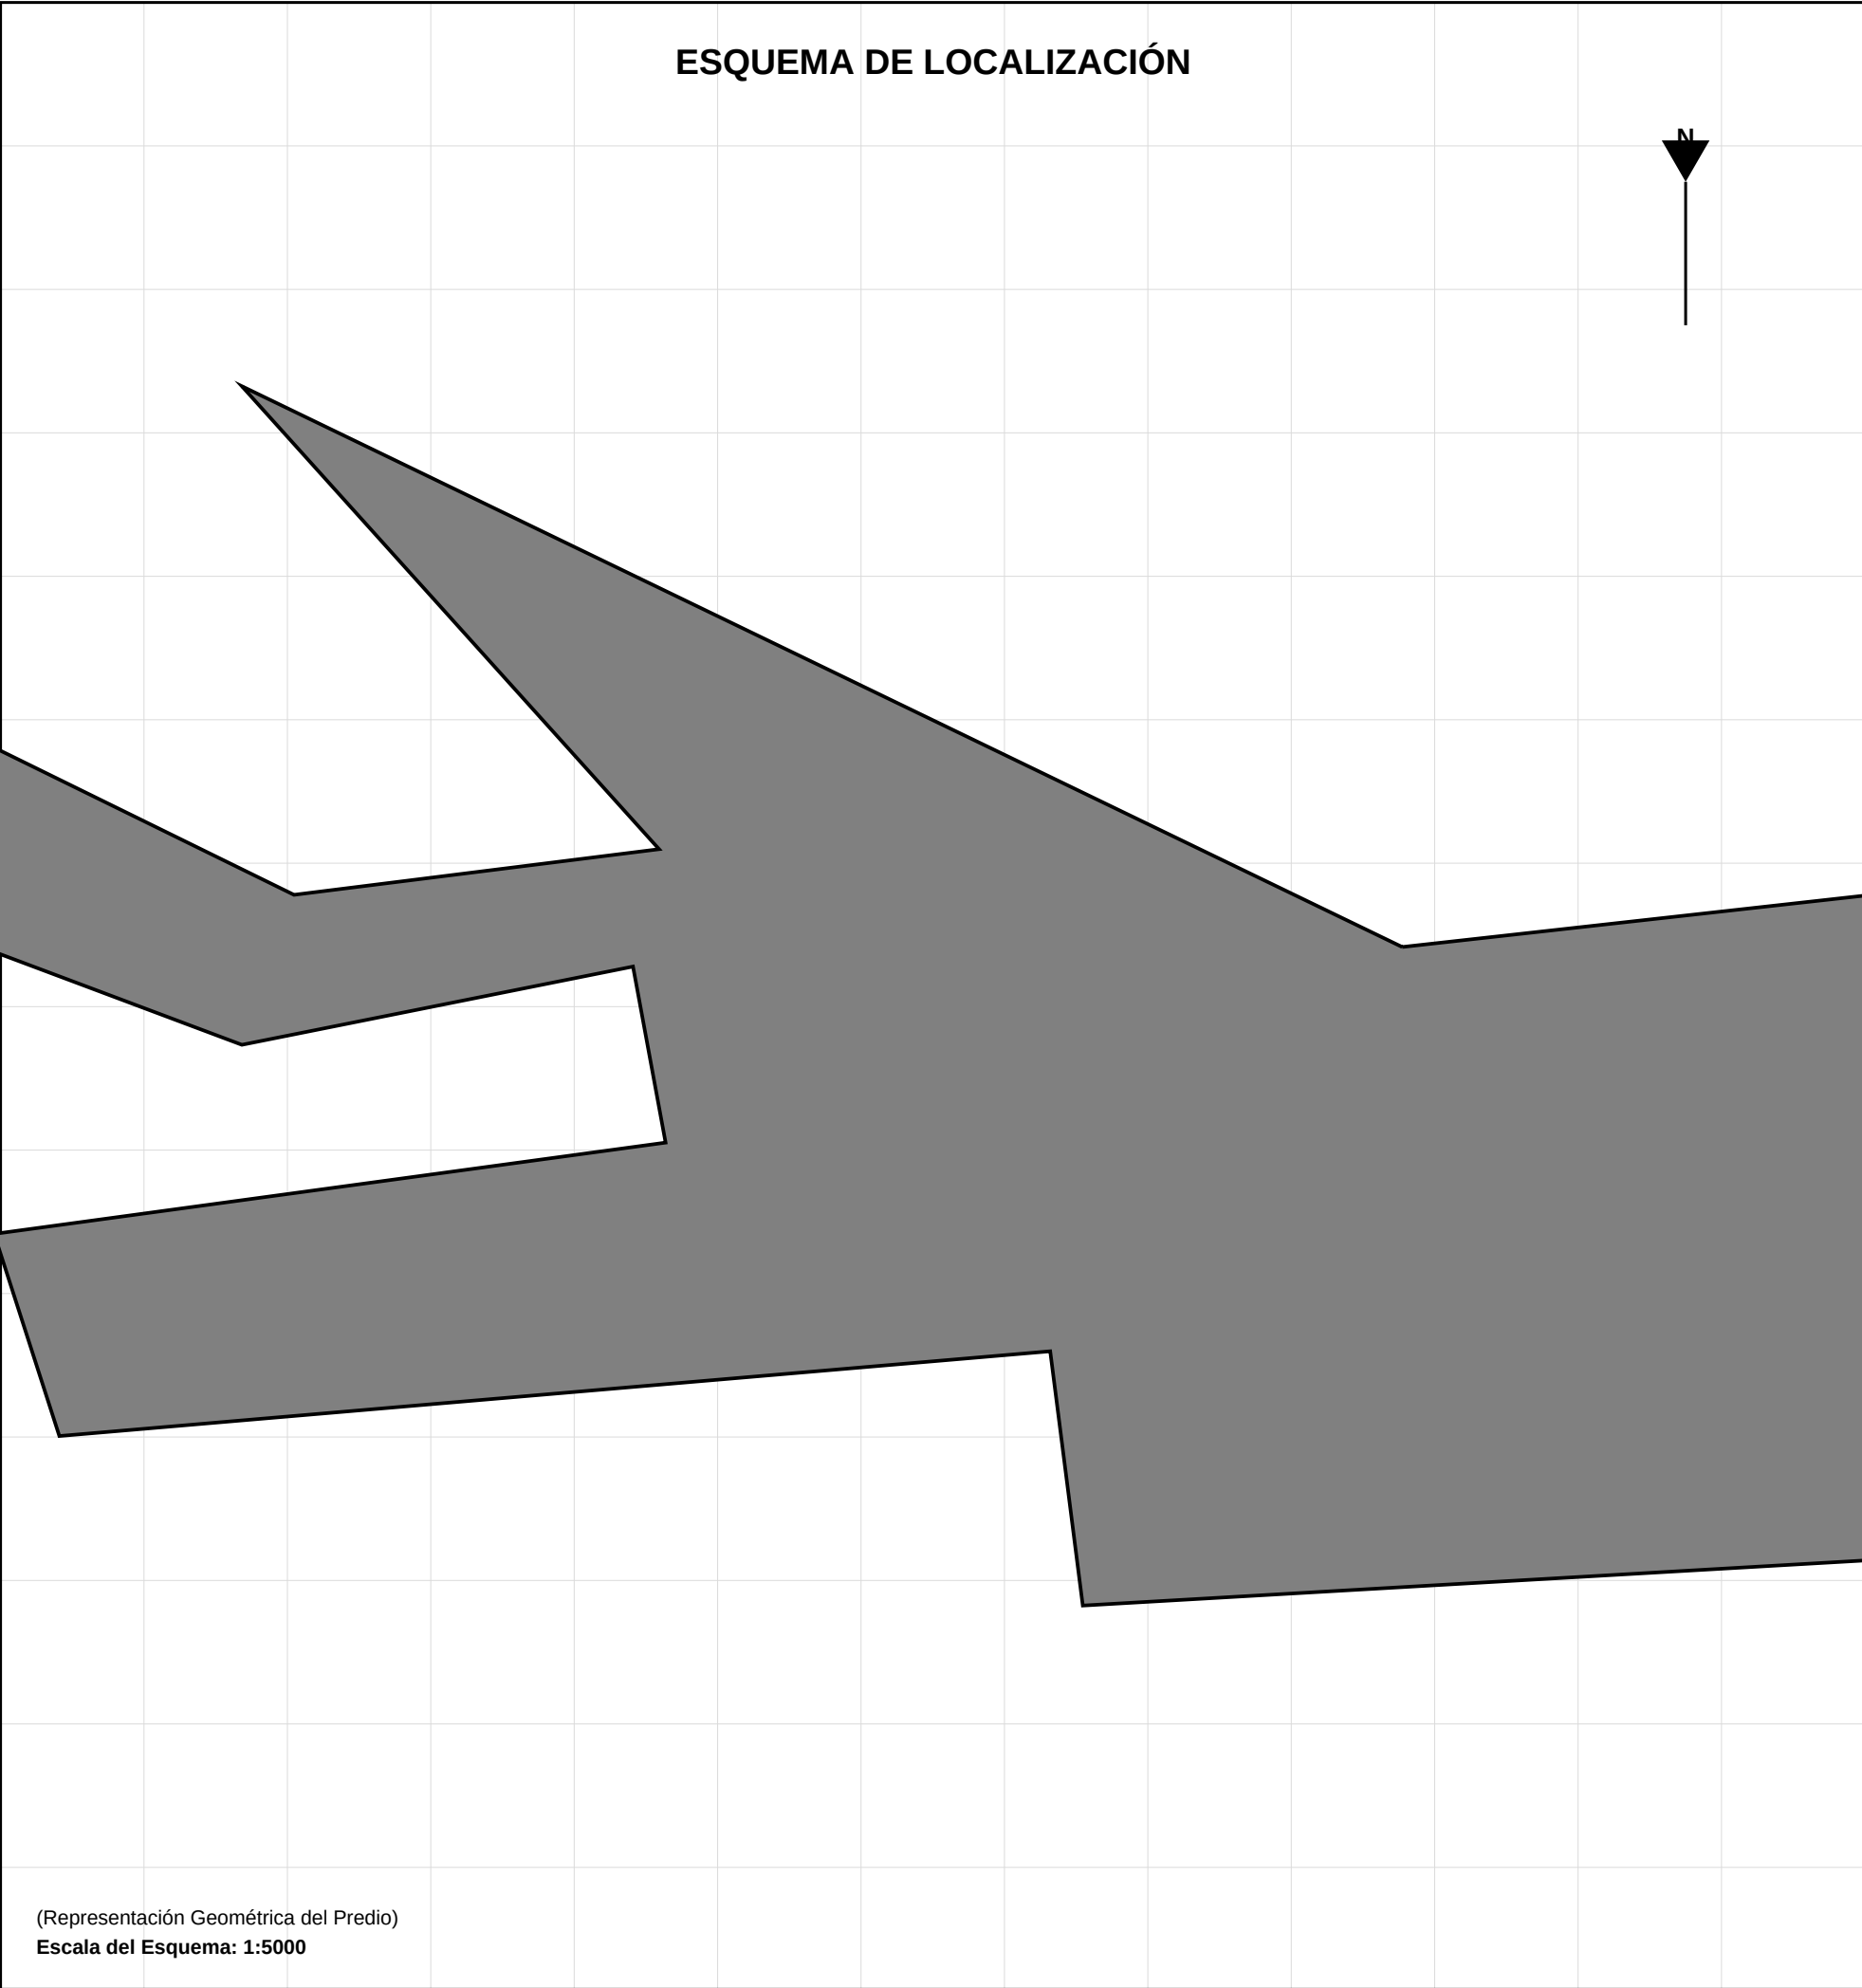

DATOS GENERALES Y NORMATIVOS	
Departamento:	Lima
Provincia:	Lima
Distrito:	Habilitación Urbana Los Cedros
Urbanización/Sector:	Habilitación Urbana Los Cedros - MZ-C-Lote14
Manzana:	C
Lote:	14
---	---
Zonificación:	RDM (Residencial Densidad Media)*
Usos Permisibles:	Unifamiliar / Multifamiliar*
Área Terreno:	200.00 m²
Perímetro:	5763.78 ml
* Datos referenciales de zonificación. Verificar Certificado de Parámetros.	

COORDENADAS DE LOCALIZACIÓN (CENTROIDE)	
SISTEMA DE REFERENCIA:	WGS-84 / ZONA 18S
COORDENADAS UTM:	
ESTE (X): 283537.298 m	NORTE (Y): 8670413.060 m
COORDENADAS GEOGRÁFICAS:	
LATITUD: -76.9882493°	LONGITUD: -12.0203557°

PLANO DE UBICACIÓN		FIRMA Y SELLO:
PROPIETARIO:	---	
UBICACIÓN:	Habilitación Urbana Los Cedros - Mz. C Lt. 14	
LÁMINA:	U-01	
FECHA: 25/1/2026	DIBUJO: AUTOMÁTICO	
		ESCALA: INDICADA