

PLANOS PRO

Sistema Profesional de Generación de Planos

PROYECTO:

Habilitación Urbana Los Cedros

LOTE:

MZ-C-Lote14

DOCUMENTO: MEMORIA DESCRIPTIVA

FECHA: 25 de enero de 2026

MEMORIA DESCRIPTIVA

I. IDENTIFICACIÓN DEL PREDIO

Código Catastral:	MZ-C-Lote14
Nombre del Lote:	Habilitación Urbana Los Cedros - MZ-C-Lote14
Manzana:	C
Etapas:	Habilitación Urbana Los Cedros
Número de Lote:	14
Estado:	LIBRE

II. UBICACIÓN GEOGRÁFICA

Sistema de Coordenadas:	UTM WGS84 - Zona 18S
Datum:	WGS84
Hemisferio:	Sur

III. CARACTERÍSTICAS MÉTRICAS DEL PREDIO

ÁREA TOTAL:	200.00 m ²
PERÍMETRO TOTAL:	2809.67 ml
Frente:	10.00 ml
Fondo:	10.00 ml
Lado Derecho:	20.00 ml
Lado Izquierdo:	20.00 ml

IV. LINDEROS Y COLINDANCIAS

El predio tiene los siguientes linderos y colindancias:

Por el NORTE: Con calle "Av. Los Alamos"

Por el SUR: Con lote "Lote 05"

Por el OESTE: Con lote "Lote 13"

Por el ESTE: Con lote "Lote 15"

V. CUADRO DE DATOS TÉCNICOS - COORDENADAS UTM

VÉRTICE	LADO	ESTE (m)	NORTE (m)
V1	V1-V2	284281.59	8670374.86
V2	V2-V3	284552.10	8670416.60
V3	V3-V4	284564.38	8670043.87
V4	V4-V5	284077.13	8670037.70
V5	V5-V6	284074.32	8670114.86
V6	V6-V7	283832.50	8670107.59
V7	V7-V8	283825.23	8670187.59
V8	V8-V9	284036.14	8670205.77
V9	V9-V10	284025.23	8670258.50
V10	V10-V11	283901.59	8670251.23
V11	V11-V12	283810.68	8670294.86
V12	V12-V13	283841.59	8670336.68
V13	V13-V14	283941.59	8670296.68
V14	V14-V15	284008.86	8670309.41
V15	V15-V1	283945.23	8670498.50


PROPIETARIO

Firma y Sello

PROFESIONAL RESPONSABLE


Ing. Civil / Arquitecto

PLANO PERIMÉTRICO

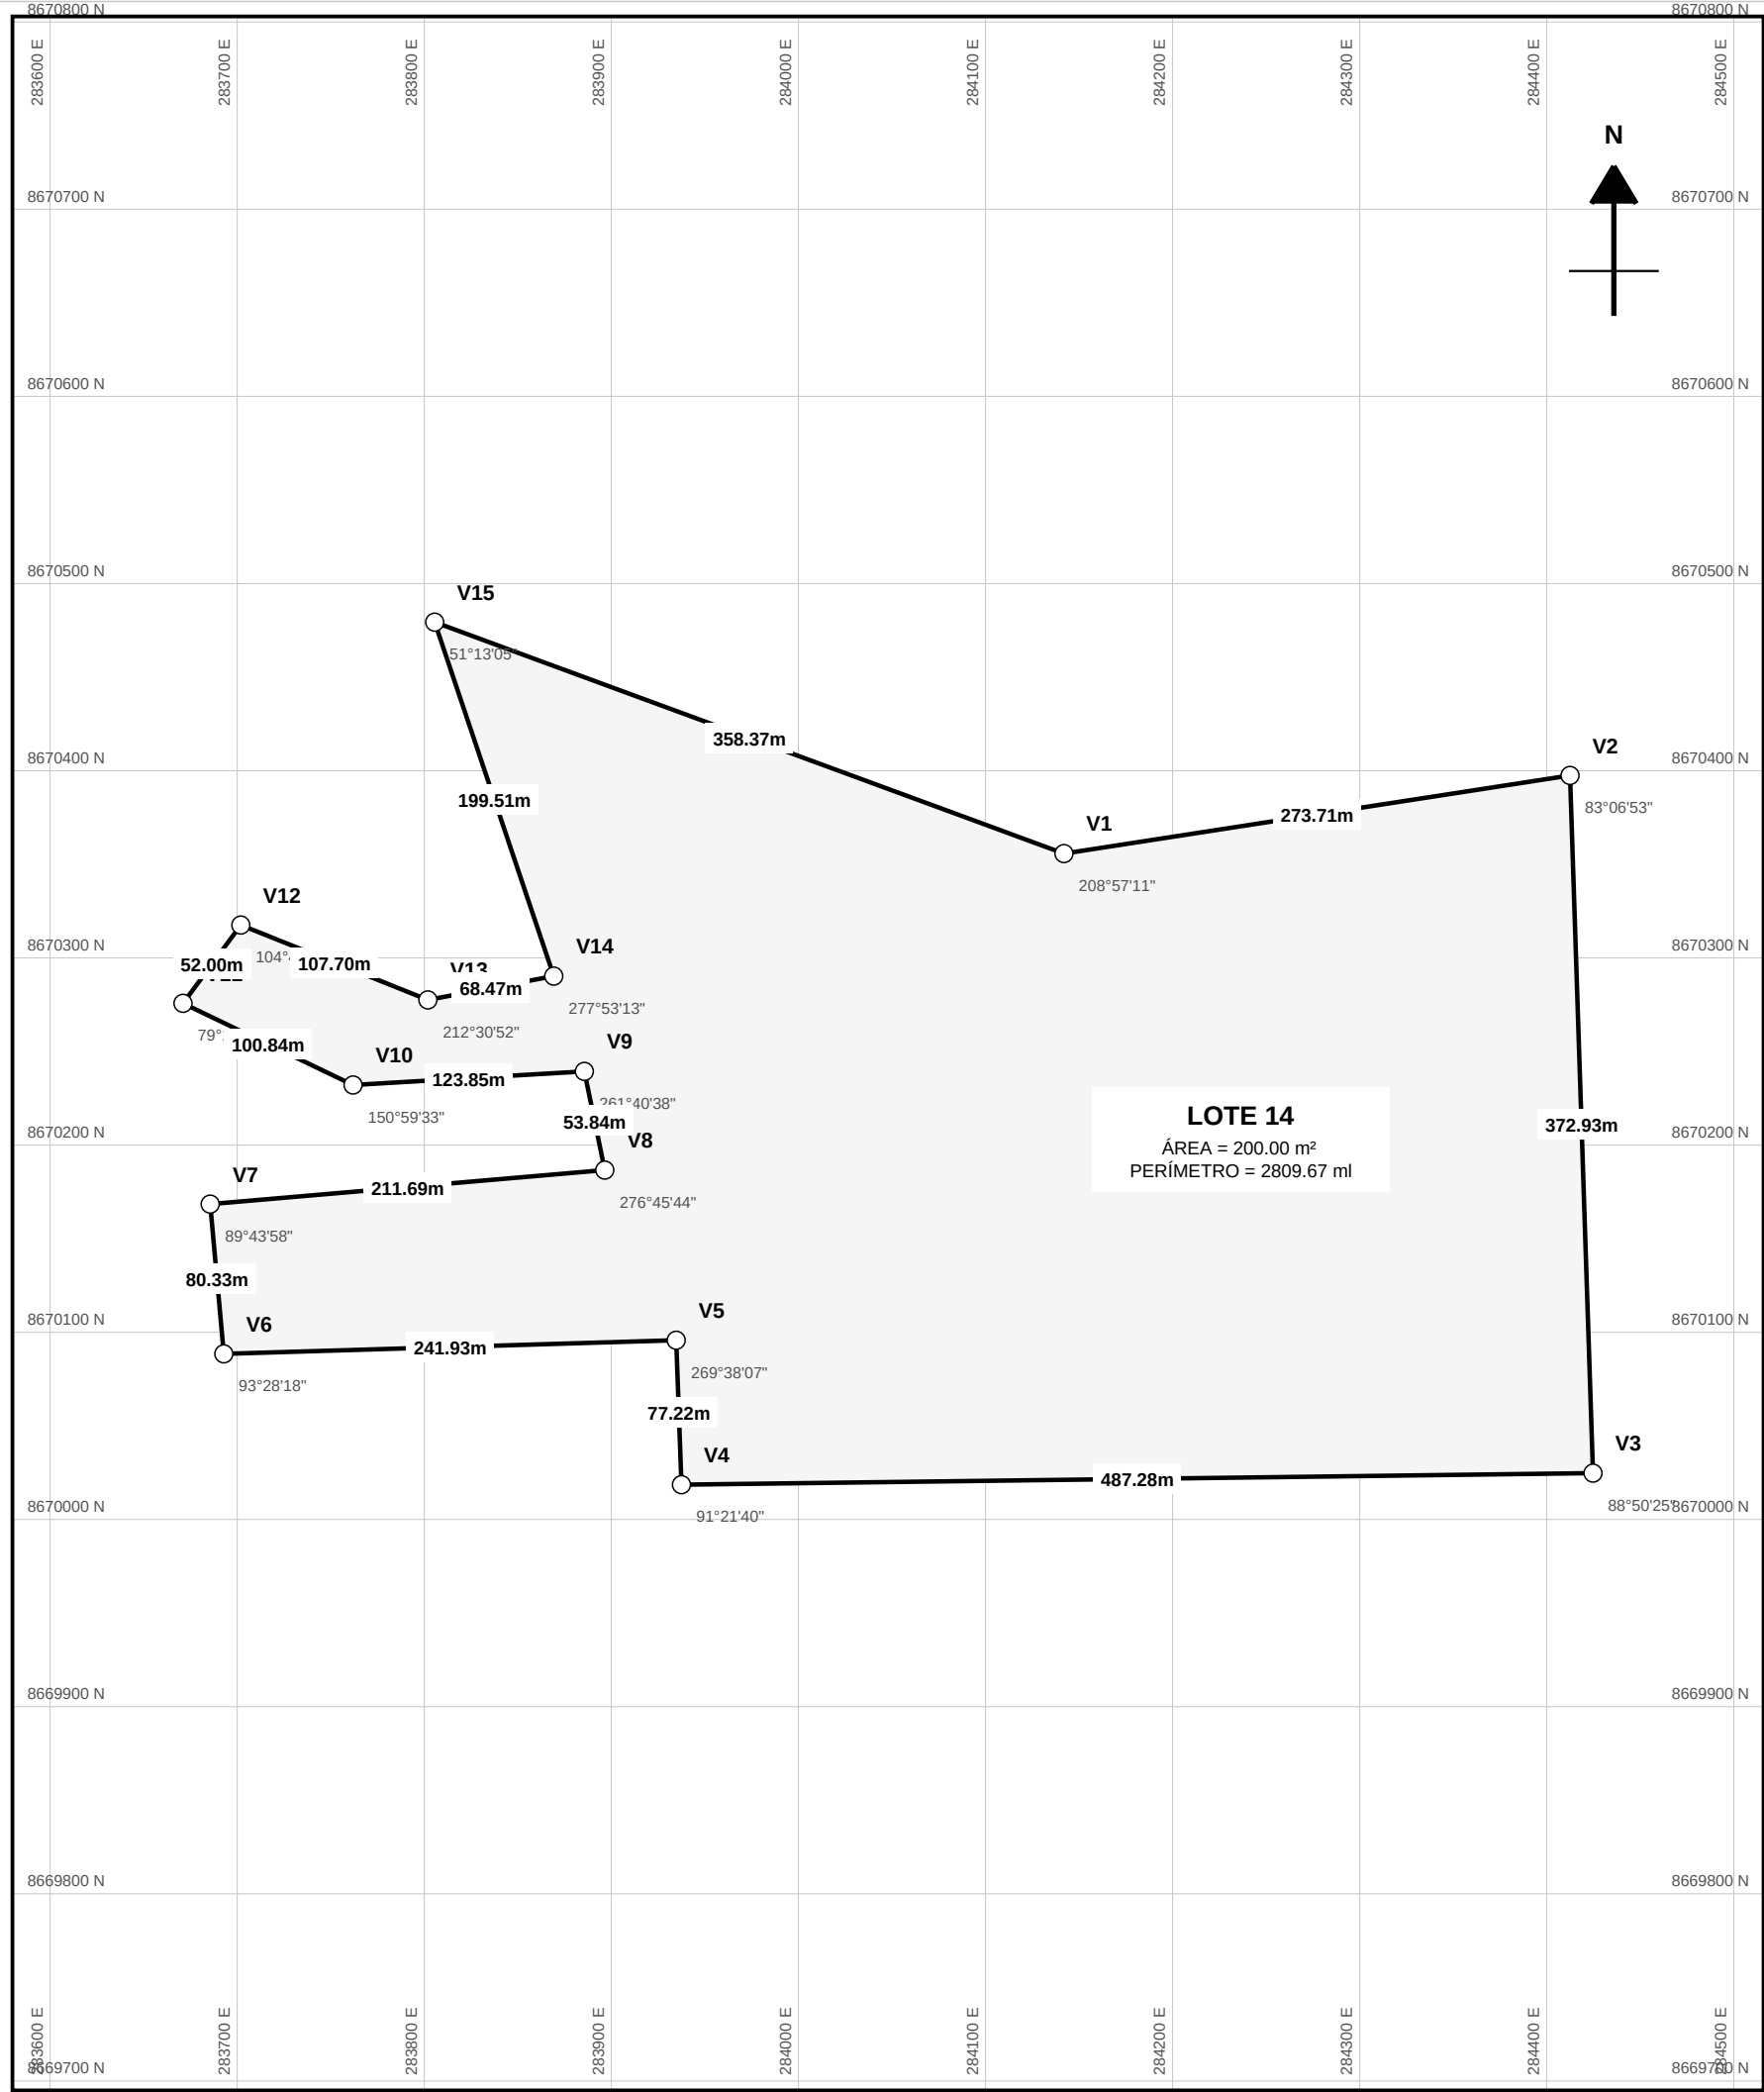

PLANO DE UBICACIÓN

ESCALA 1/1000
(Escala Ajustada: 1/10000)

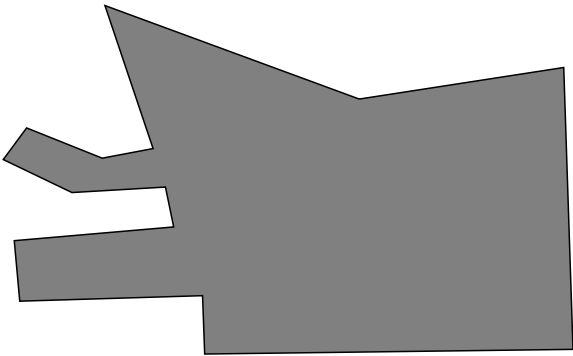

CUADRO DE DATOS TÉCNICOS - UTM WGS84

VÉRTICE	LADO	DIST (m)	ÁNGULO INT.	ESTE (X)	NORTE (Y)
V-1	V1-V2	273.71	208°57'11"	284281.591	8670374.864
V-2	V2-V3	372.93	83°06'53"	284552.102	8670416.602
V-3	V3-V4	487.28	88°50'25"	284564.375	8670043.875
V-4	V4-V5	77.22	91°21'40"	284077.131	8670037.699
V-5	V5-V6	241.93	269°38'07"	284074.318	8670114.864
V-6	V6-V7	80.33	93°28'18"	283832.500	8670107.591
V-7	V7-V8	211.69	89°43'58"	283825.227	8670187.591
V-8	V8-V9	53.84	276°45'44"	284036.136	8670205.773
V-9	V9-V10	123.85	261°40'38"	284025.227	8670258.500
V-10	V10-V11	100.84	150°59'33"	283901.591	8670251.227
V-11	V11-V12	52.00	79°10'18"	283810.682	8670294.864
V-12	V12-V13	107.70	104°40'04"	283841.591	8670336.682
V-13	V13-V14	68.47	212°30'52"	283941.591	8670296.682
V-14	V14-V15	199.51	277°53'13"	284008.864	8670309.409
V-15	V15-V1	358.37	51°13'05"	283945.227	8670498.500

PLANO
PERIMÉTRICO

PROPIETARIO / PROYECTO:

Habitación Urbana Los Cedros

UBICACIÓN:

Mina. C - Lote 14

ÁREA TERRENO:

200.00 m²

PERÍMETRO:


2809.67 ml

ESCALA: 1/4000

FIRMA Y SELLO PROFESIONAL:

FECHA: 25/1/2026

ESQUEMA DE LOCALIZACIÓN

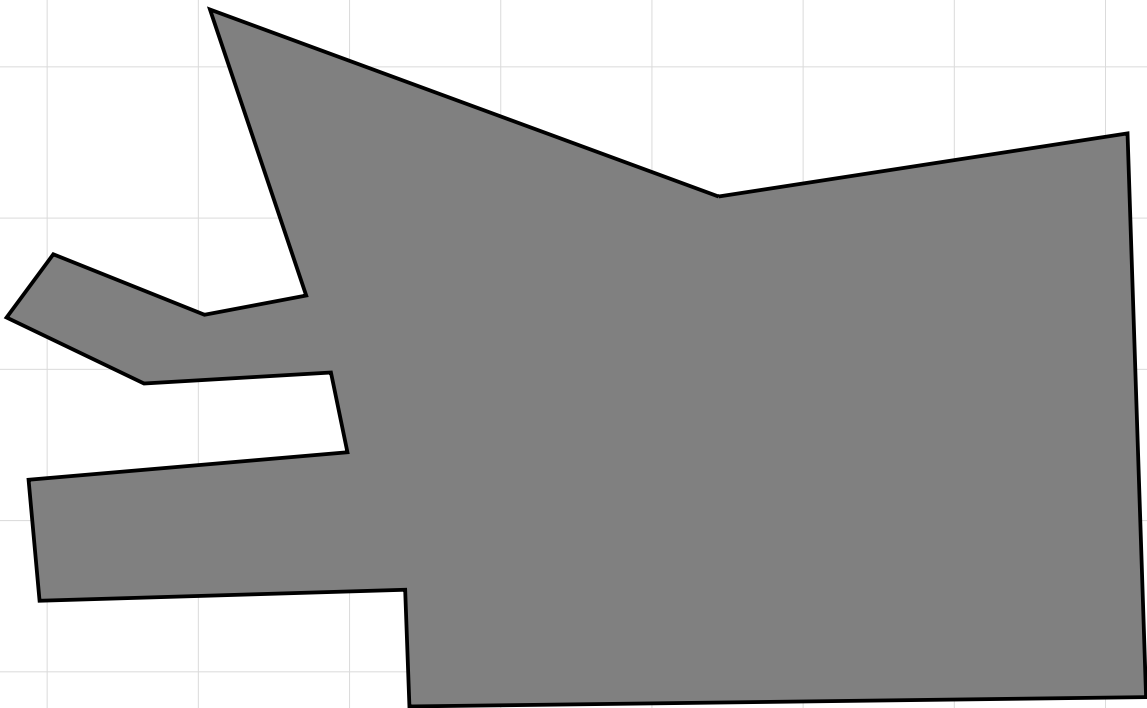

(Representación Geométrica del Predio)
Escala del Esquema: 1/5000

DATOS GENERALES Y NORMATIVOS

Departamento:	Lima
Provincia:	Lima
Distrito:	Habilitación Urbana Los Cedros
Urb./Sector:	Habilitación Urbana Los Cedros - MZ-C-Lote14
Manzana:	C
Lote:	14
---	---
Zonificación:	RDM
Área Terreno:	200.00 m²
Perímetro:	2809.67 ml

COORDENADAS DE LOCALIZACIÓN

SISTEMA: WGS-84 / ZONA 18S	
UTM:	
E: 284047.877	N: 8670248.981
GEOGRÁFICAS:	
Lat: -76.983572°	Lng: -12.021872°

PLANO DE UBICACIÓN

PROPIETARIO: ---	FIRMA Y SELLO:
UBICACIÓN: Habilitación Urbana Los Cedros - Mz. C Lt. 14	
LÁMINA: U-01	
FECHA: 25/1/2026	ESCALA: 1/5000