

PLANOS PRO

Sistema Profesional de Generación de Planos

PROYECTO:

Habilitación Urbana Los Cedros

LOTE:

MZ-C-Lote14

DOCUMENTO: MEMORIA DESCRIPTIVA

FECHA: 25 de enero de 2026

MEMORIA DESCRIPTIVA

I. IDENTIFICACIÓN DEL PREDIO

Código Catastral:	MZ-C-Lote14
Nombre del Lote:	Habilitación Urbana Los Cedros - MZ-C-Lote14
Manzana:	C
Etapas:	Habilitación Urbana Los Cedros
Número de Lote:	14
Estado:	LIBRE

II. UBICACIÓN GEOGRÁFICA

Sistema de Coordenadas:	UTM WGS84 - Zona 18S
Datum:	WGS84
Hemisferio:	Sur

III. CARACTERÍSTICAS MÉTRICAS DEL PREDIO

ÁREA TOTAL:	200.00 m²
PERÍMETRO TOTAL:	2377.26 ml
Frente:	10.00 ml
Fondo:	10.00 ml
Lado Derecho:	20.00 ml
Lado Izquierdo:	20.00 ml

IV. LINDEROS Y COLINDANCIAS

El predio tiene los siguientes linderos y colindancias:

PLANOS PRO

Sistema Profesional de Generación de Planos

PROYECTO:

Habilitación Urbana Los Cedros

LOTE:

MZ-C-Lote14

DOCUMENTO: MEMORIA DESCRIPTIVA

FECHA: 25 de enero de 2026

Por el NORTE: Con calle "Av. Los Alamos"

Por el SUR: Con lote "Lote 05"

Por el OESTE: Con lote "Lote 13"

Por el ESTE: Con lote "Lote 15"

V. CUADRO DE DATOS TÉCNICOS - COORDENADAS UTM

VÉRTICE	LADO	ESTE (m)	NORTE (m)
V1	V1-V2	285365.70	8670276.68
V2	V2-V3	285159.87	8670768.04
V3	V3-V4	285465.70	8670543.95
V4	V4-V5	285655.48	8670171.65
V5	V5-V6	285392.98	8670118.50
V6	V6-V7	285171.16	8670114.86
V7	V7-V1	285020.25	8670263.95

PROPIETARIO

Firma y Sello


PROFESIONAL RESPONSABLE

Ing. Civil / Arquitecto

Este documento ha sido generado automáticamente por el sistema PLANOS PRO

Código de Verificación: MZ-C-Lote14-MKUCU9OH

PLANO PERIMÉTRICO

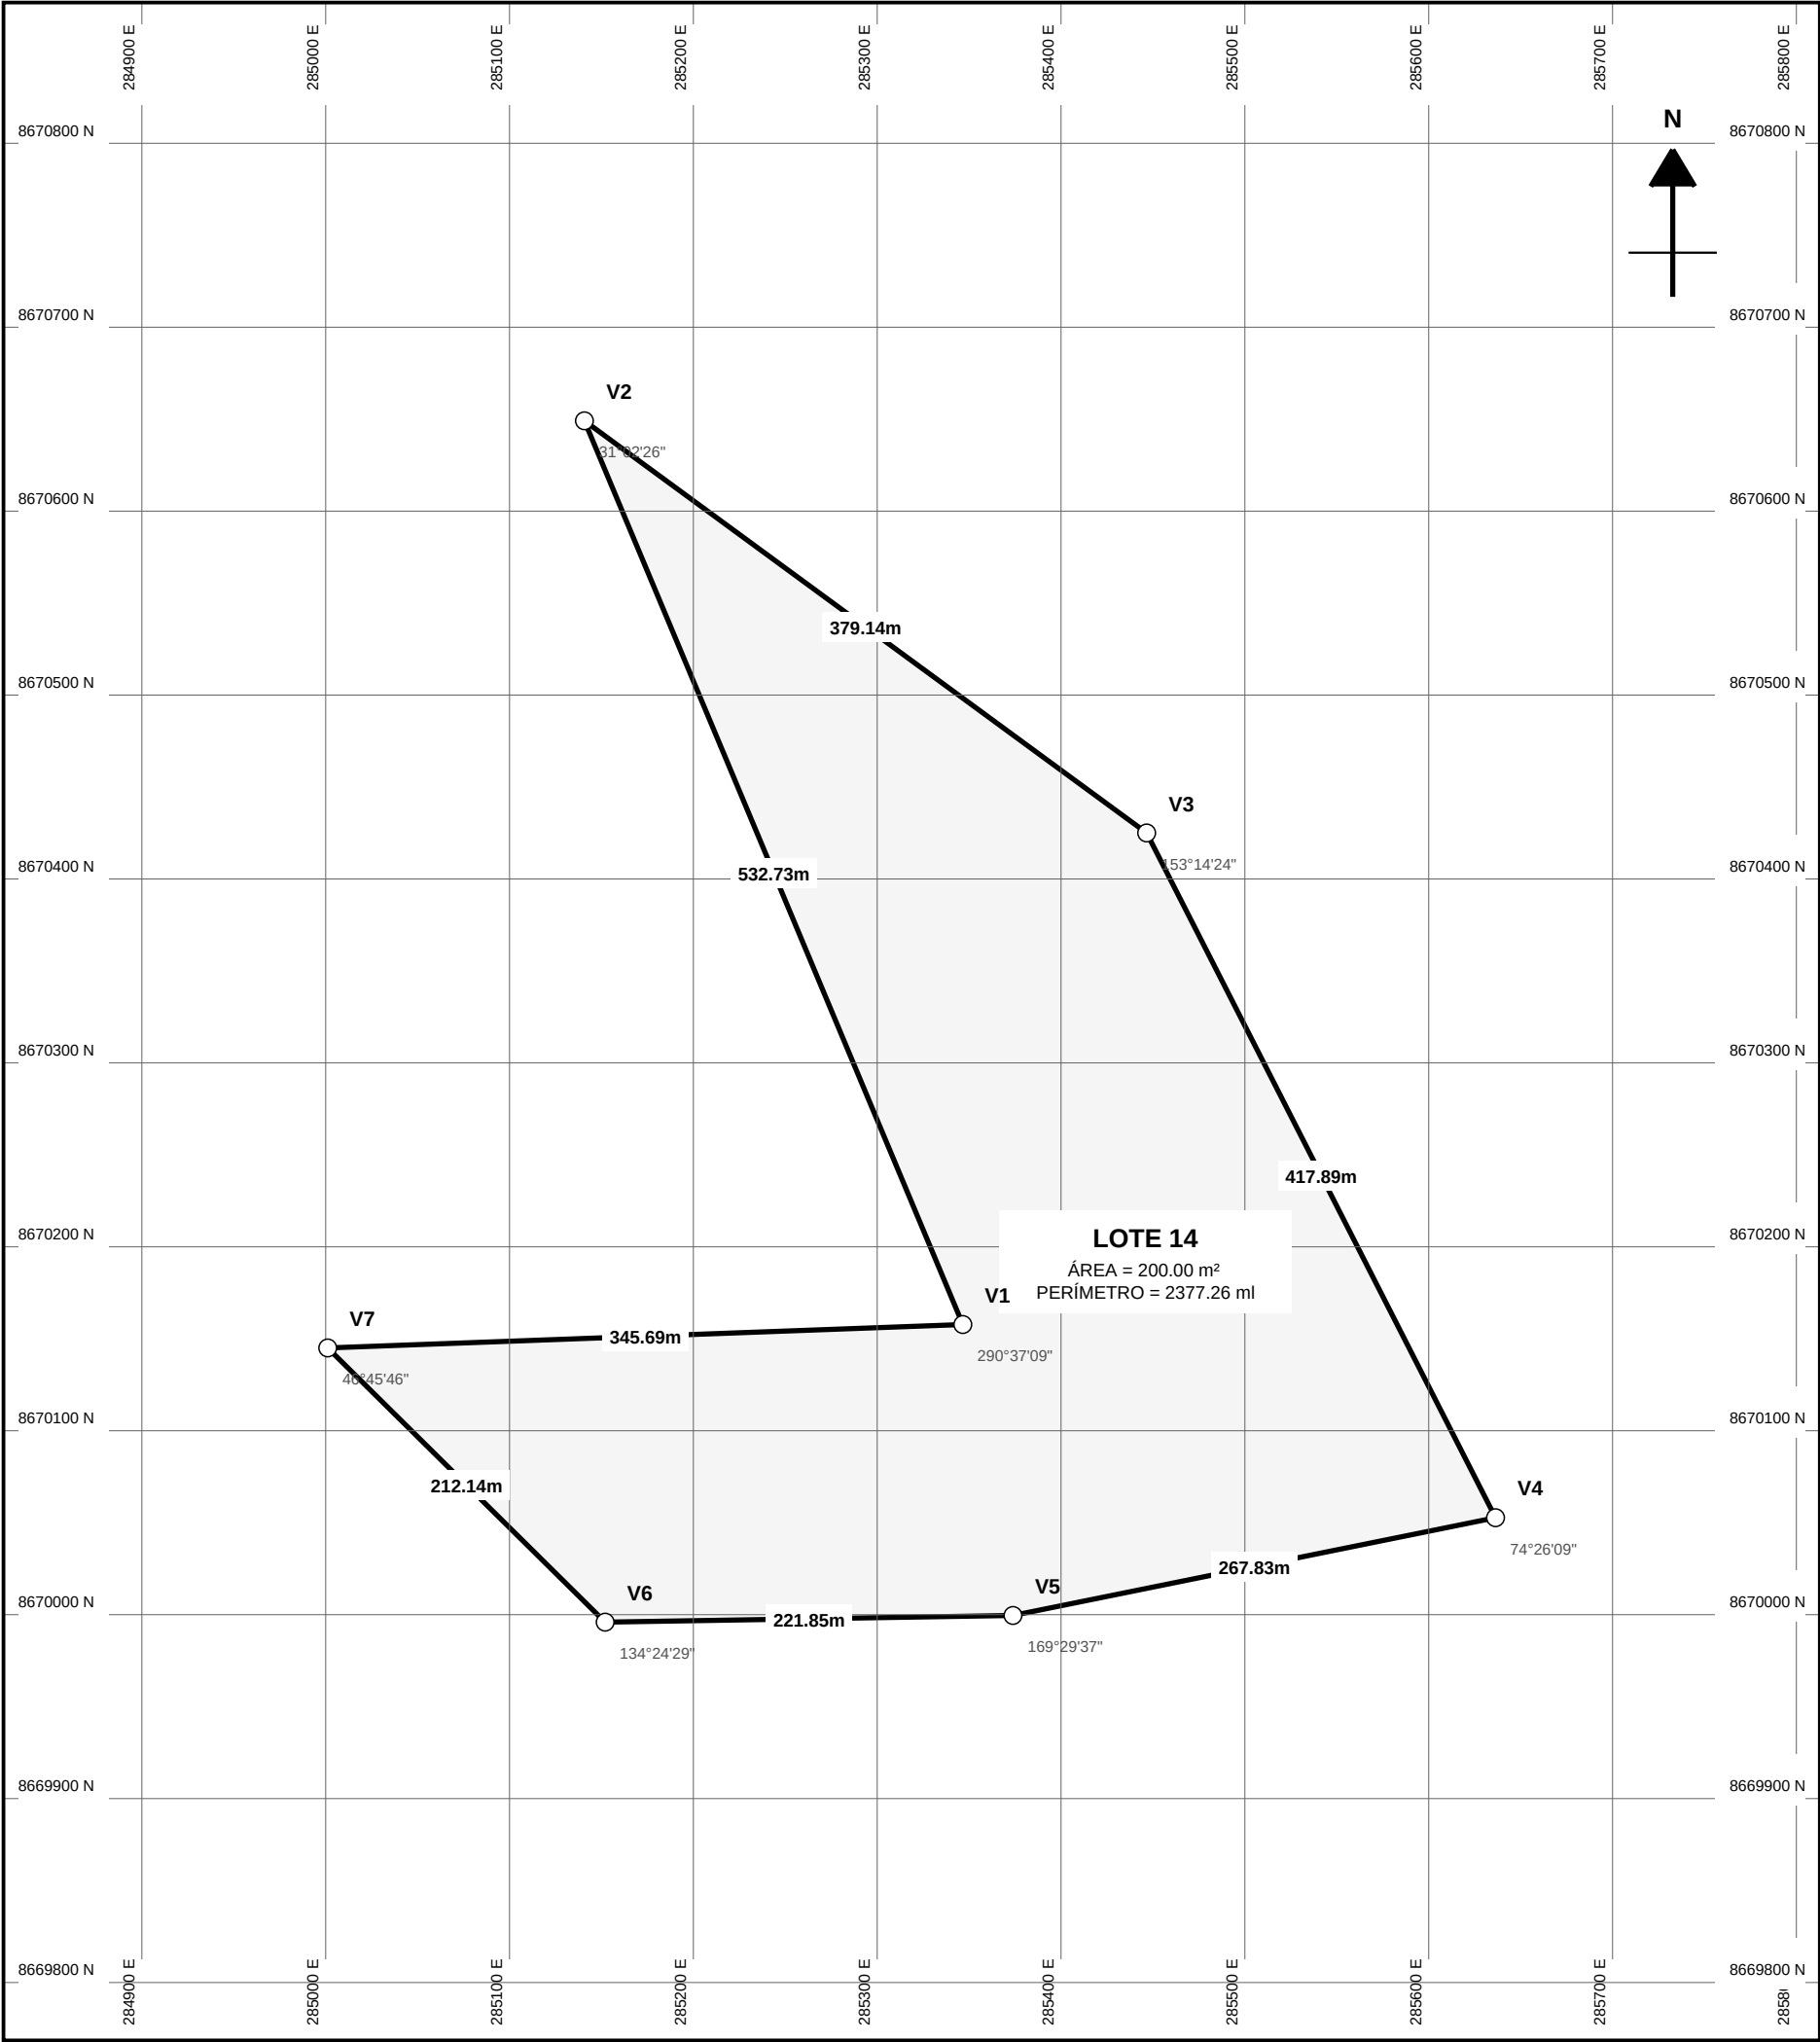


PLANO DE UBICACIÓN
ESCALA 1/1000

CUADRO DE DATOS TÉCNICOS - UTM WGS84

VÉRTICE	LADO	DIST (m)	ÁNGULO INT.	ESTE (X)	NORTE (Y)
V-1	V1-V2	532.73	290°37'09"	285365.705	8670276.682
V-2	V2-V3	379.14	31°02'26"	285159.872	8670768.040
V-3	V3-V4	417.89	153°14'24"	285465.705	8670543.955
V-4	V4-V5	267.83	74°26'09"	285655.483	8670171.648
V-5	V5-V6	221.85	169°29'37"	285392.977	8670118.500
V-6	V6-V7	212.14	134°24'29"	285171.159	8670114.864
V-7	V7-V1	345.69	46°45'46"	285020.250	8670263.955

PLANO
PERIMÉTRICO

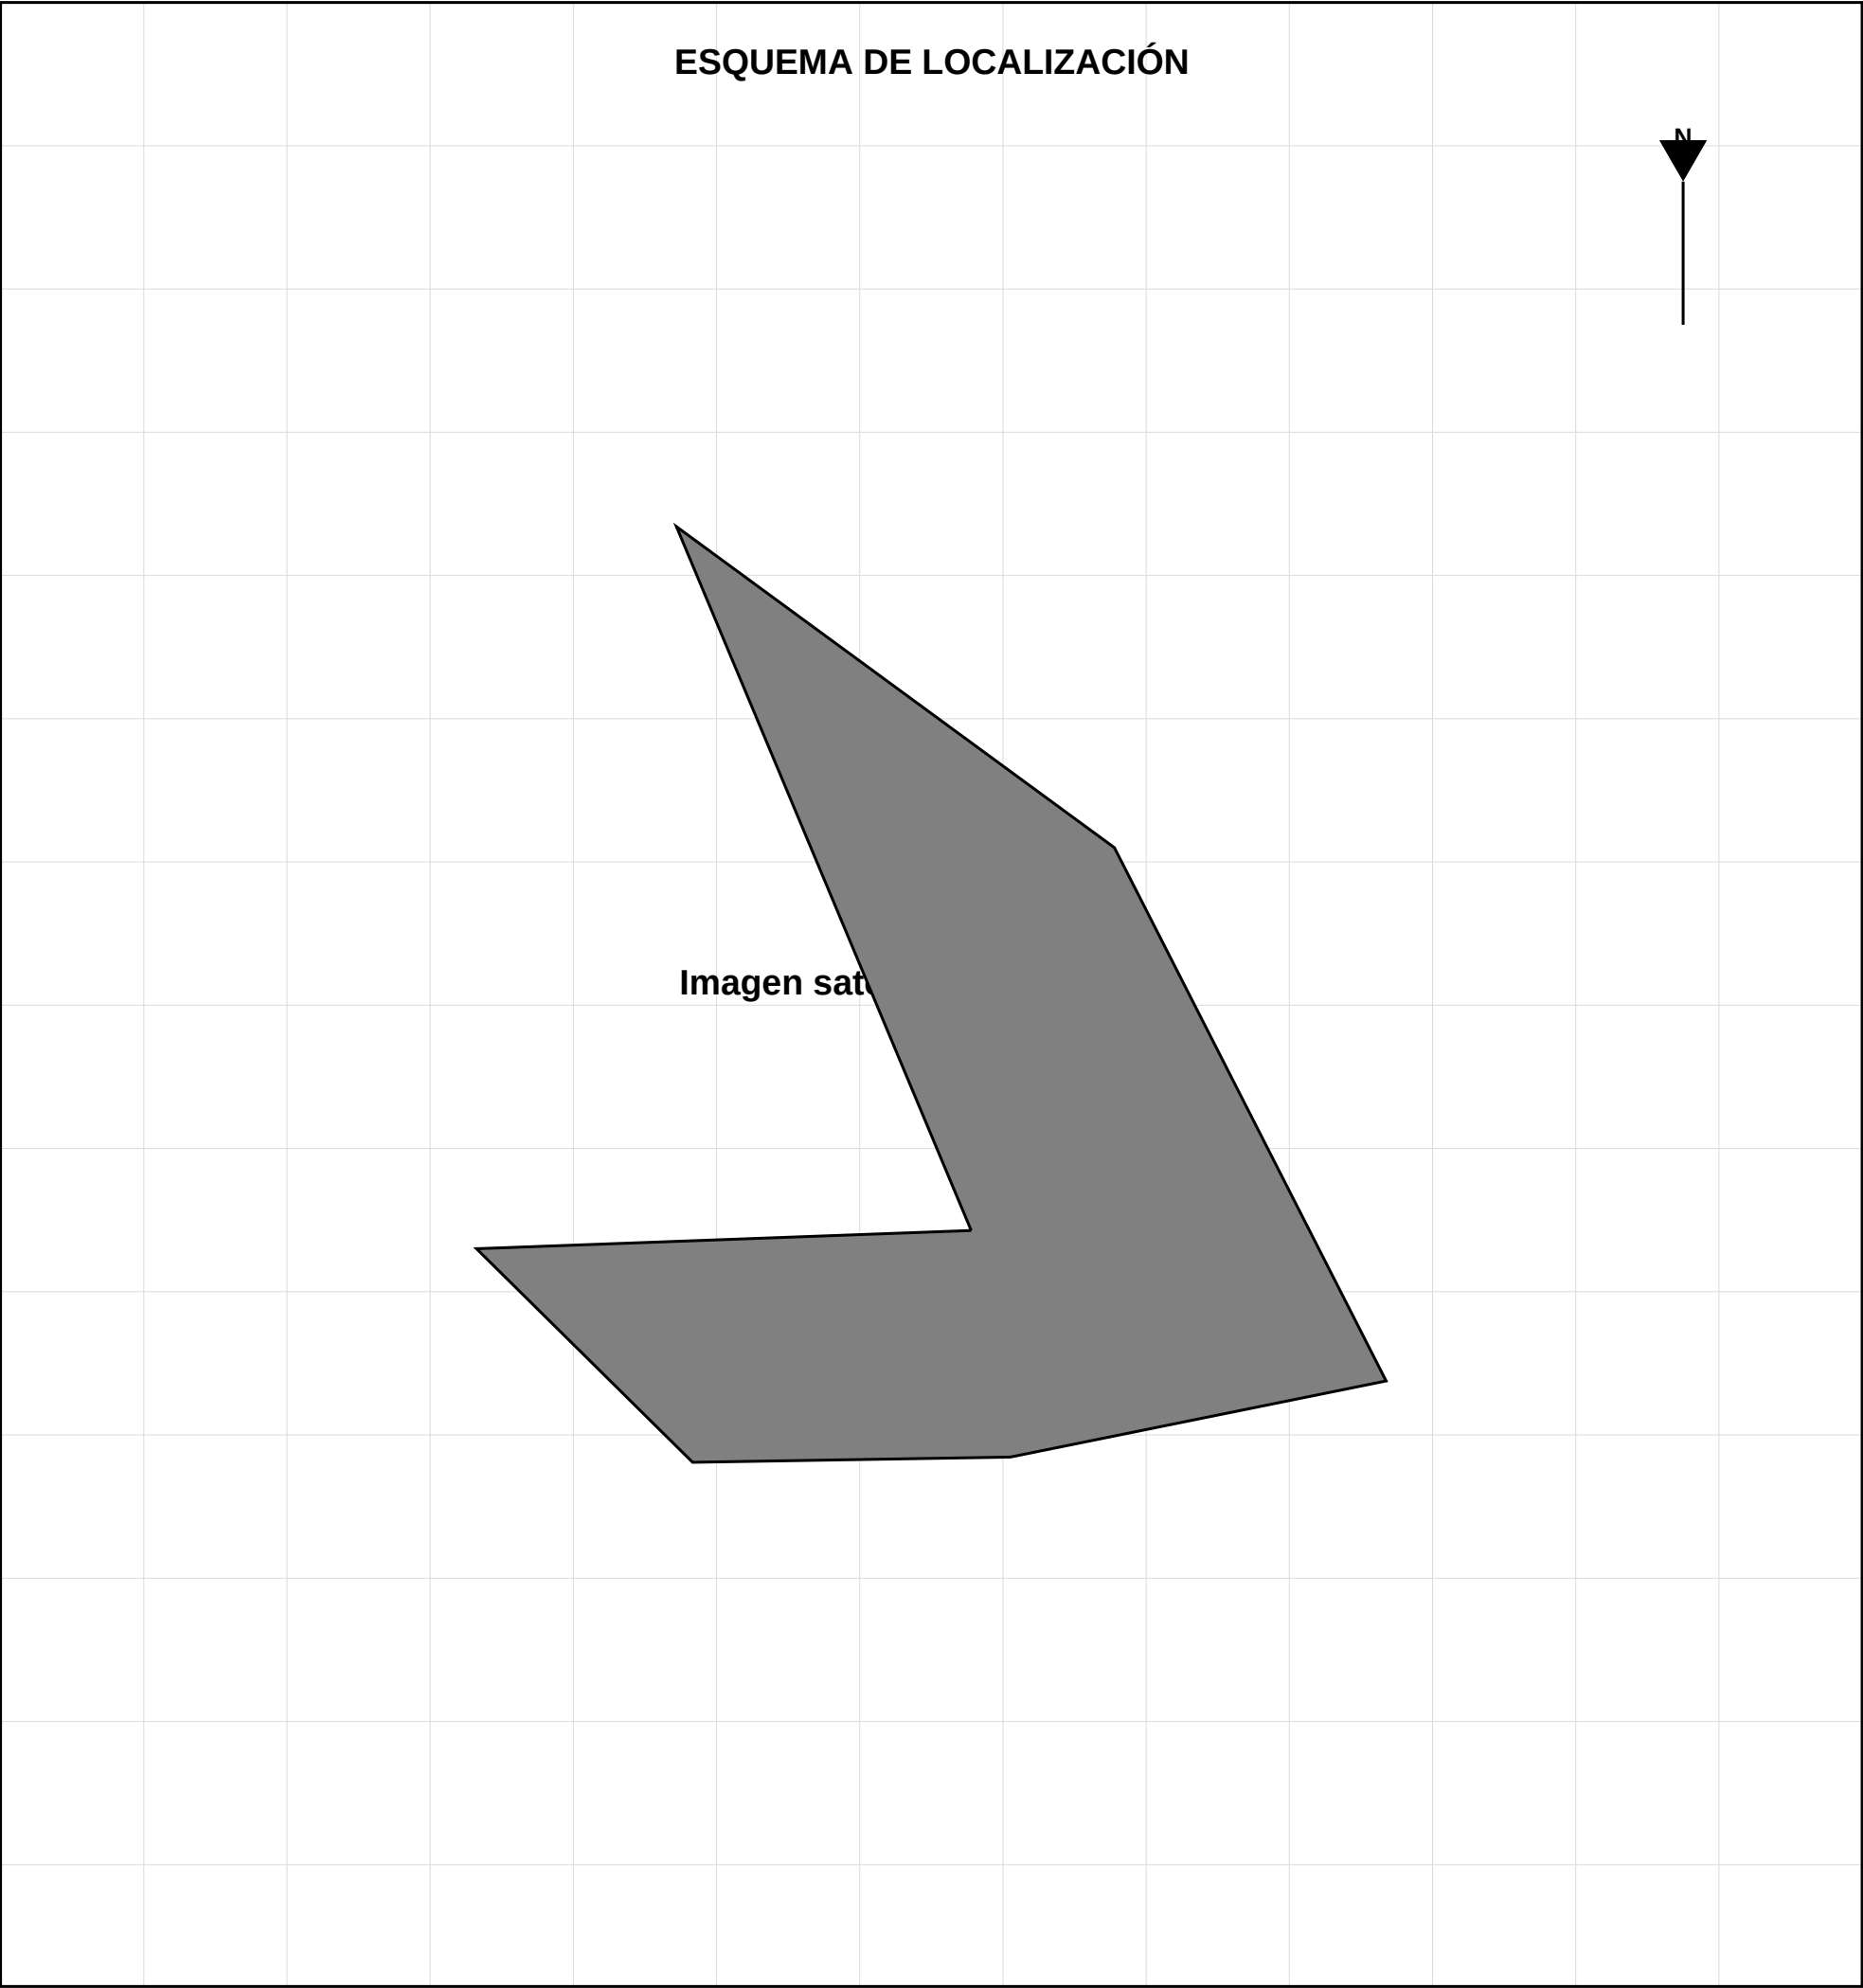

DATOS GENERALES	
Departamento:	Lima
Provincia:	Lima
Distrito:	Habilitación Urbana Los Cedros
Manzana:	C
Lote:	14
Área:	200.00 m²

COORDENADAS (CENTROIDE)	
UTM WGS84:	E: 285318.74 N: 8670322.52
GEOGRÁFICAS:	Lat: -76.97190 Lng: -12.02129

MACRO LOCALIZACIÓN
VISTA GENERAL PROYECTO

PLANO DE UBICACIÓN		
PROPIETARIO: ---		
UBICACIÓN: Mz. C Lt. 14		
FECHA: 25/1/2026		ESCALA: 1/5000