

PLANOS PRO

Sistema Profesional de Generación de Planos

PROYECTO:

Habilitación Urbana Los Cedros

LOTE:

MZ-C-Lote14

DOCUMENTO: MEMORIA DESCRIPTIVA

FECHA: 25 de enero de 2026

MEMORIA DESCRIPTIVA

I. IDENTIFICACIÓN DEL PREDIO

Código Catastral:	MZ-C-Lote14
Nombre del Lote:	Habilitación Urbana Los Cedros - MZ-C-Lote14
Manzana:	C
Etapas:	Habilitación Urbana Los Cedros
Número de Lote:	14
Estado:	LIBRE

II. UBICACIÓN GEOGRÁFICA

Sistema de Coordenadas:	UTM WGS84 - Zona 18S
Datum:	WGS84
Hemisferio:	Sur

III. CARACTERÍSTICAS MÉTRICAS DEL PREDIO

ÁREA TOTAL:	200.00 m ²
PERÍMETRO TOTAL:	81.32 ml
Frente:	10.00 ml
Fondo:	10.00 ml
Lado Derecho:	20.00 ml
Lado Izquierdo:	20.00 ml

IV. LINDEROS Y COLINDANCIAS

El predio tiene los siguientes linderos y colindancias:

PLANOS PRO

Sistema Profesional de Generación de Planos

PROYECTO:

Habilitación Urbana Los Cedros

LOTE:

MZ-C-Lote14

DOCUMENTO: MEMORIA DESCRIPTIVA

FECHA: 25 de enero de 2026

Por el NORTE: Con calle "Av. Los Alamos"

Por el SUR: Con lote "Lote 05"

Por el OESTE: Con lote "Lote 13"

Por el ESTE: Con lote "Lote 15"

V. CUADRO DE DATOS TÉCNICOS - COORDENADAS UTM

VÉRTICE	LADO	ESTE (m)	NORTE (m)
V1	V1-V2	284497.57	8670105.72
V2	V2-V3	284511.41	8670105.79
V3	V3-V4	284511.28	8670082.88
V4	V4-V1	284490.35	8670083.22

PROPIETARIO

Firma y Sello


PROFESIONAL RESPONSABLE

Ing. Civil / Arquitecto

Este documento ha sido generado automáticamente por el sistema PLANOS PRO

Código de Verificación: MZ-C-Lote14-MKUEQ1PI

PLANO PERIMÉTRICO

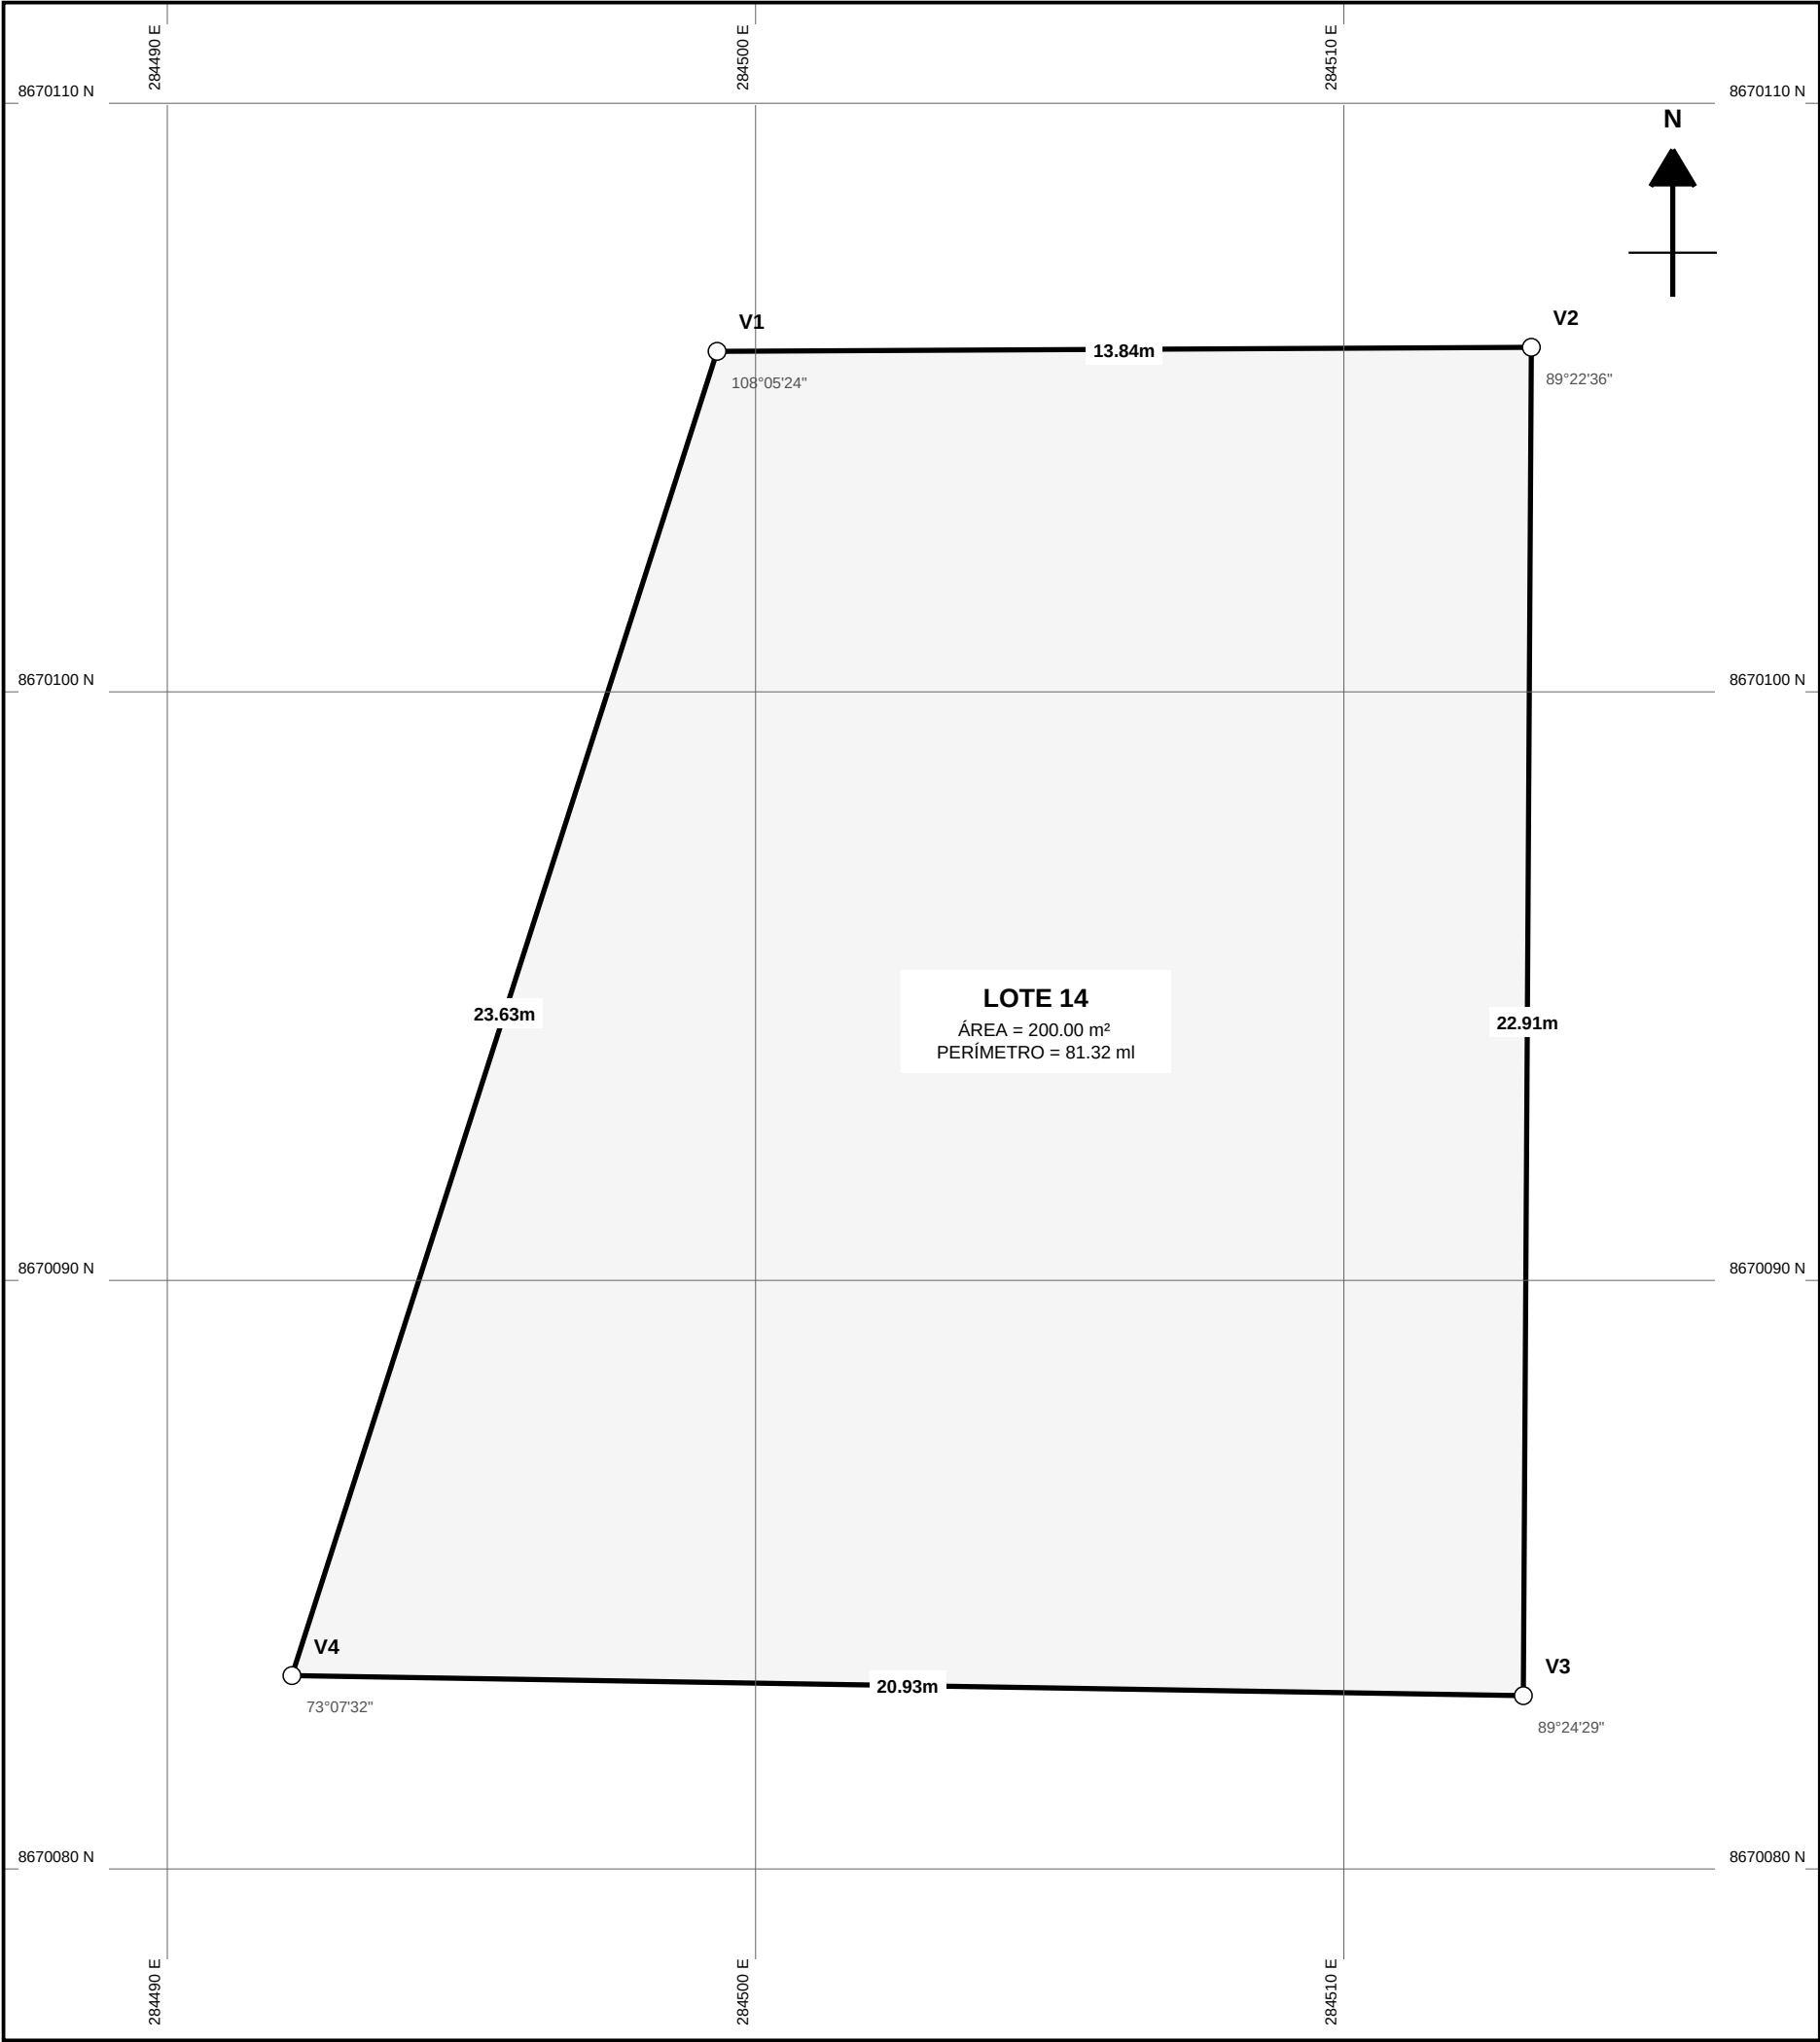


PLANO DE UBICACIÓN
ESCALA 1/1000

CUADRO DE DATOS TÉCNICOS - UTM WGS84

VÉRTICE	LADO	DIST (m)	ÁNGULO INT.	ESTE (X)	NORTE (Y)
V-1	V1-V2	13.84	108°05'24"	284497.573	8670105.717
V-2	V2-V3	22.91	89°22'36"	284511.414	8670105.786
V-3	V3-V4	20.93	89°24'29"	284511.278	8670082.876
V-4	V4-V1	23.63	73°07'32"	284490.346	8670083.217

PLANO
PERIMÉTRICO

ESQUEMA DE LOCALIZACIÓN

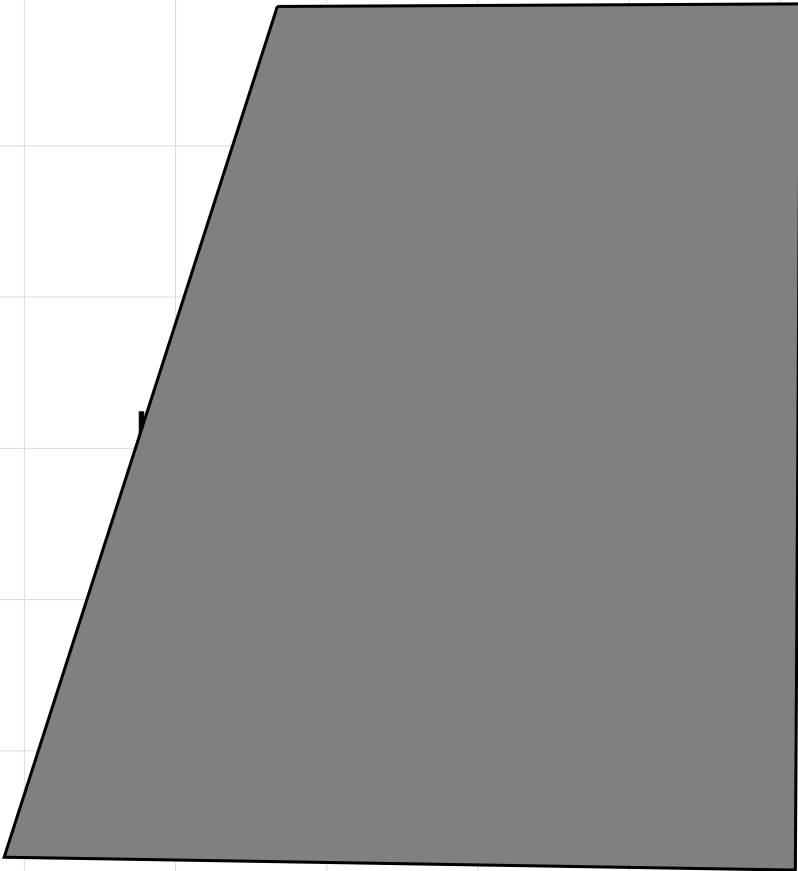

DATOS GENERALES

Departamento:	Lima
Provincia:	Lima
Distrito:	Habilitación Urbana Los Cedros
Manzana:	C
Lote:	14
Área:	200.00 m²

COORDENADAS (CENTROIDE)

UTM WGS84:	E: 284502.65 N: 8670094.40
GEOGRÁFICAS:	Lat: -76.97941 Lng: -12.02330

MACRO LOCALIZACIÓN

VISTA GENERAL PROYECTO

PLANO DE UBICACIÓN

PROPIETARIO: ---

UBICACIÓN: Mz. C Lt. 14

FECHA: 25/1/2026

ESCALA: 1/200