

PLANOS PRO

Sistema Profesional de Generación de Planos

PROYECTO:

Habilitación Urbana Los Cedros

LOTE:

MZ-C-Lote14

DOCUMENTO: MEMORIA DESCRIPTIVA

FECHA: 26 de enero de 2026

MEMORIA DESCRIPTIVA

I. IDENTIFICACIÓN DEL PREDIO

Código Catastral:	MZ-C-Lote14
Nombre del Lote:	Habilitación Urbana Los Cedros - MZ-C-Lote14
Manzana:	C
Etapas:	Habilitación Urbana Los Cedros
Número de Lote:	14
Estado:	LIBRE

II. UBICACIÓN GEOGRÁFICA

Sistema de Coordenadas:	UTM WGS84 - Zona 18S
Datum:	WGS84
Hemisferio:	Sur

III. CARACTERÍSTICAS MÉTRICAS DEL PREDIO

ÁREA TOTAL:	200.00 m ²
PERÍMETRO TOTAL:	70.88 ml
Frente:	10.00 ml
Fondo:	10.00 ml
Lado Derecho:	20.00 ml
Lado Izquierdo:	20.00 ml

IV. LINDEROS Y COLINDANCIAS

El predio tiene los siguientes linderos y colindancias:

PLANOS PRO

Sistema Profesional de Generación de Planos

PROYECTO:

Habilitación Urbana Los Cedros

LOTE:

MZ-C-Lote14

DOCUMENTO: MEMORIA DESCRIPTIVA

FECHA: 26 de enero de 2026

Por el NORTE: Con calle "Av. Los Alamos"

Por el SUR: Con lote "Lote 05"

Por el OESTE: Con lote "Lote 13"

Por el ESTE: Con lote "Lote 15"

V. CUADRO DE DATOS TÉCNICOS - COORDENADAS UTM

VÉRTICE	LADO	ESTE (m)	NORTE (m)
V1	V1-V2	308499.07	8622744.69
V2	V2-V3	308493.21	8622743.40
V3	V3-V4	308497.50	8622723.87
V4	V4-V5	308503.36	8622725.16
V5	V5-V6	308491.64	8622722.58
V6	V6-V1	308497.50	8622723.87

PROPIETARIO

Firma y Sello


PROFESIONAL RESPONSABLE

Ing. Civil / Arquitecto

Este documento ha sido generado automáticamente por el sistema PLANOS PRO

Código de Verificación: MZ-C-Lote14-MKUSVTYB

PLANO PERIMÉTRICO

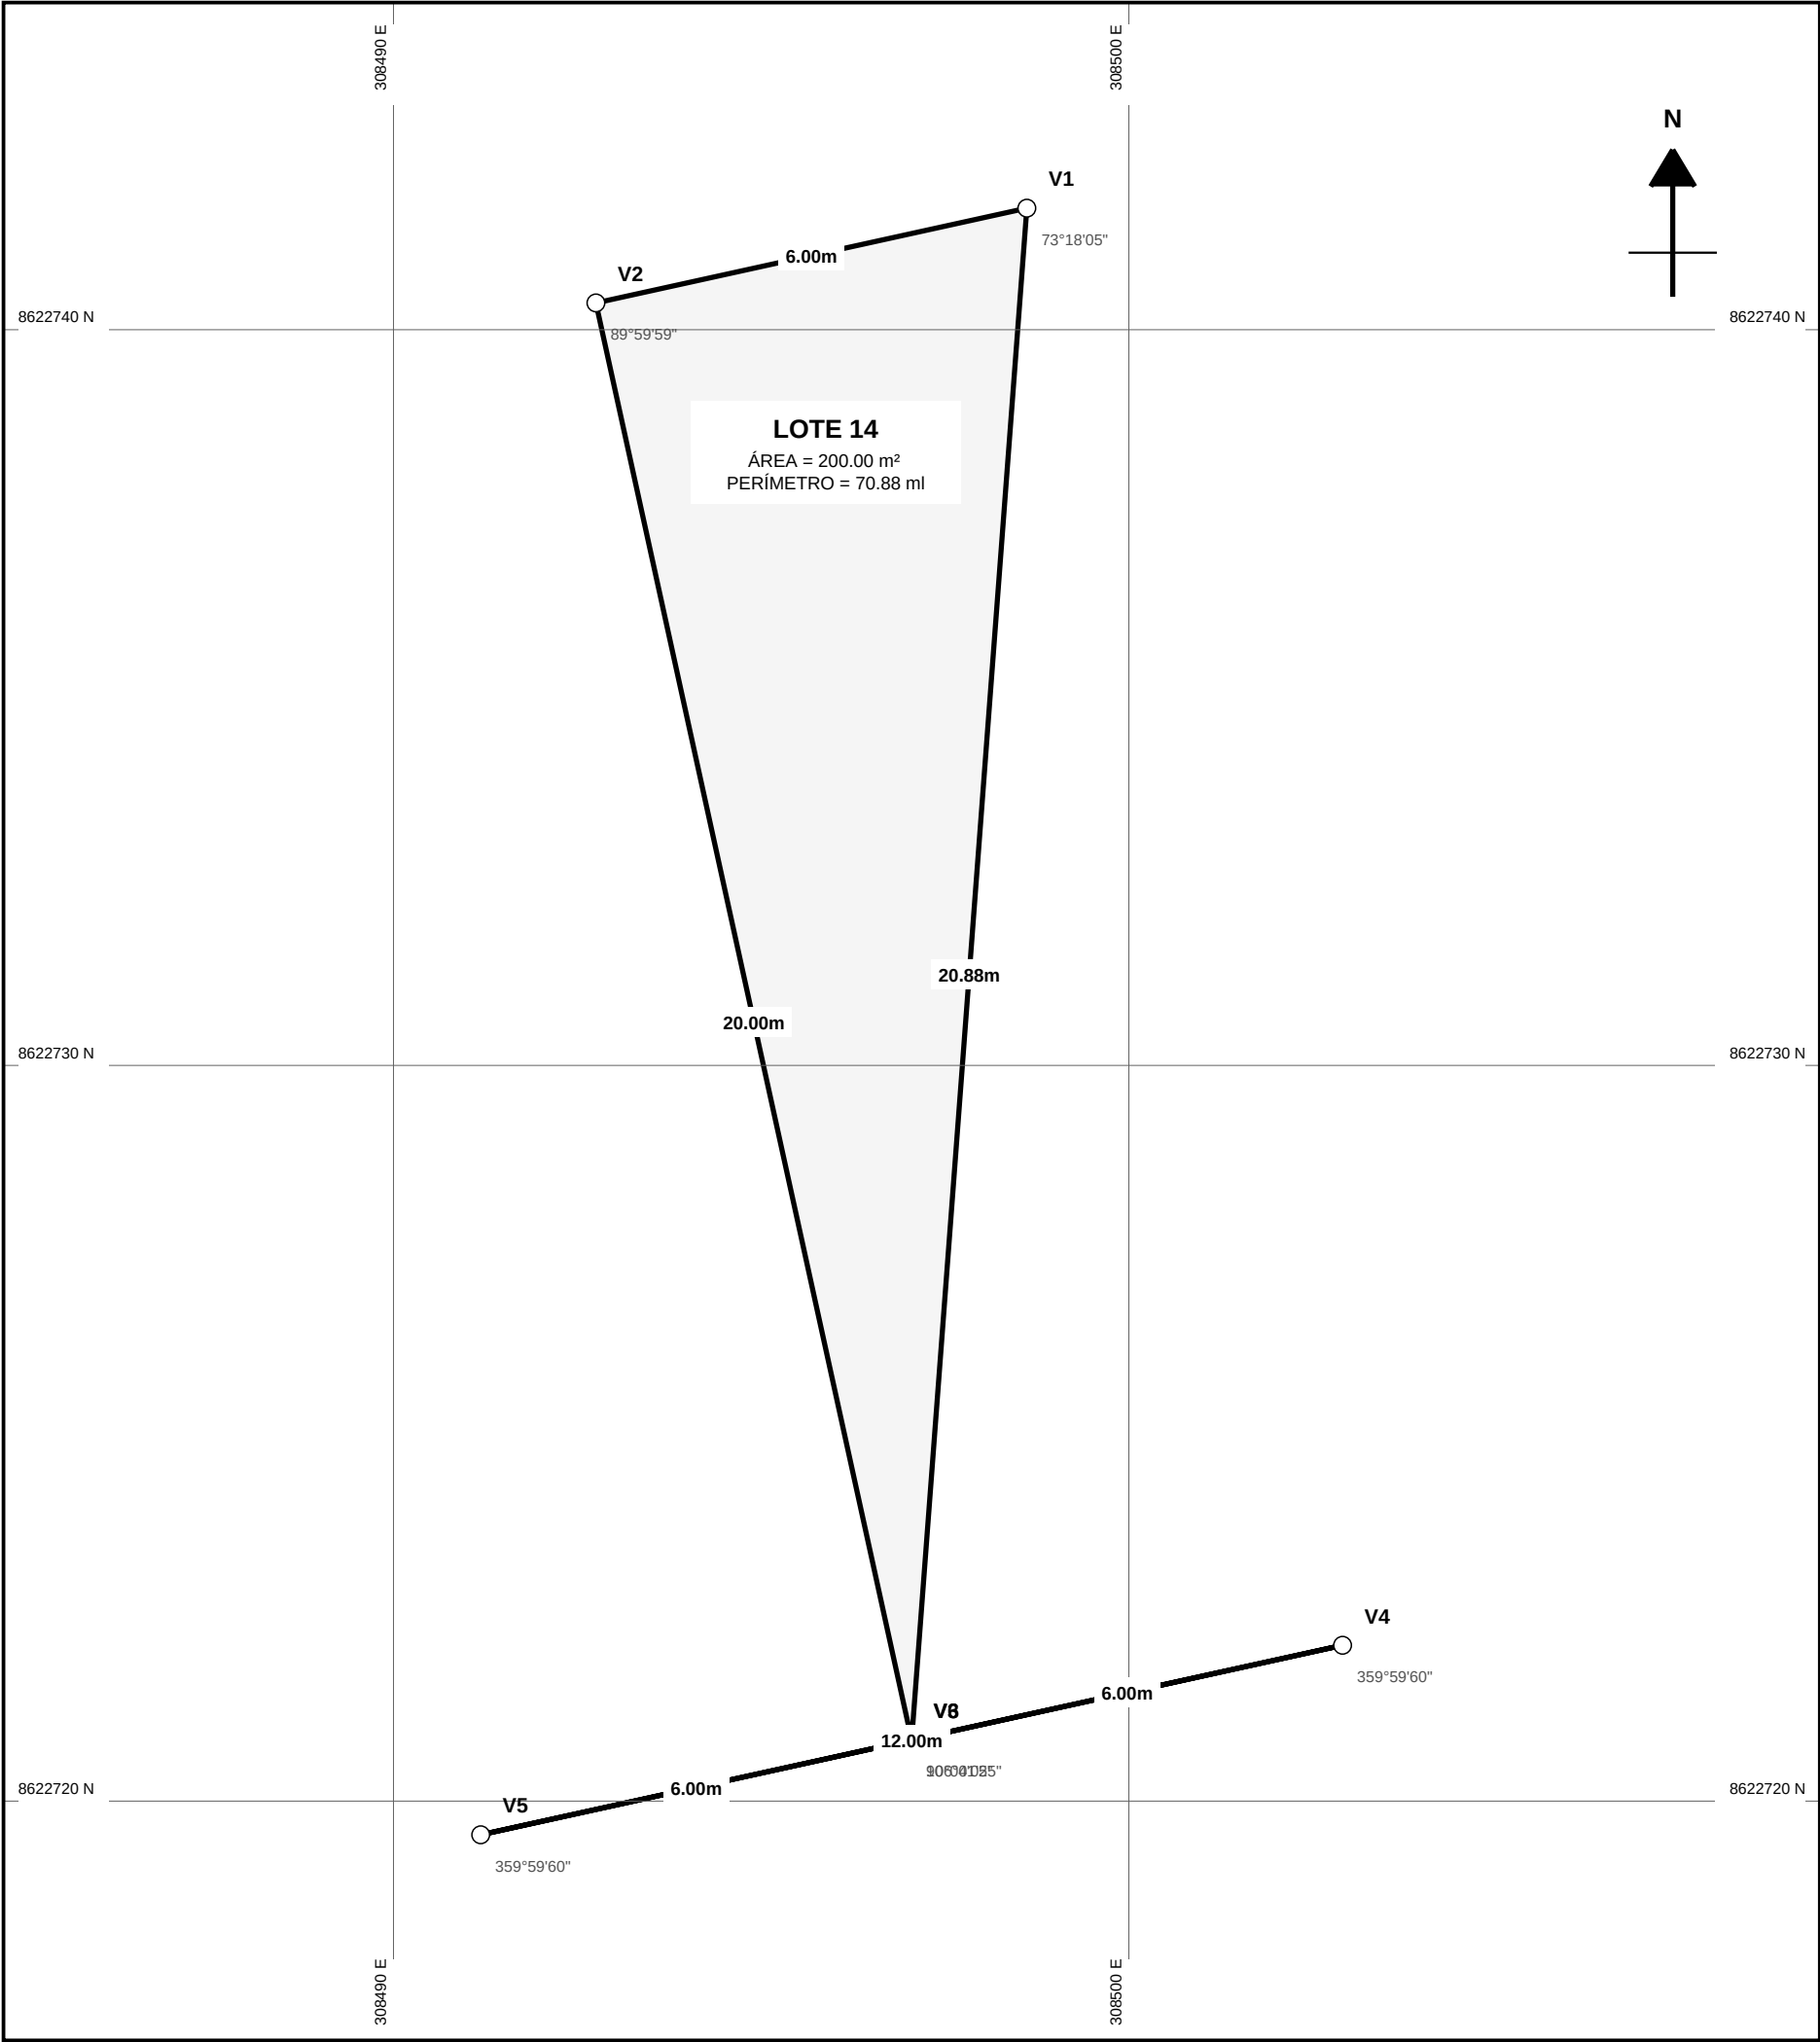

PLANO DE UBICACIÓN
ESCALA 1/1000

CUADRO DE DATOS TÉCNICOS - UTM WGS84

VÉRTICE	LADO	DIST (m)	ÁNGULO INT.	ESTE (X)	NORTE (Y)
V-1	V1-V2	6.00	73°18'05"	308499.067	8622744.693
V-2	V2-V3	20.00	89°59'59"	308493.207	8622743.405
V-3	V3-V4	6.00	90°00'02"	308497.501	8622723.871
V-4	V4-V5	12.00	359°59'60"	308503.361	8622725.159
V-5	V5-V6	6.00	359°59'60"	308491.641	8622722.583
V-6	V6-V1	20.88	106°41'55"	308497.501	8622723.871

PLANO
PERIMÉTRICO

ESQUEMA DE LOCALIZACIÓN



Imagen satelital no disponible

DATOS GENERALES

Departamento:	Lima
Provincia:	Lima
Distrito:	Habilitación Urbana Los Cedros
Manzana:	C
Lote:	14
Área:	200.00 m²

COORDENADAS (CENTROIDE)

UTM WGS84:	E: 308497.05 N: 8622730.60
GEOGRÁFICAS:	Lat: -76.76192 Lng: -12.45289

MACRO LOCALIZACIÓN

VISTA GENERAL PROYECTO

PLANO DE UBICACIÓN

PROPIETARIO: ---

UBICACIÓN: Mz. C Lt. 14

FECHA: 26/1/2026

ESCALA: 1/200