

# PLANOS PRO

Sistema Profesional de Generación de Planos

## PROYECTO:

Habilitación Urbana Los Cedros

## LOTE:

MZ-C-Lote14

DOCUMENTO: MEMORIA DESCRIPTIVA

FECHA: 26 de enero de 2026

## MEMORIA DESCRIPTIVA

### I. IDENTIFICACIÓN DEL PREDIO

|                   |                                              |
|-------------------|----------------------------------------------|
| Código Catastral: | MZ-C-Lote14                                  |
| Nombre del Lote:  | Habilitación Urbana Los Cedros - MZ-C-Lote14 |
| Manzana:          | C                                            |
| Etapas:           | Habilitación Urbana Los Cedros               |
| Número de Lote:   | 14                                           |
| Estado:           | LIBRE                                        |

### II. UBICACIÓN GEOGRÁFICA

|                         |                      |
|-------------------------|----------------------|
| Sistema de Coordenadas: | UTM WGS84 - Zona 18S |
| Datum:                  | WGS84                |
| Hemisferio:             | Sur                  |

### III. CARACTERÍSTICAS MÉTRICAS DEL PREDIO

|                  |                       |
|------------------|-----------------------|
| ÁREA TOTAL:      | 200.00 m <sup>2</sup> |
| PERÍMETRO TOTAL: | 72.16 ml              |
| Frente:          | 10.00 ml              |
| Fondo:           | 10.00 ml              |
| Lado Derecho:    | 20.00 ml              |
| Lado Izquierdo:  | 20.00 ml              |

### IV. LINDEROS Y COLINDANCIAS

El predio tiene los siguientes linderos y colindancias:

# PLANOS PRO

Sistema Profesional de Generación de Planos

## PROYECTO:

Habilitación Urbana Los Cedros

## LOTE:

MZ-C-Lote14

DOCUMENTO: MEMORIA DESCRIPTIVA

FECHA: 26 de enero de 2026

Por el NORTE: Con calle "Av. Los Alamos"

Por el SUR: Con lote "Lote 05"

Por el OESTE: Con lote "Lote 13"

Por el ESTE: Con lote "Lote 15"

## V. CUADRO DE DATOS TÉCNICOS - COORDENADAS UTM

| VÉRTICE | LADO  | ESTE (m)  | NORTE (m)  |
|---------|-------|-----------|------------|
| V1      | V1-V2 | 284495.67 | 8670106.19 |
| V2      | V2-V3 | 284510.00 | 8670100.00 |
| V3      | V3-V4 | 284510.00 | 8670080.00 |
| V4      | V4-V1 | 284500.00 | 8670080.00 |

PROPIETARIO

Firma y Sello


PROFESIONAL RESPONSABLE

Ing. Civil / Arquitecto

Este documento ha sido generado automáticamente por el sistema PLANOS PRO

Código de Verificación: MZ-C-Lote14-MKVE2NEY

PLANO PERIMÉTRICO

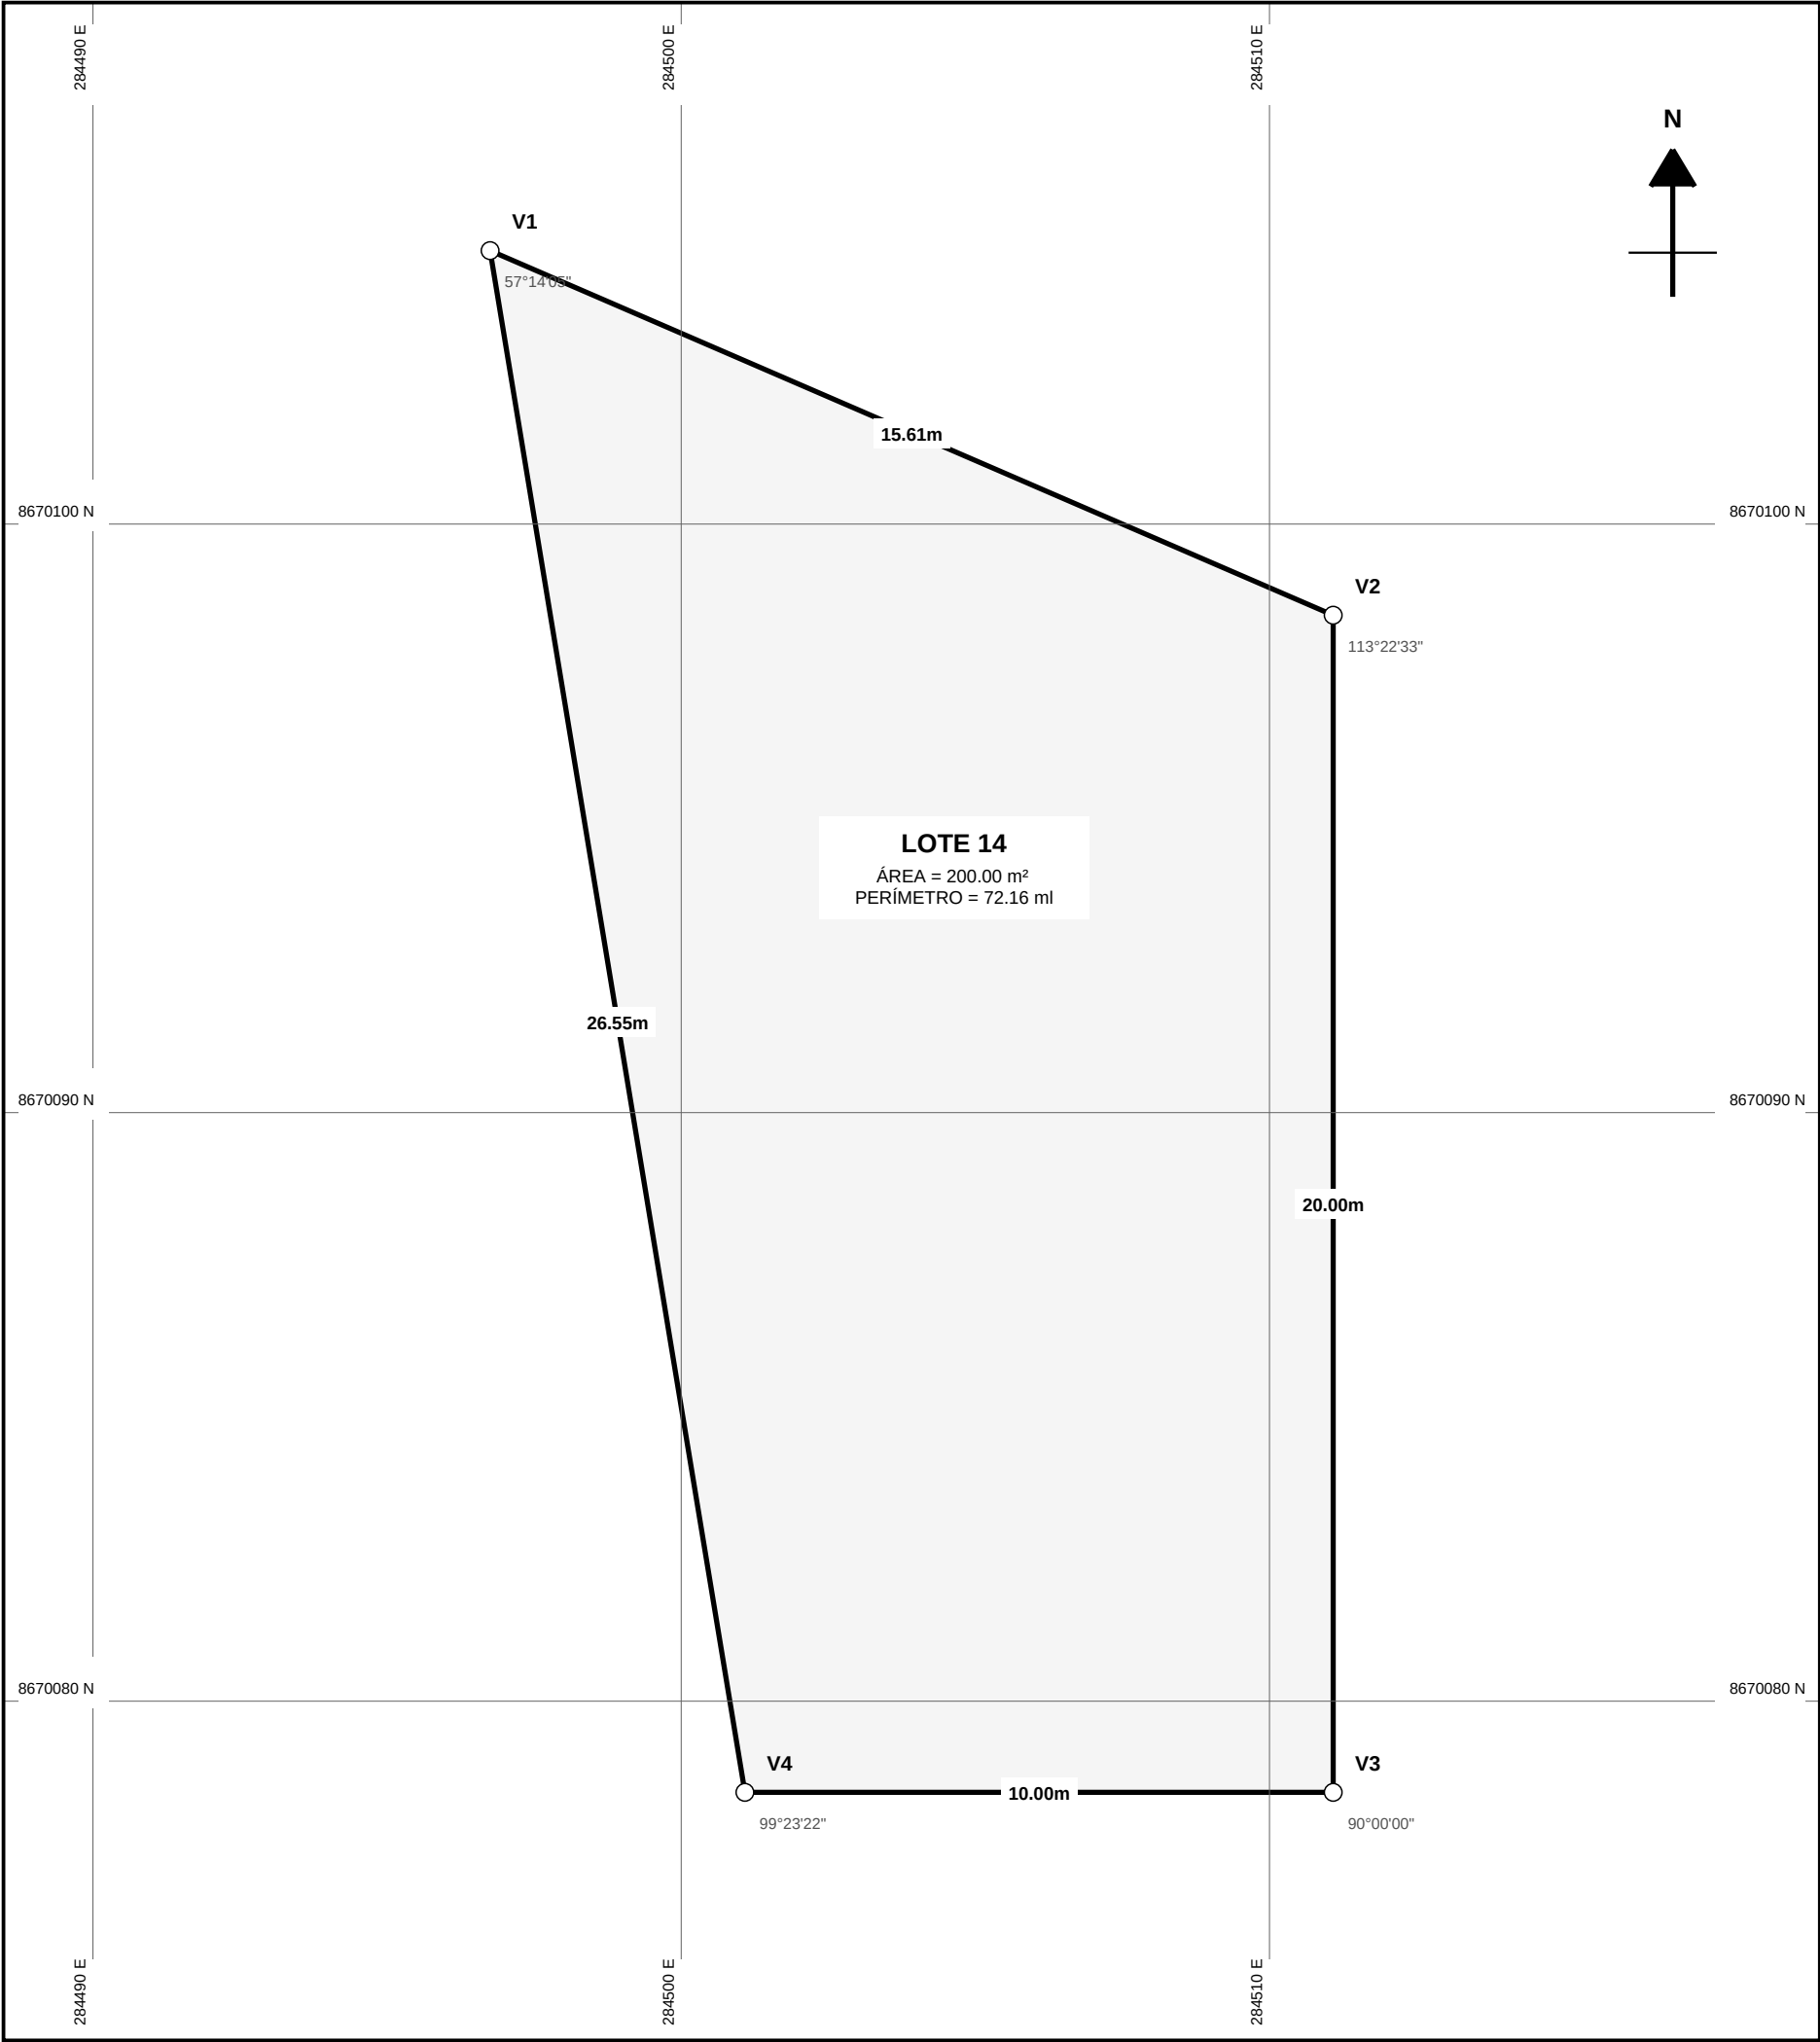


PLANO DE UBICACIÓN  
ESCALA 1/1000

CUADRO DE DATOS TÉCNICOS - UTM WGS84

| VÉRTICE | LADO  | DIST (m) | ÁNGULO INT. | ESTE (X)   | NORTE (Y)   |
|---------|-------|----------|-------------|------------|-------------|
| V-1     | V1-V2 | 15.61    | 57°14'05"   | 284495.668 | 8670106.195 |
| V-2     | V2-V3 | 20.00    | 113°22'33"  | 284510.000 | 8670100.000 |
| V-3     | V3-V4 | 10.00    | 90°00'00"   | 284510.000 | 8670080.000 |
| V-4     | V4-V1 | 26.55    | 99°23'22"   | 284500.000 | 8670080.000 |

PLANO  
PERIMÉTRICO

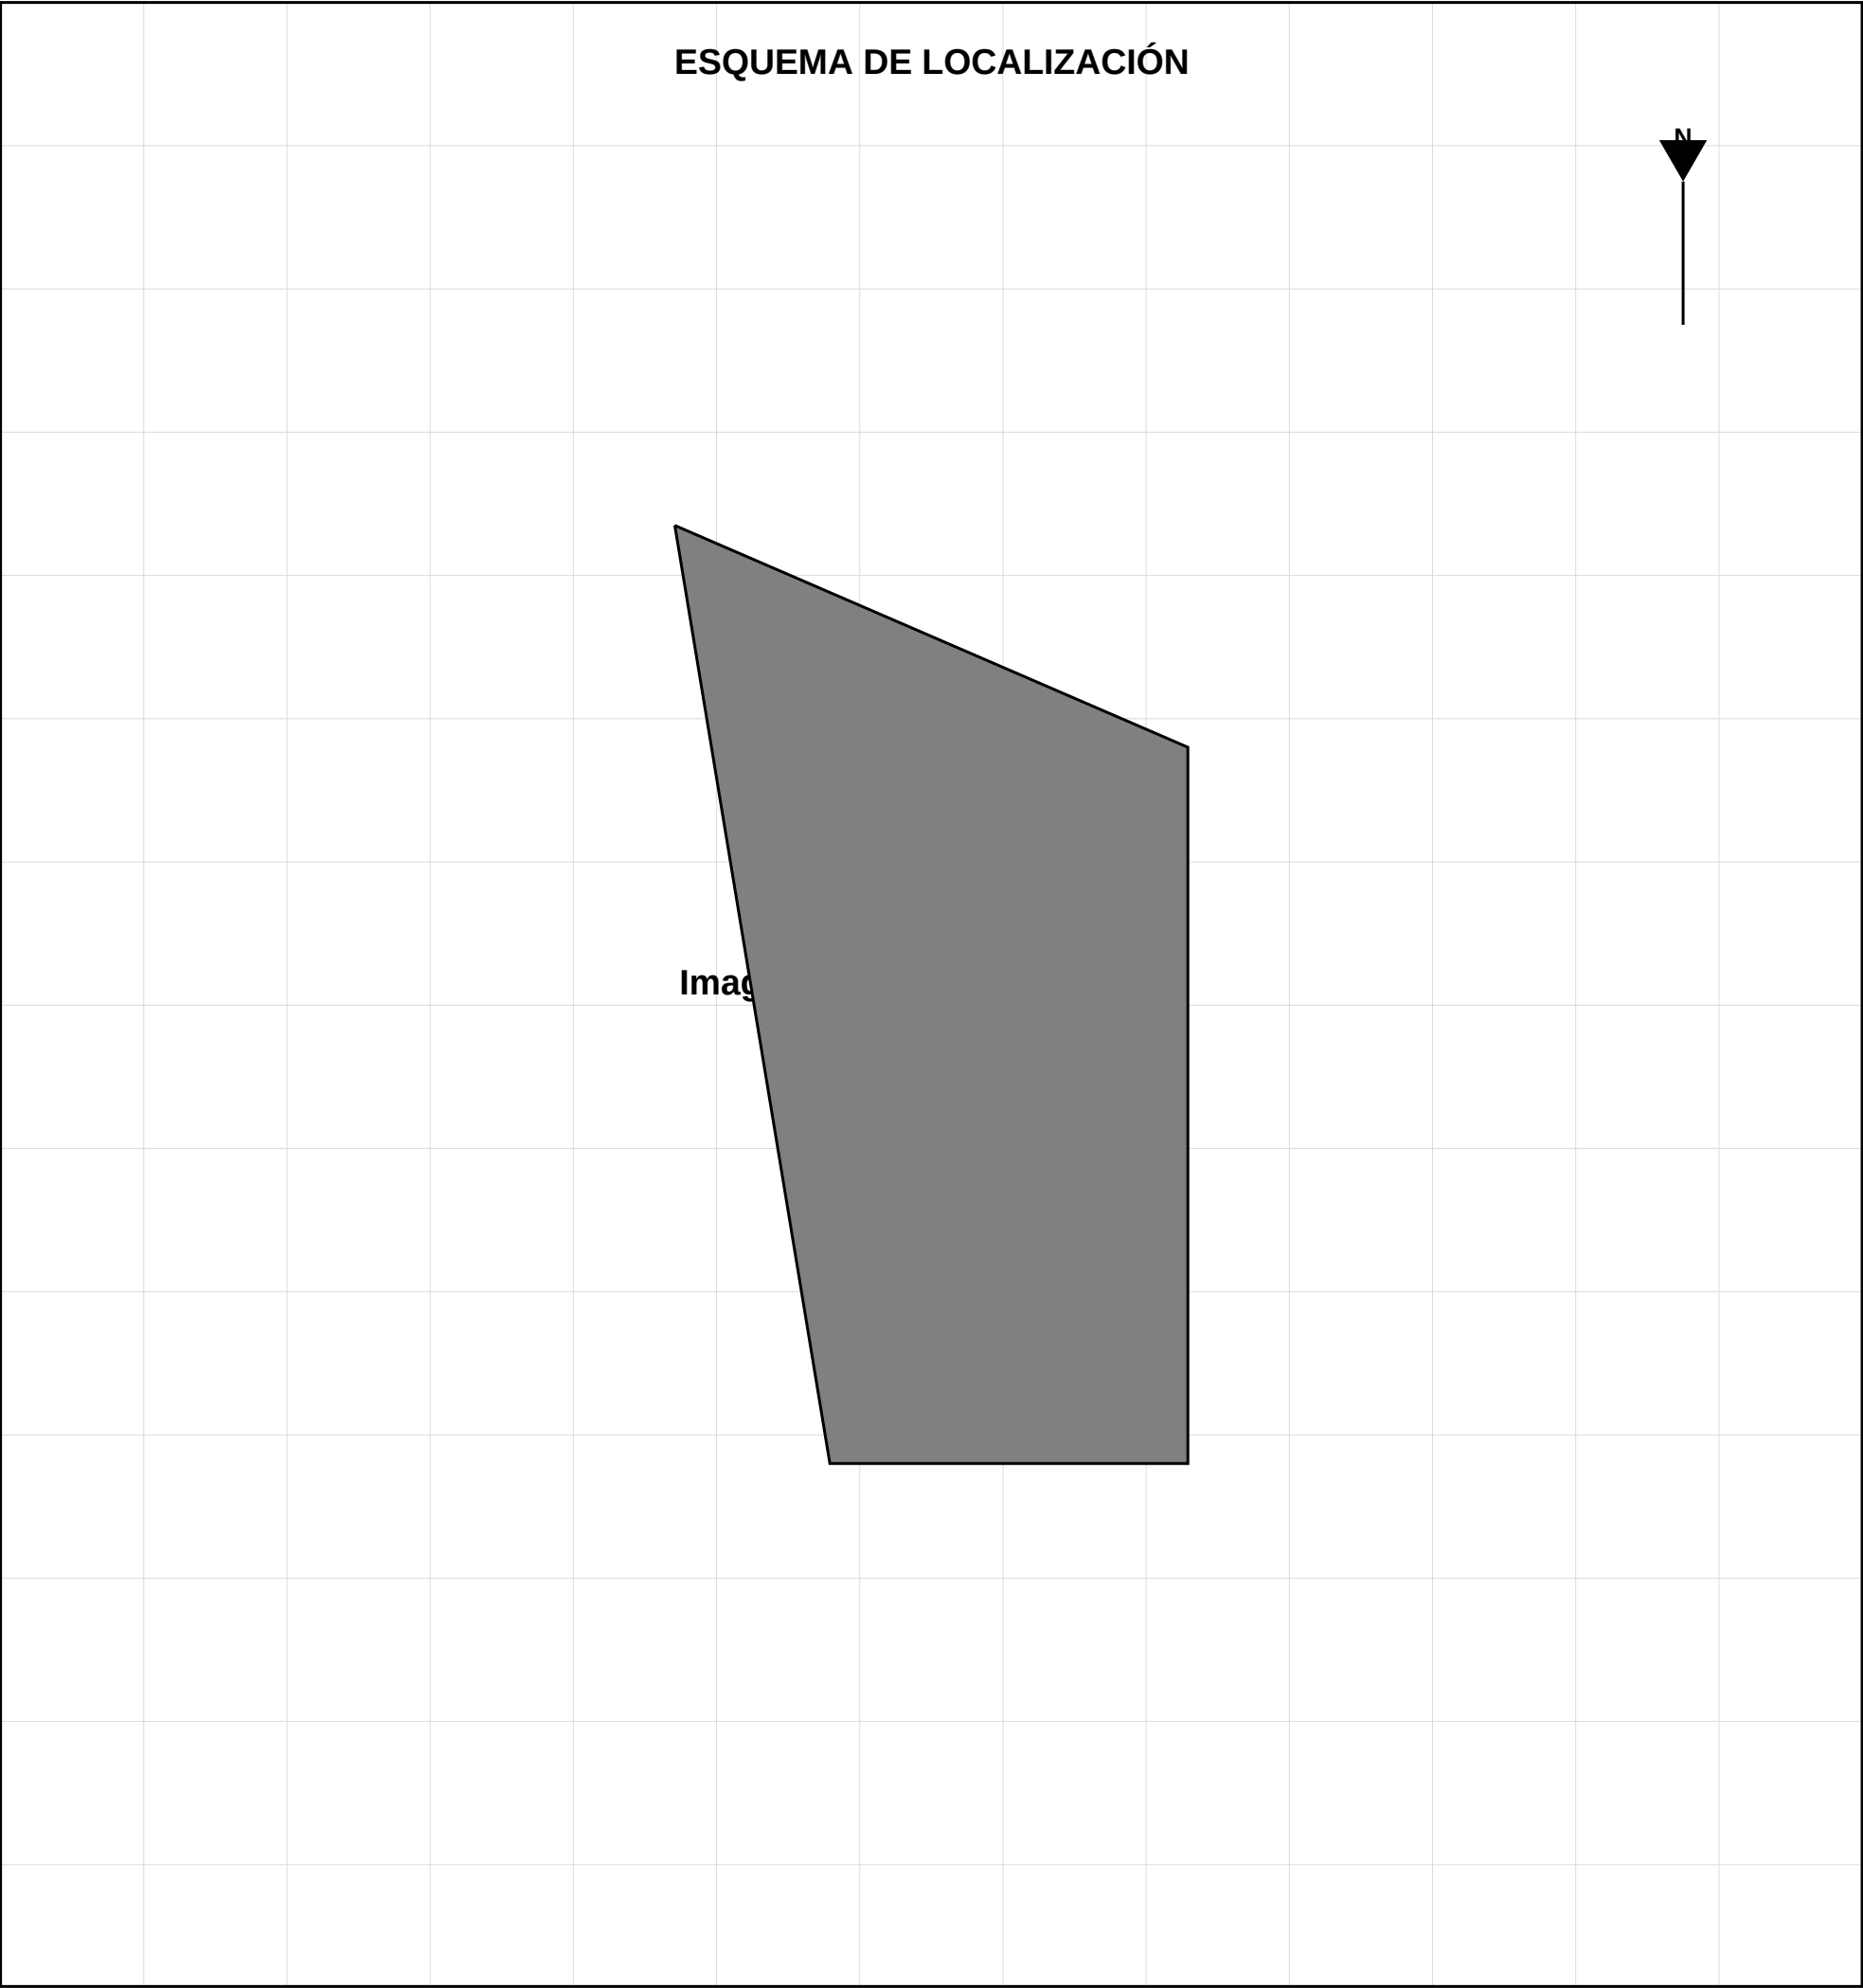

| DATOS GENERALES |                                |
|-----------------|--------------------------------|
| Departamento:   | Lima                           |
| Provincia:      | Lima                           |
| Distrito:       | Habilitación Urbana Los Cedros |
| Manzana:        | C                              |
| Lote:           | 14                             |
| Área:           | 200.00 m²                      |

| COORDENADAS (CENTROIDE) |                               |
|-------------------------|-------------------------------|
| UTM WGS84:              | E: 284503.92 N: 8670091.55    |
| GEOGRÁFICAS:            | Lat: -76.97940 Lng: -12.02332 |

| MACRO LOCALIZACIÓN     |
|------------------------|
| VISTA GENERAL PROYECTO |

|                         |  |               |
|-------------------------|--|---------------|
| PLANO DE UBICACIÓN      |  |               |
| PROPIETARIO: ---        |  |               |
| UBICACIÓN: Mz. C Lt. 14 |  |               |
| FECHA: 26/1/2026        |  | ESCALA: 1/200 |