

PLANOS PRO

Sistema Profesional de Generación de Planos

PROYECTO:

Etapas 1

LOTE:

MZ-C-Lote14

DOCUMENTO: MEMORIA DESCRIPTIVA

FECHA: 26 de enero de 2026

MEMORIA DESCRIPTIVA

I. IDENTIFICACIÓN DEL PREDIO

Código Catastral:	MZ-C-Lote14
Nombre del Lote:	MZ-C-Lote14
Manzana:	MZ
Etapas:	Etapas 1
Número de Lote:	Lote14
Estado:	LIBRE

II. UBICACIÓN GEOGRÁFICA

Sistema de Coordenadas:	UTM WGS84 - Zona 18S
Datum:	WGS84
Hemisferio:	Sur

III. CARACTERÍSTICAS MÉTRICAS DEL PREDIO

ÁREA TOTAL:	673.79 m²
PERÍMETRO TOTAL:	133.40 ml
Frente:	10.00 ml
Fondo:	10.00 ml
Lado Derecho:	20.00 ml
Lado Izquierdo:	20.00 ml

IV. LINDEROS Y COLINDANCIAS

El predio tiene los siguientes linderos y colindancias:

PLANOS PRO

Sistema Profesional de Generación de Planos

PROYECTO:

Etapa 1

LOTE:

MZ-C-Lote14

DOCUMENTO: MEMORIA DESCRIPTIVA

FECHA: 26 de enero de 2026

Por el FRENTE: Con calle "Av. Los Alamos"

Por el FONDO: Con lote "Lote 05"

Por el IZQUIERDA: Con lote "Lote 13"

Por el DERECHA: Con lote "Lote 15"

V. CUADRO DE DATOS TÉCNICOS - COORDENADAS UTM

VÉRTICE	LADO	ESTE (m)	NORTE (m)
V1	V1-V2	284457.94	8670112.71
V2	V2-V3	284487.61	8670113.67
V3	V3-V4	284510.00	8670080.00
V4	V4-V1	284500.00	8670080.00

PROPIETARIO

Firma y Sello


PROFESIONAL RESPONSABLE

Ing. Civil / Arquitecto

Este documento ha sido generado automáticamente por el sistema PLANOS PRO

Código de Verificación: MZ-C-Lote14-MKVRGUPR


PLANO PERIMÉTRICO

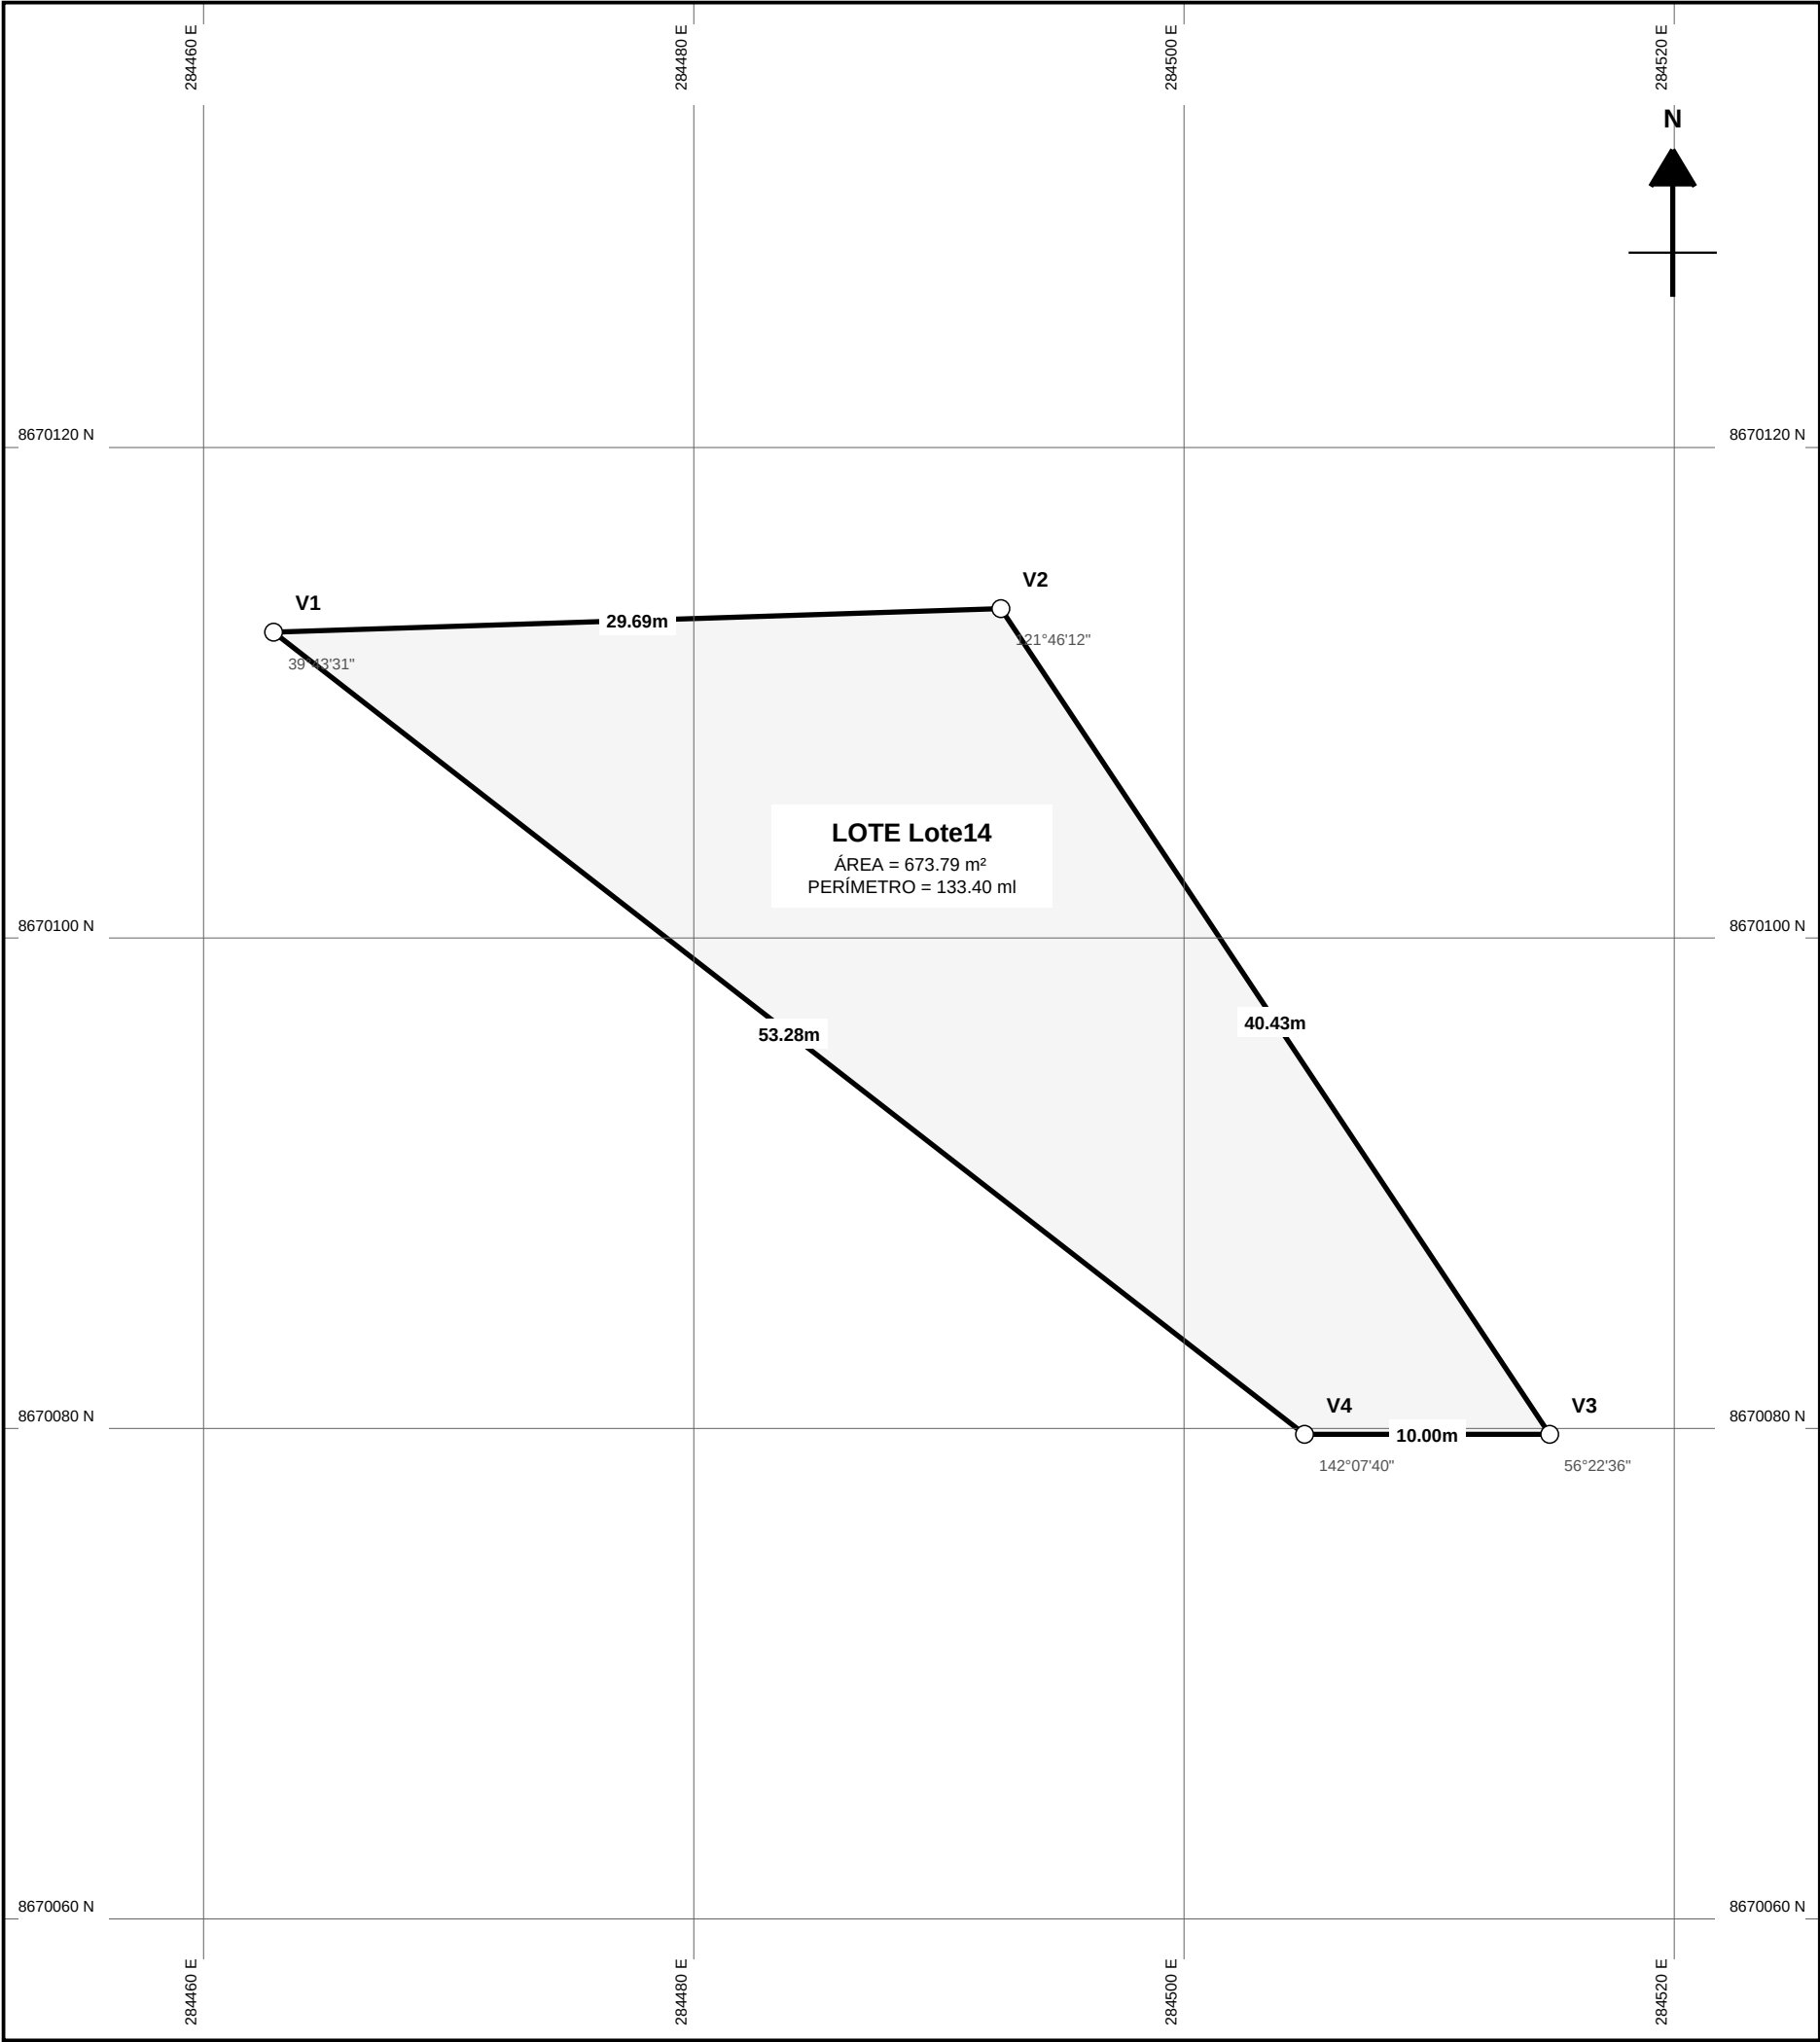

PLANO DE UBICACIÓN
ESCALA 1/1000

CUADRO DE DATOS TÉCNICOS - UTM WGS84					
VÉRTICE	LADO	DIST (m)	ÁNGULO INT.	ESTE (X)	NORTE (Y)
V-1	V1-V2	29.69	39°43'31"	284457.940	8670112.710
V-2	V2-V3	40.43	121°46'12"	284487.610	8670113.670
V-3	V3-V4	10.00	56°22'36"	284510.000	8670080.000
V-4	V4-V1	53.28	142°07'40"	284500.000	8670080.000

PLANO
PERIMÉTRICO

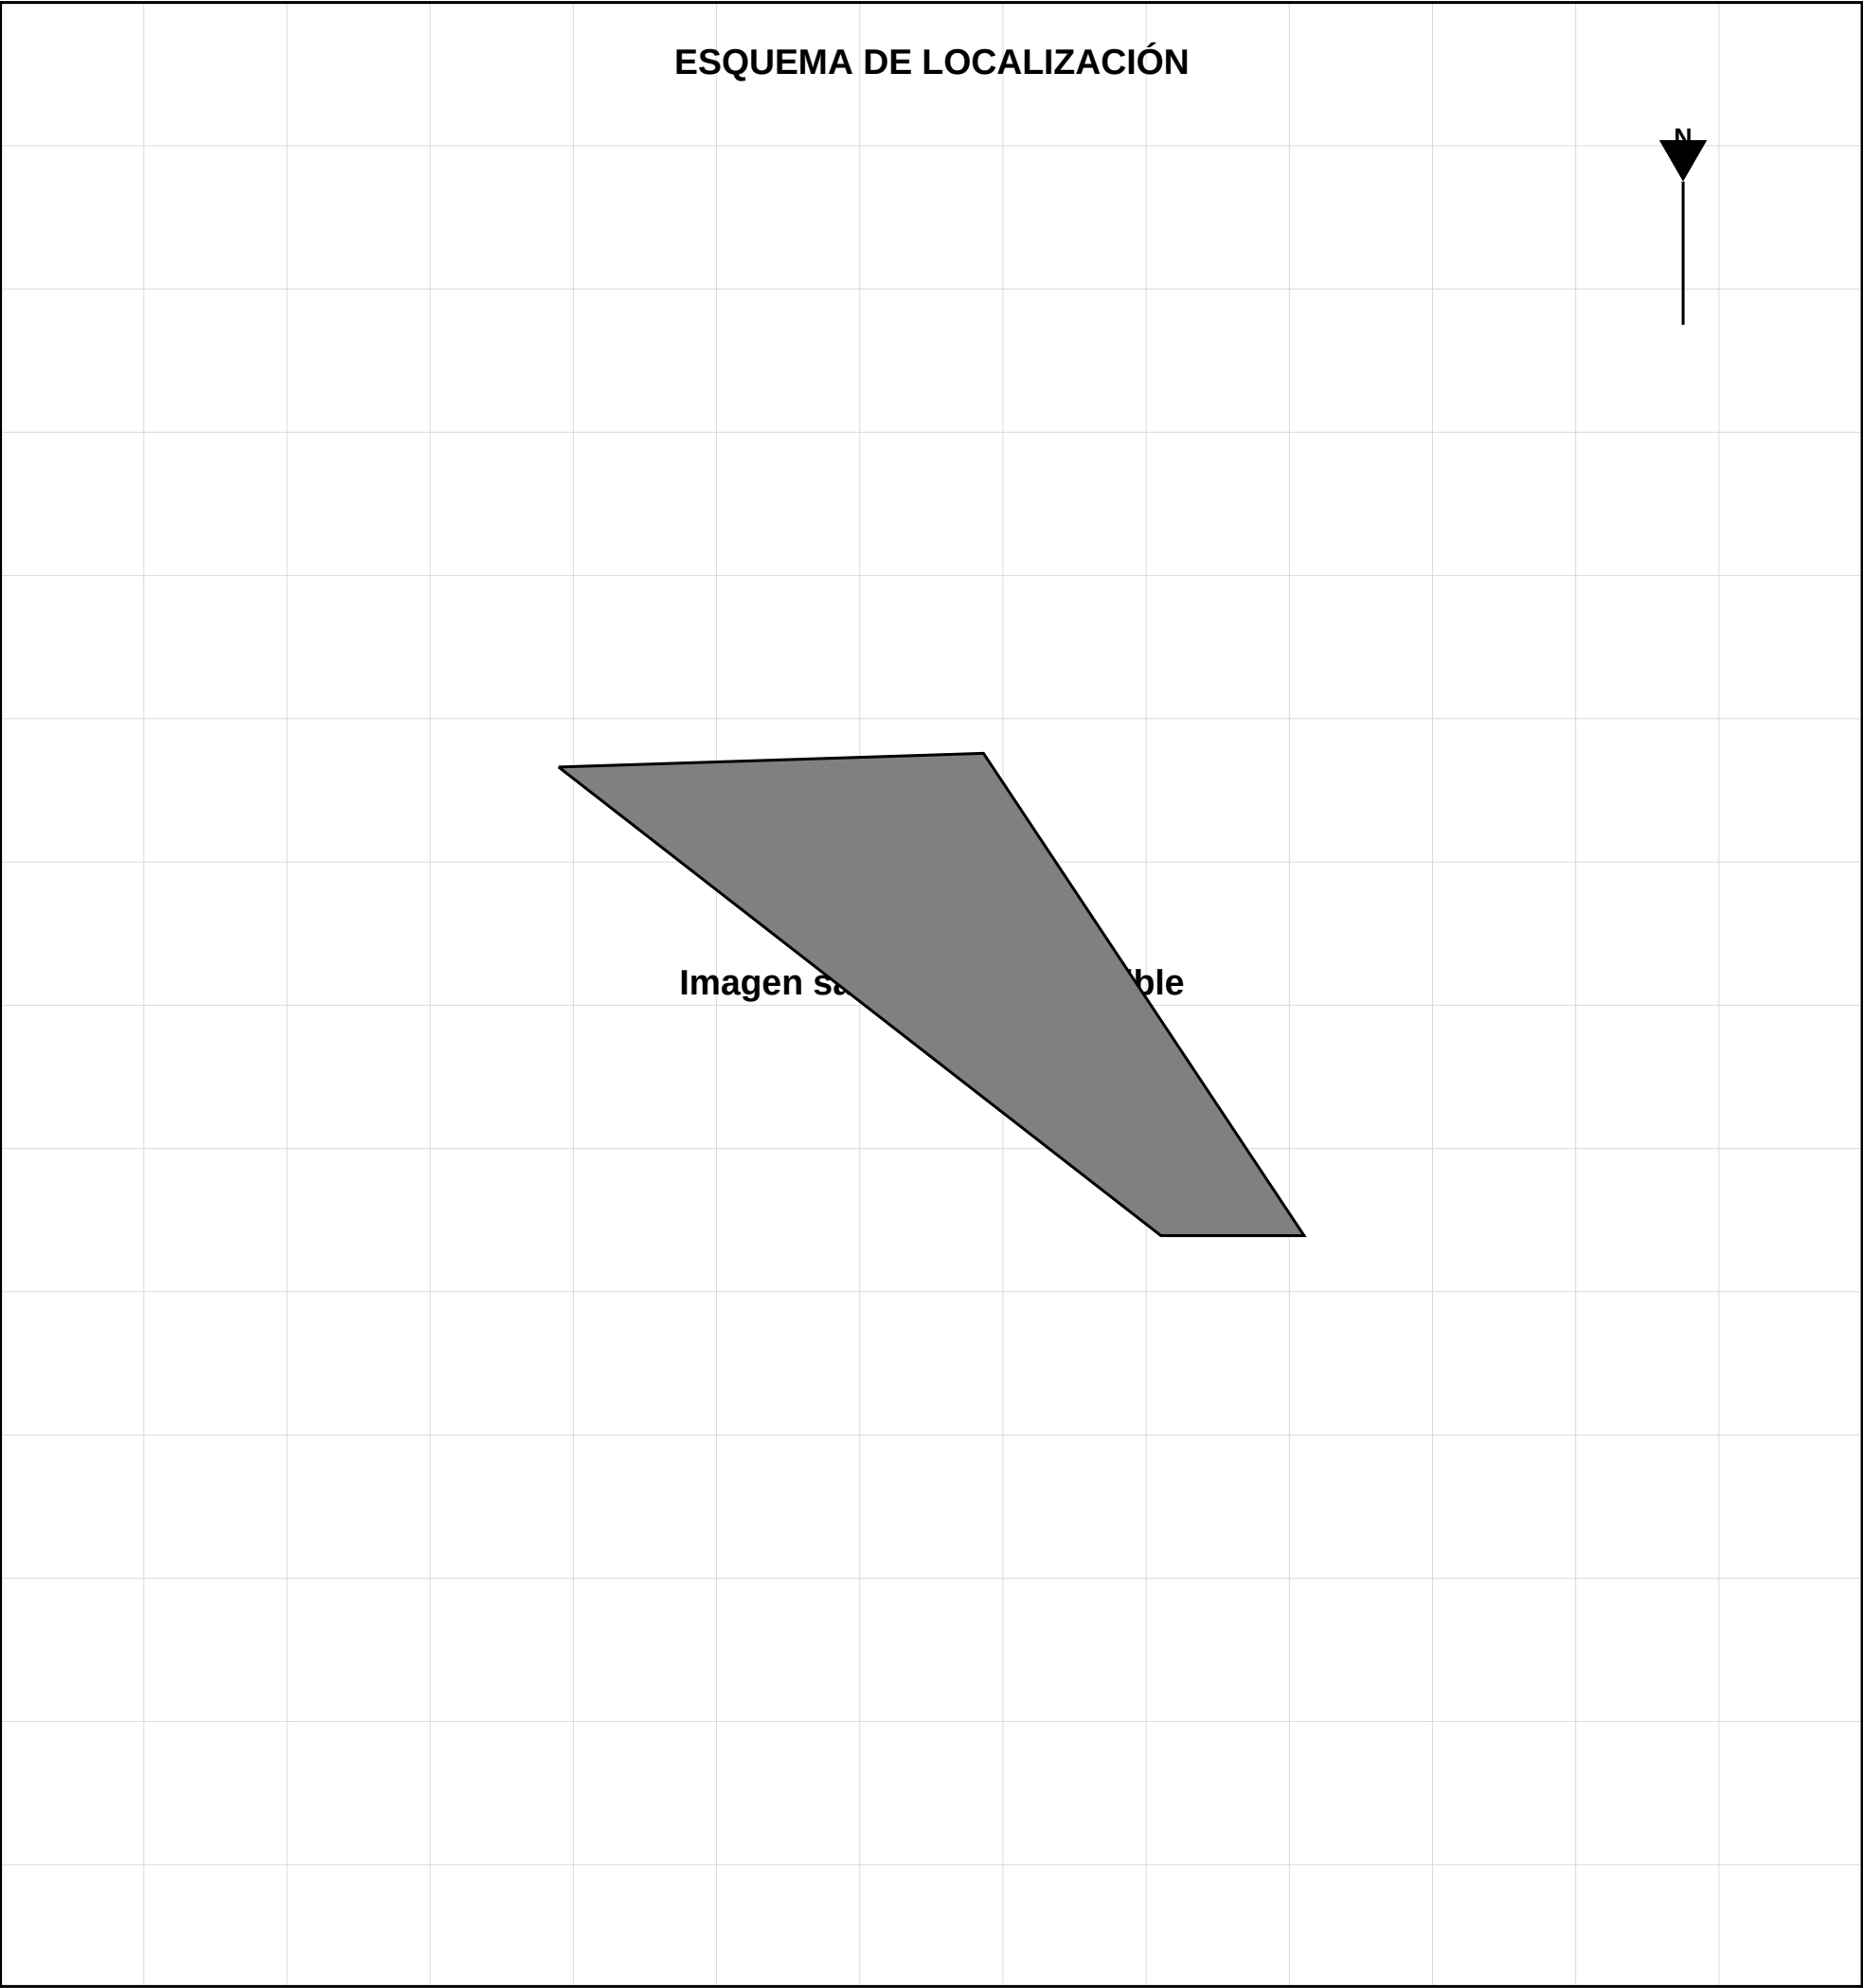

DATOS GENERALES	
Departamento:	Lima
Provincia:	Lima
Distrito:	Etapa 1
Manzana:	MZ
Lote:	Lote14
Área:	673.79 m²

COORDENADAS (CENTROIDE)	
UTM WGS84:	E: 284488.89 N: 8670096.60
GEOGRÁFICAS:	Lat: -76.97953 Lng: -12.02328

MACRO LOCALIZACIÓN
VISTA GENERAL PROYECTO

PLANO DE UBICACIÓN		
PROPIETARIO: ---		
UBICACIÓN: Mz. MZ Lt. Lote14		
FECHA: 26/1/2026		ESCALA: 1/500