

PLANOS PRO

Sistema Profesional de Generación de Planos

PROYECTO:

Etapas 1

LOTE:

MZ-C-Lote14

DOCUMENTO: MEMORIA DESCRIPTIVA

FECHA: 26 de enero de 2026

MEMORIA DESCRIPTIVA

I. IDENTIFICACIÓN DEL PREDIO

Código Catastral:	MZ-C-Lote14
Nombre del Lote:	MZ-C-Lote14
Manzana:	MZ
Etapas:	Etapas 1
Número de Lote:	Lote14
Estado:	LIBRE

II. UBICACIÓN GEOGRÁFICA

Sistema de Coordenadas:	UTM WGS84 - Zona 18S
Datum:	WGS84
Hemisferio:	Sur

III. CARACTERÍSTICAS MÉTRICAS DEL PREDIO

ÁREA TOTAL:	4101.05 m ²
PERÍMETRO TOTAL:	422.70 ml
Frente:	10.00 ml
Fondo:	10.00 ml
Lado Derecho:	20.00 ml
Lado Izquierdo:	20.00 ml

IV. LINDEROS Y COLINDANCIAS

El predio tiene los siguientes linderos y colindancias:

PLANOS PRO

Sistema Profesional de Generación de Planos

PROYECTO:

Etapas 1

LOTE:

MZ-C-Lote14

DOCUMENTO: MEMORIA DESCRIPTIVA

FECHA: 26 de enero de 2026

Por el FRENTE: Con calle "Av. Los Alamos"

Por el FONDO: Con lote "Lote 05"

Por el IZQUIERDA: Con lote "Lote 13"

Por el DERECHA: Con lote "Lote 15"

V. CUADRO DE DATOS TÉCNICOS - COORDENADAS UTM

VÉRTICE	LADO	ESTE (m)	NORTE (m)
V1	V1-V2	284489.04	8670099.83
V2	V2-V3	284515.64	8670195.63
V3	V3-V4	284591.09	8670092.68
V4	V4-V5	284550.18	8670115.52
V5	V5-V6	284532.80	8670070.18
V6	V6-V1	284528.37	8670124.04

PROPIETARIO

Firma y Sello


PROFESIONAL RESPONSABLE

Ing. Civil / Arquitecto

Este documento ha sido generado automáticamente por el sistema PLANOS PRO

Código de Verificación: MZ-C-Lote14-MKVRKNA1


PLANO PERIMÉTRICO

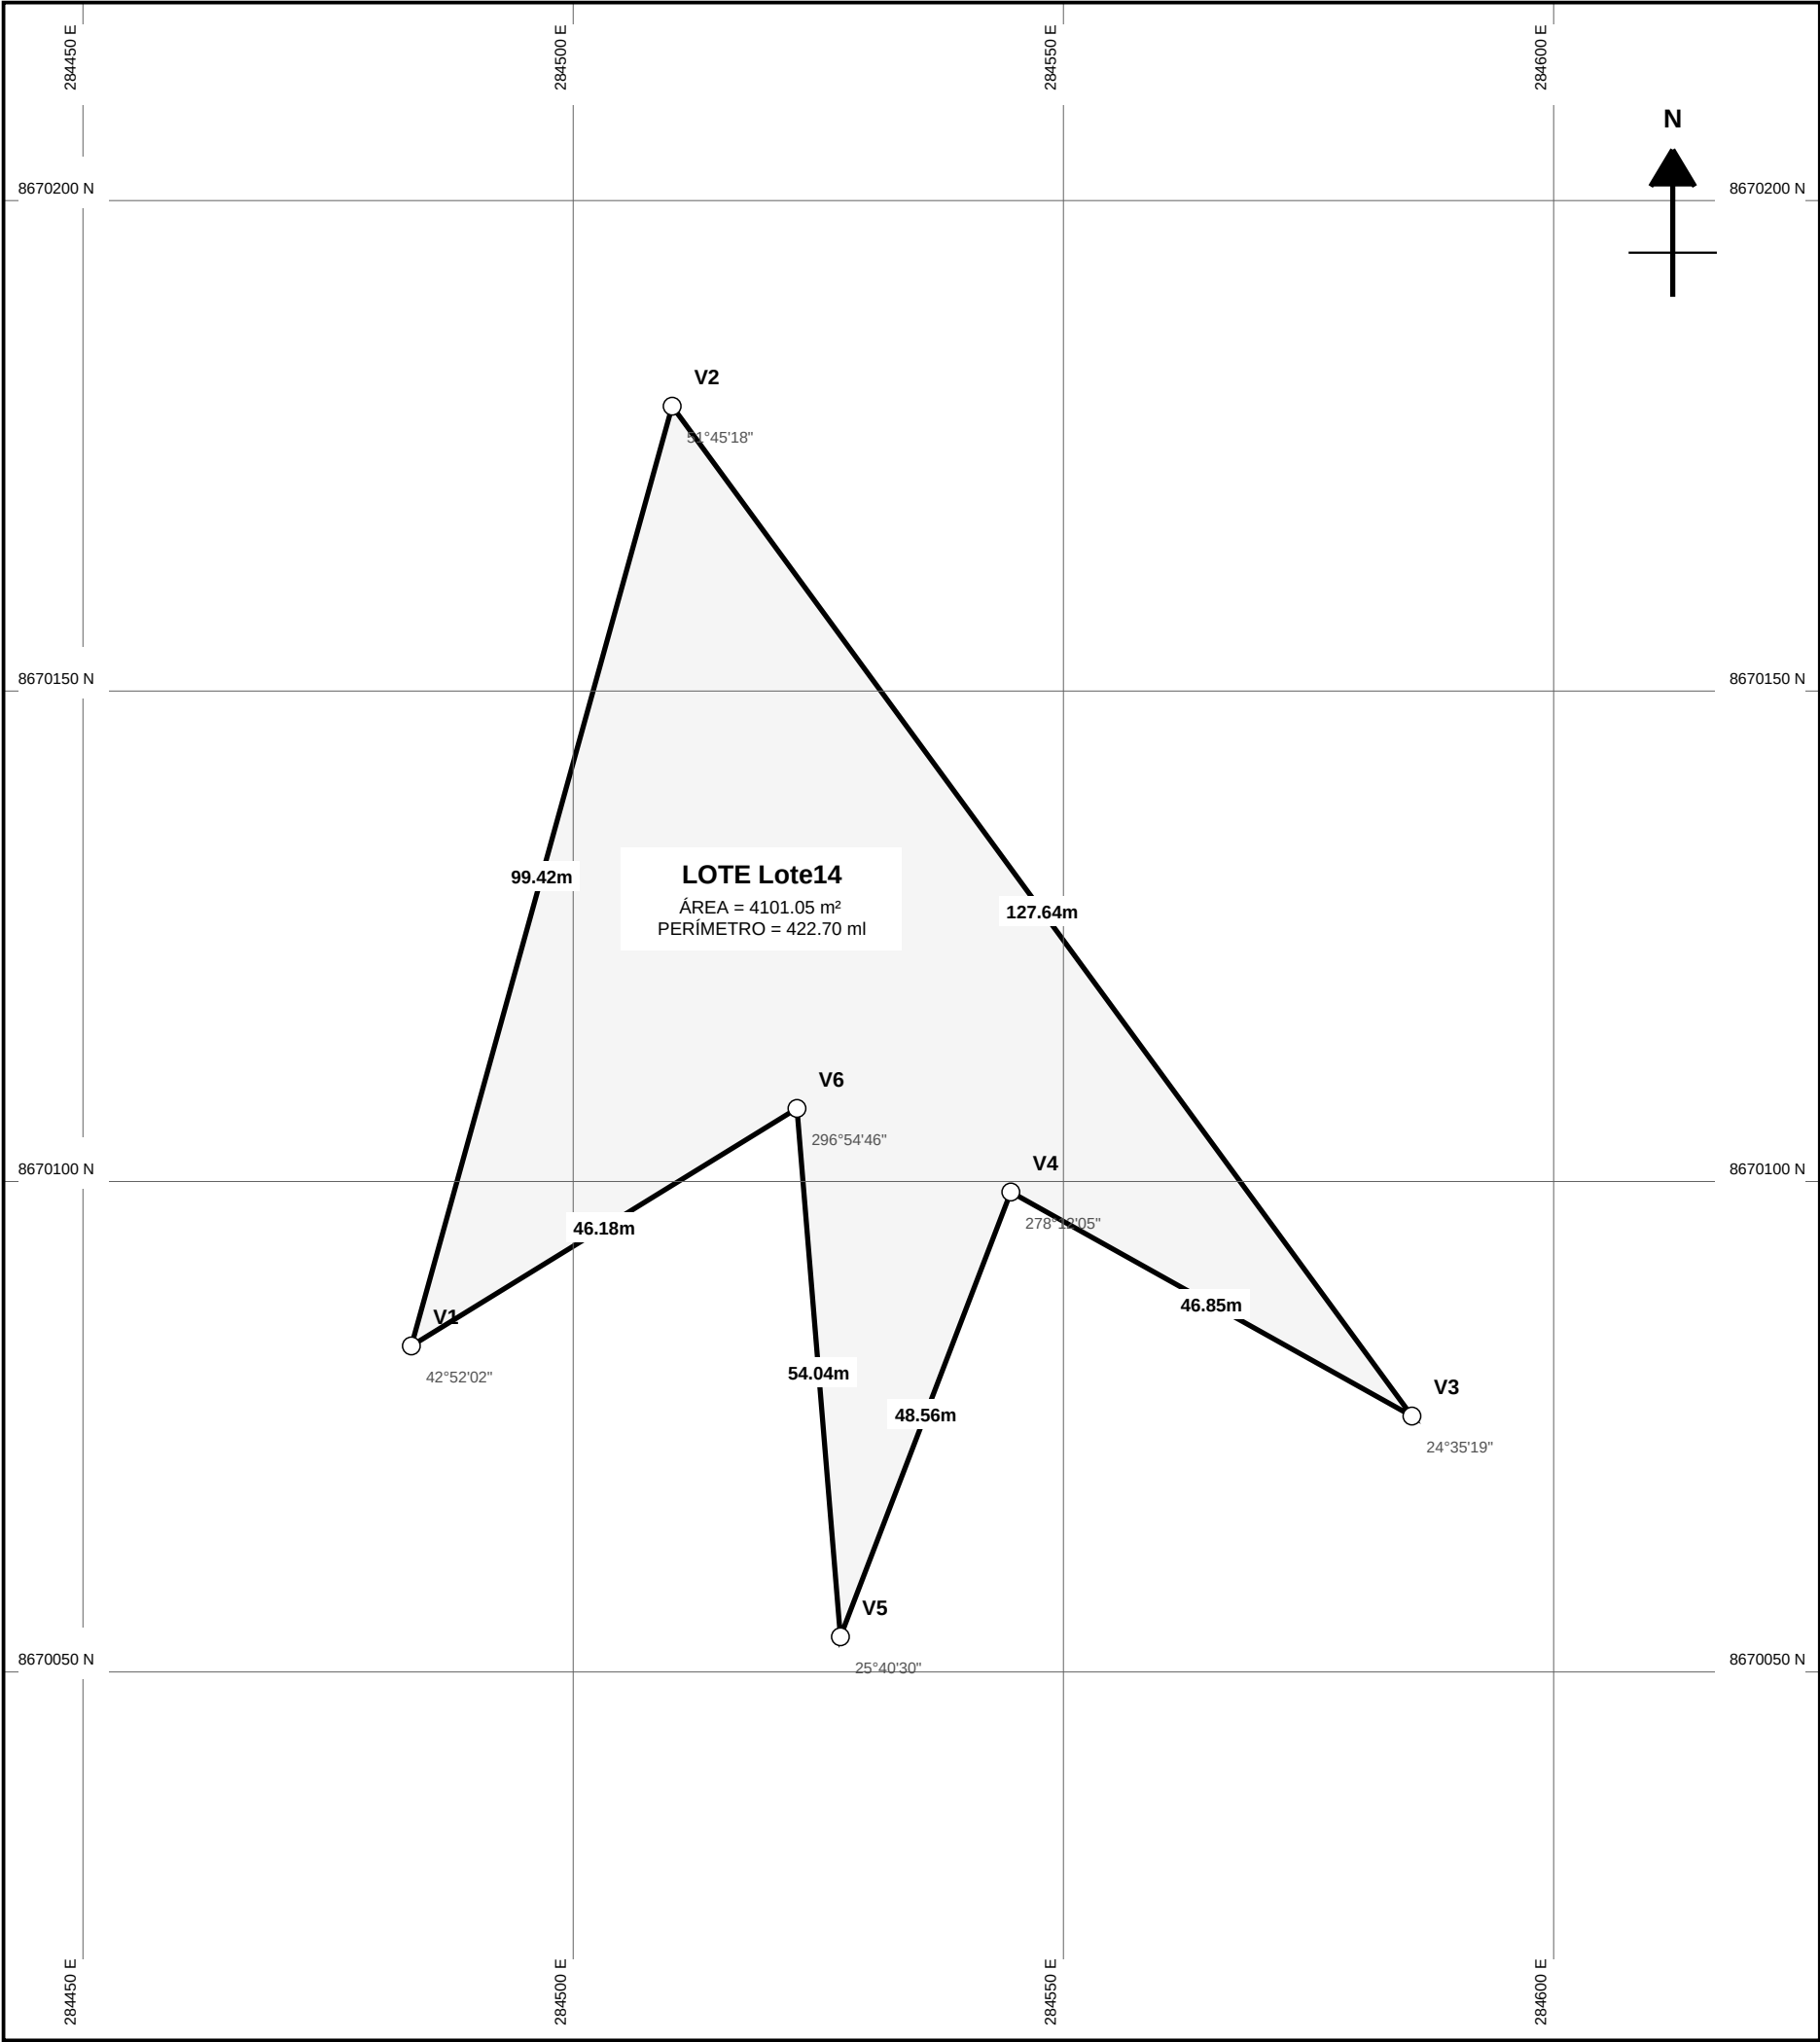

PLANO DE UBICACIÓN
ESCALA 1/1000

CUADRO DE DATOS TÉCNICOS - UTM WGS84					
VÉRTICE	LADO	DIST (m)	ÁNGULO INT.	ESTE (X)	NORTE (Y)
V-1	V1-V2	99.42	42°52'02"	284489.040	8670099.830
V-2	V2-V3	127.64	51°45'18"	284515.640	8670195.630
V-3	V3-V4	46.85	24°35'19"	284591.090	8670092.680
V-4	V4-V5	48.56	278°12'05"	284550.180	8670115.520
V-5	V5-V6	54.04	25°40'30"	284532.800	8670070.180
V-6	V6-V1	46.18	296°54'46"	284528.370	8670124.040

PLANO
PERIMÉTRICO

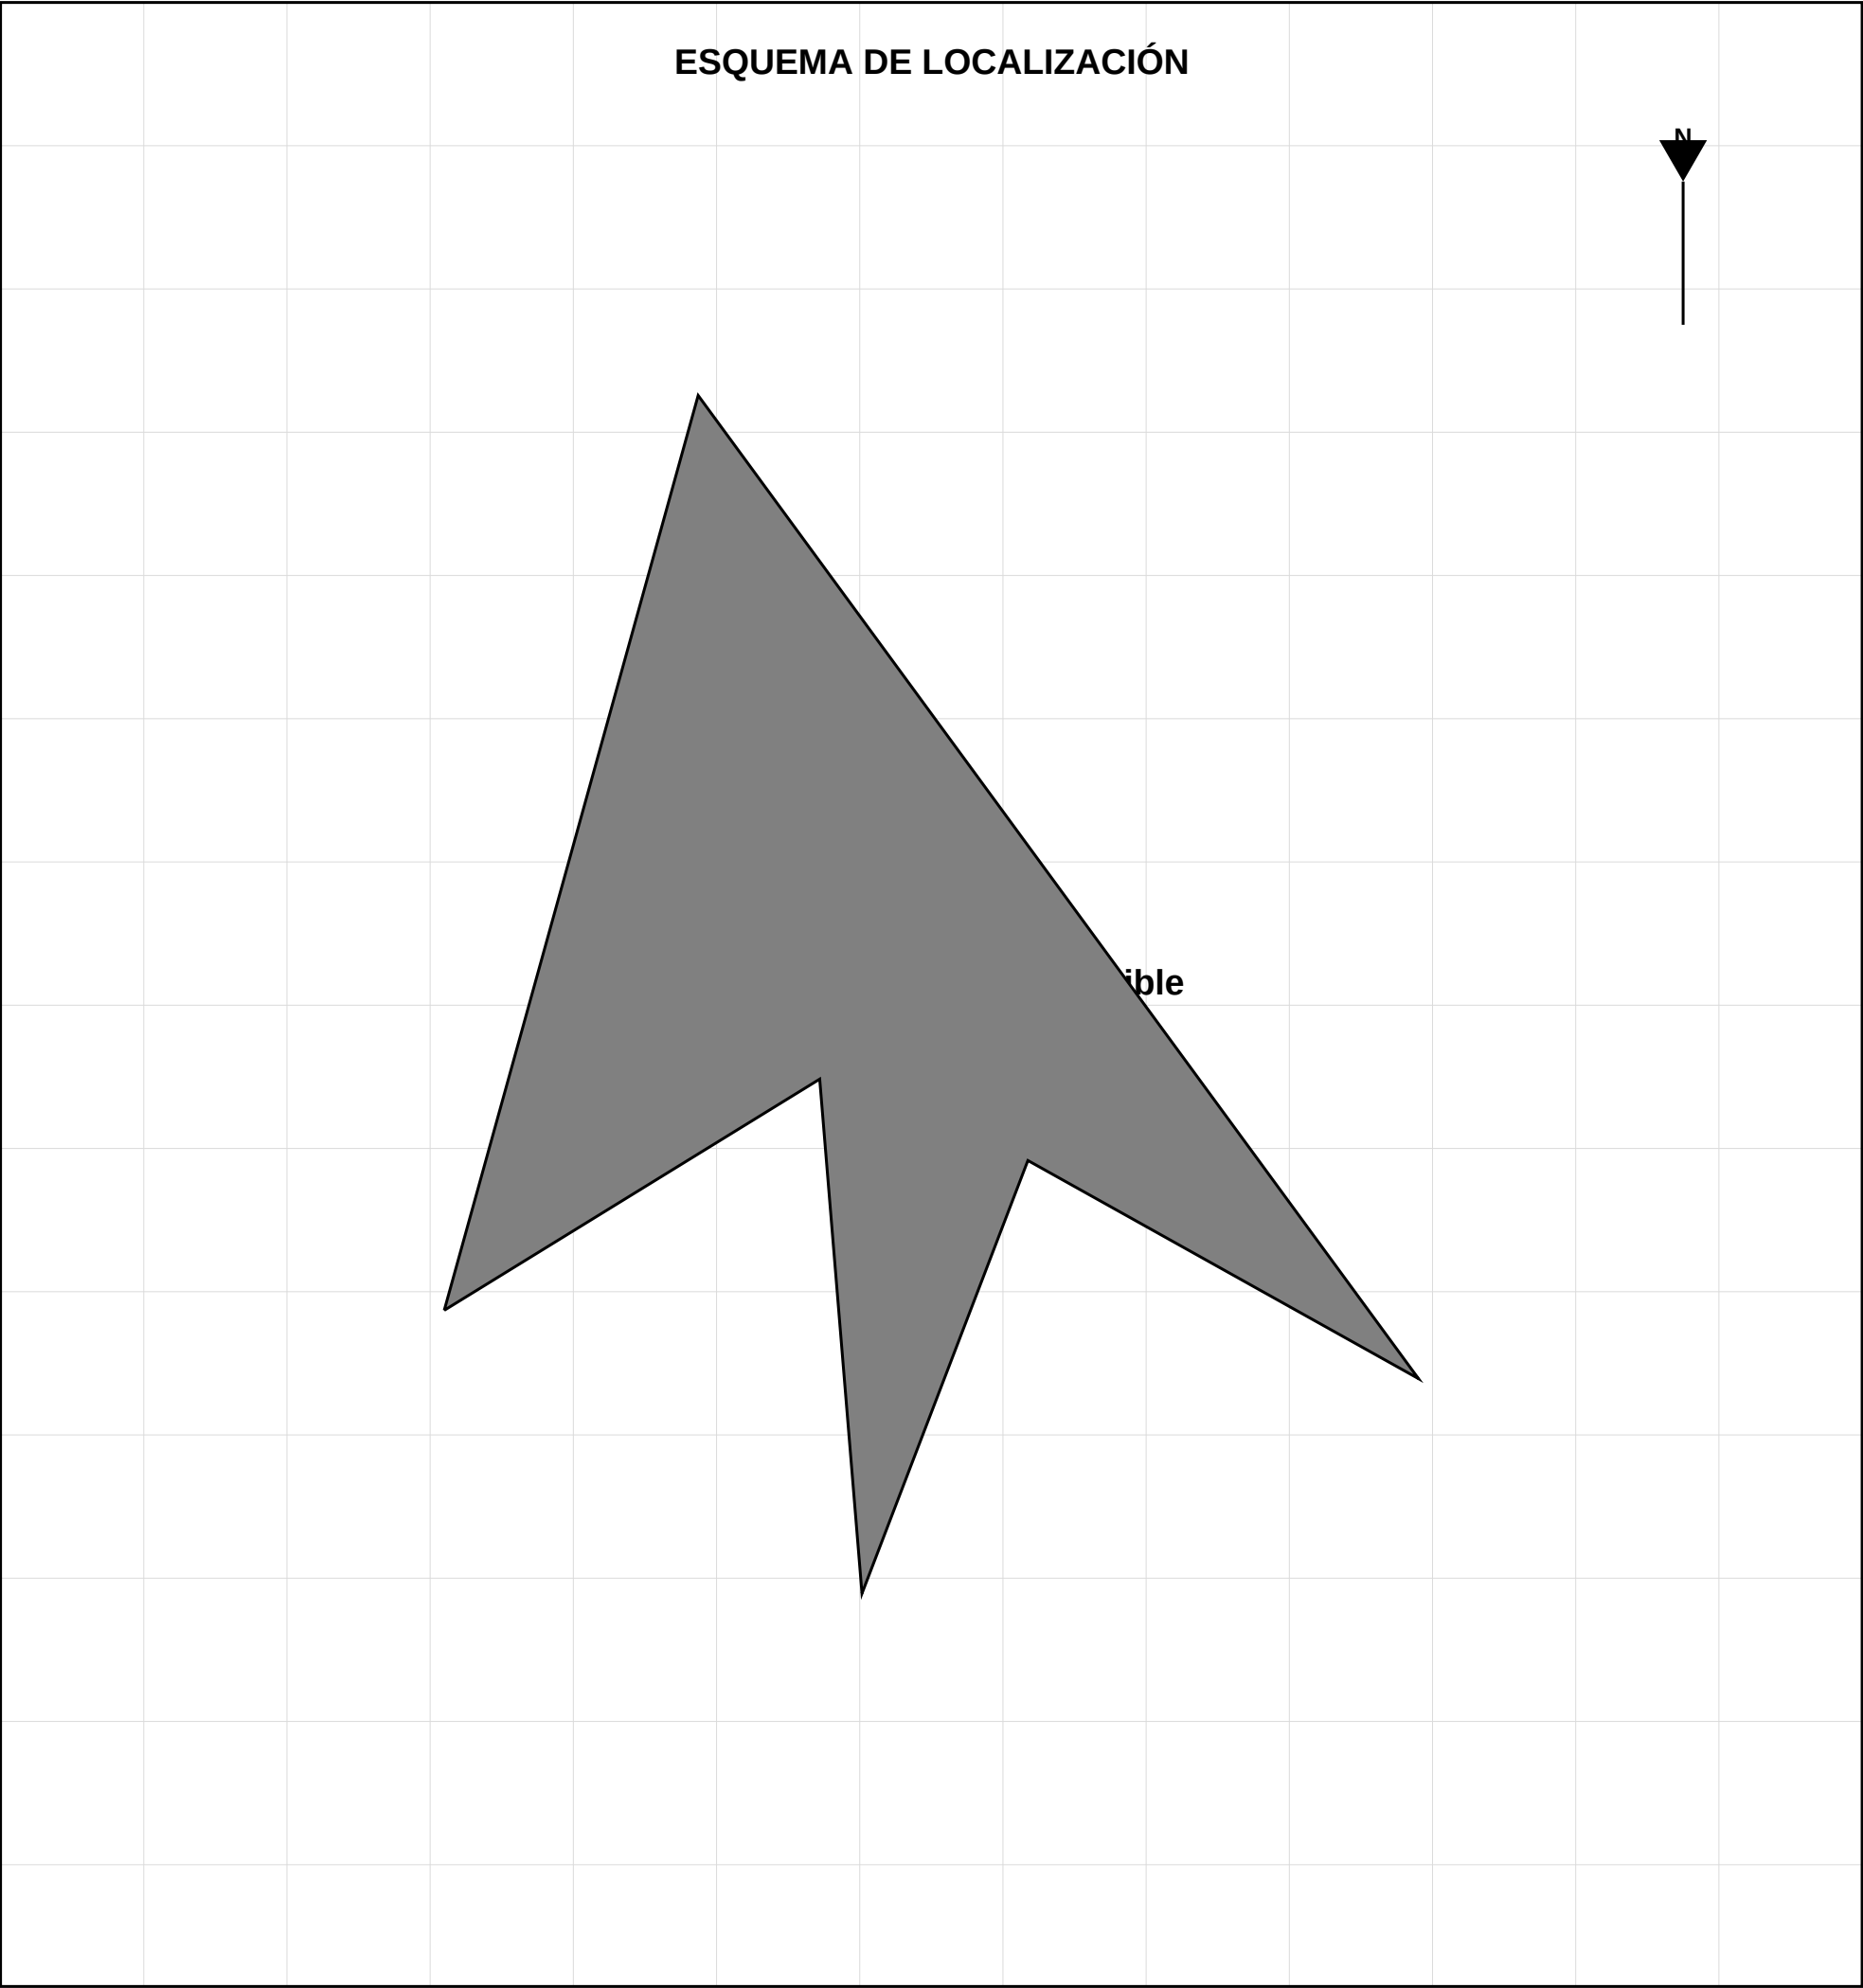

DATOS GENERALES	
Departamento:	Lima
Provincia:	Lima
Distrito:	Etapa 1
Manzana:	MZ
Lote:	Lote14
Área:	4101.05 m²

COORDENADAS (CENTROIDE)	
UTM WGS84:	E: 284534.52 N: 8670116.31
GEOGRÁFICAS:	Lat: -76.97911 Lng: -12.02310

MACRO LOCALIZACIÓN
VISTA GENERAL PROYECTO

PLANO DE UBICACIÓN		
PROPIETARIO: ---		
UBICACIÓN: Mz. MZ Lt. Lote14		
FECHA: 26/1/2026		ESCALA: 1/750