

TERRA LIMA

Desarrollo Inmobiliario

PROYECTO: TERRA LIMA
DOCUMENTO: MEMORIA DESCRIPTIVA
CÓDIGO: E01MZC024P
FECHA: 27 de enero de 2026

MEMORIA DESCRIPTIVA

I. GENERALIDADES

La presente Memoria Descriptiva tiene por objeto describir técnica y legalmente el lote de terreno urbano, delimitando sus linderos y medidas perimétricas, así como su ubicación y área, el cual forma parte del proyecto inmobiliario "TERRA LIMA".

II. IDENTIFICACIÓN Y UBICACIÓN DEL PREDIO

PROYECTO: TERRA LIMA
ETAPA: Etapa 1
MANZANA: C
LOTE: 24
CÓDIGO INTERNO: E01MZC024P
DEPARTAMENTO: Lima
PROVINCIA: Lima
DISTRITO: San Juan de Lurigancho
DIRECCIÓN: Av. Los Alamos S/N

III. ÁREA Y PERÍMETRO

ÁREA DEL TERRENO: 200.00 m²
PERÍMETRO TOTAL: 60.00 ml

TERRA LIMA

Desarrollo Inmobiliario

PROYECTO: TERRA LIMA
DOCUMENTO: MEMORIA DESCRIPTIVA
CÓDIGO: E01MZC024P
FECHA: 27 de enero de 2026

IV. LINDEROS Y MEDIDAS PERIMÉTRICAS

El inmueble se encuentra delimitado de la siguiente manera:

POR EL FRENTE: Colinda con calle "Av. Los Alamos", con una línea recta de 10.00 ml.

POR EL FONDO: Colinda con el lote "Lote 05", propiedad de Juan Pérez García, con una línea recta de 10.00 ml.

POR EL IZQUIERDA: Colinda con el lote "Lote 13", propiedad de María González, con una línea recta de 20.00 ml.

POR EL DERECHA: Colinda con el lote "Lote 15", propiedad de Pedro Sánchez, con una línea recta de 20.00 ml.


V. COORDENADAS UTM (WGS-84)

VÉRTICE	LADO	ESTE (X)	NORTE (Y)
V-1	V1-V2	284500.000	8670100.000
V-2	V2-V3	284510.000	8670100.000
V-3	V3-V4	284510.000	8670080.000
V-4	V4-V1	284500.000	8670080.000

PROFESIONAL RESPONSABLE

Ingeniero Civil / Arquitecto

PLANO PERIMÉTRICO

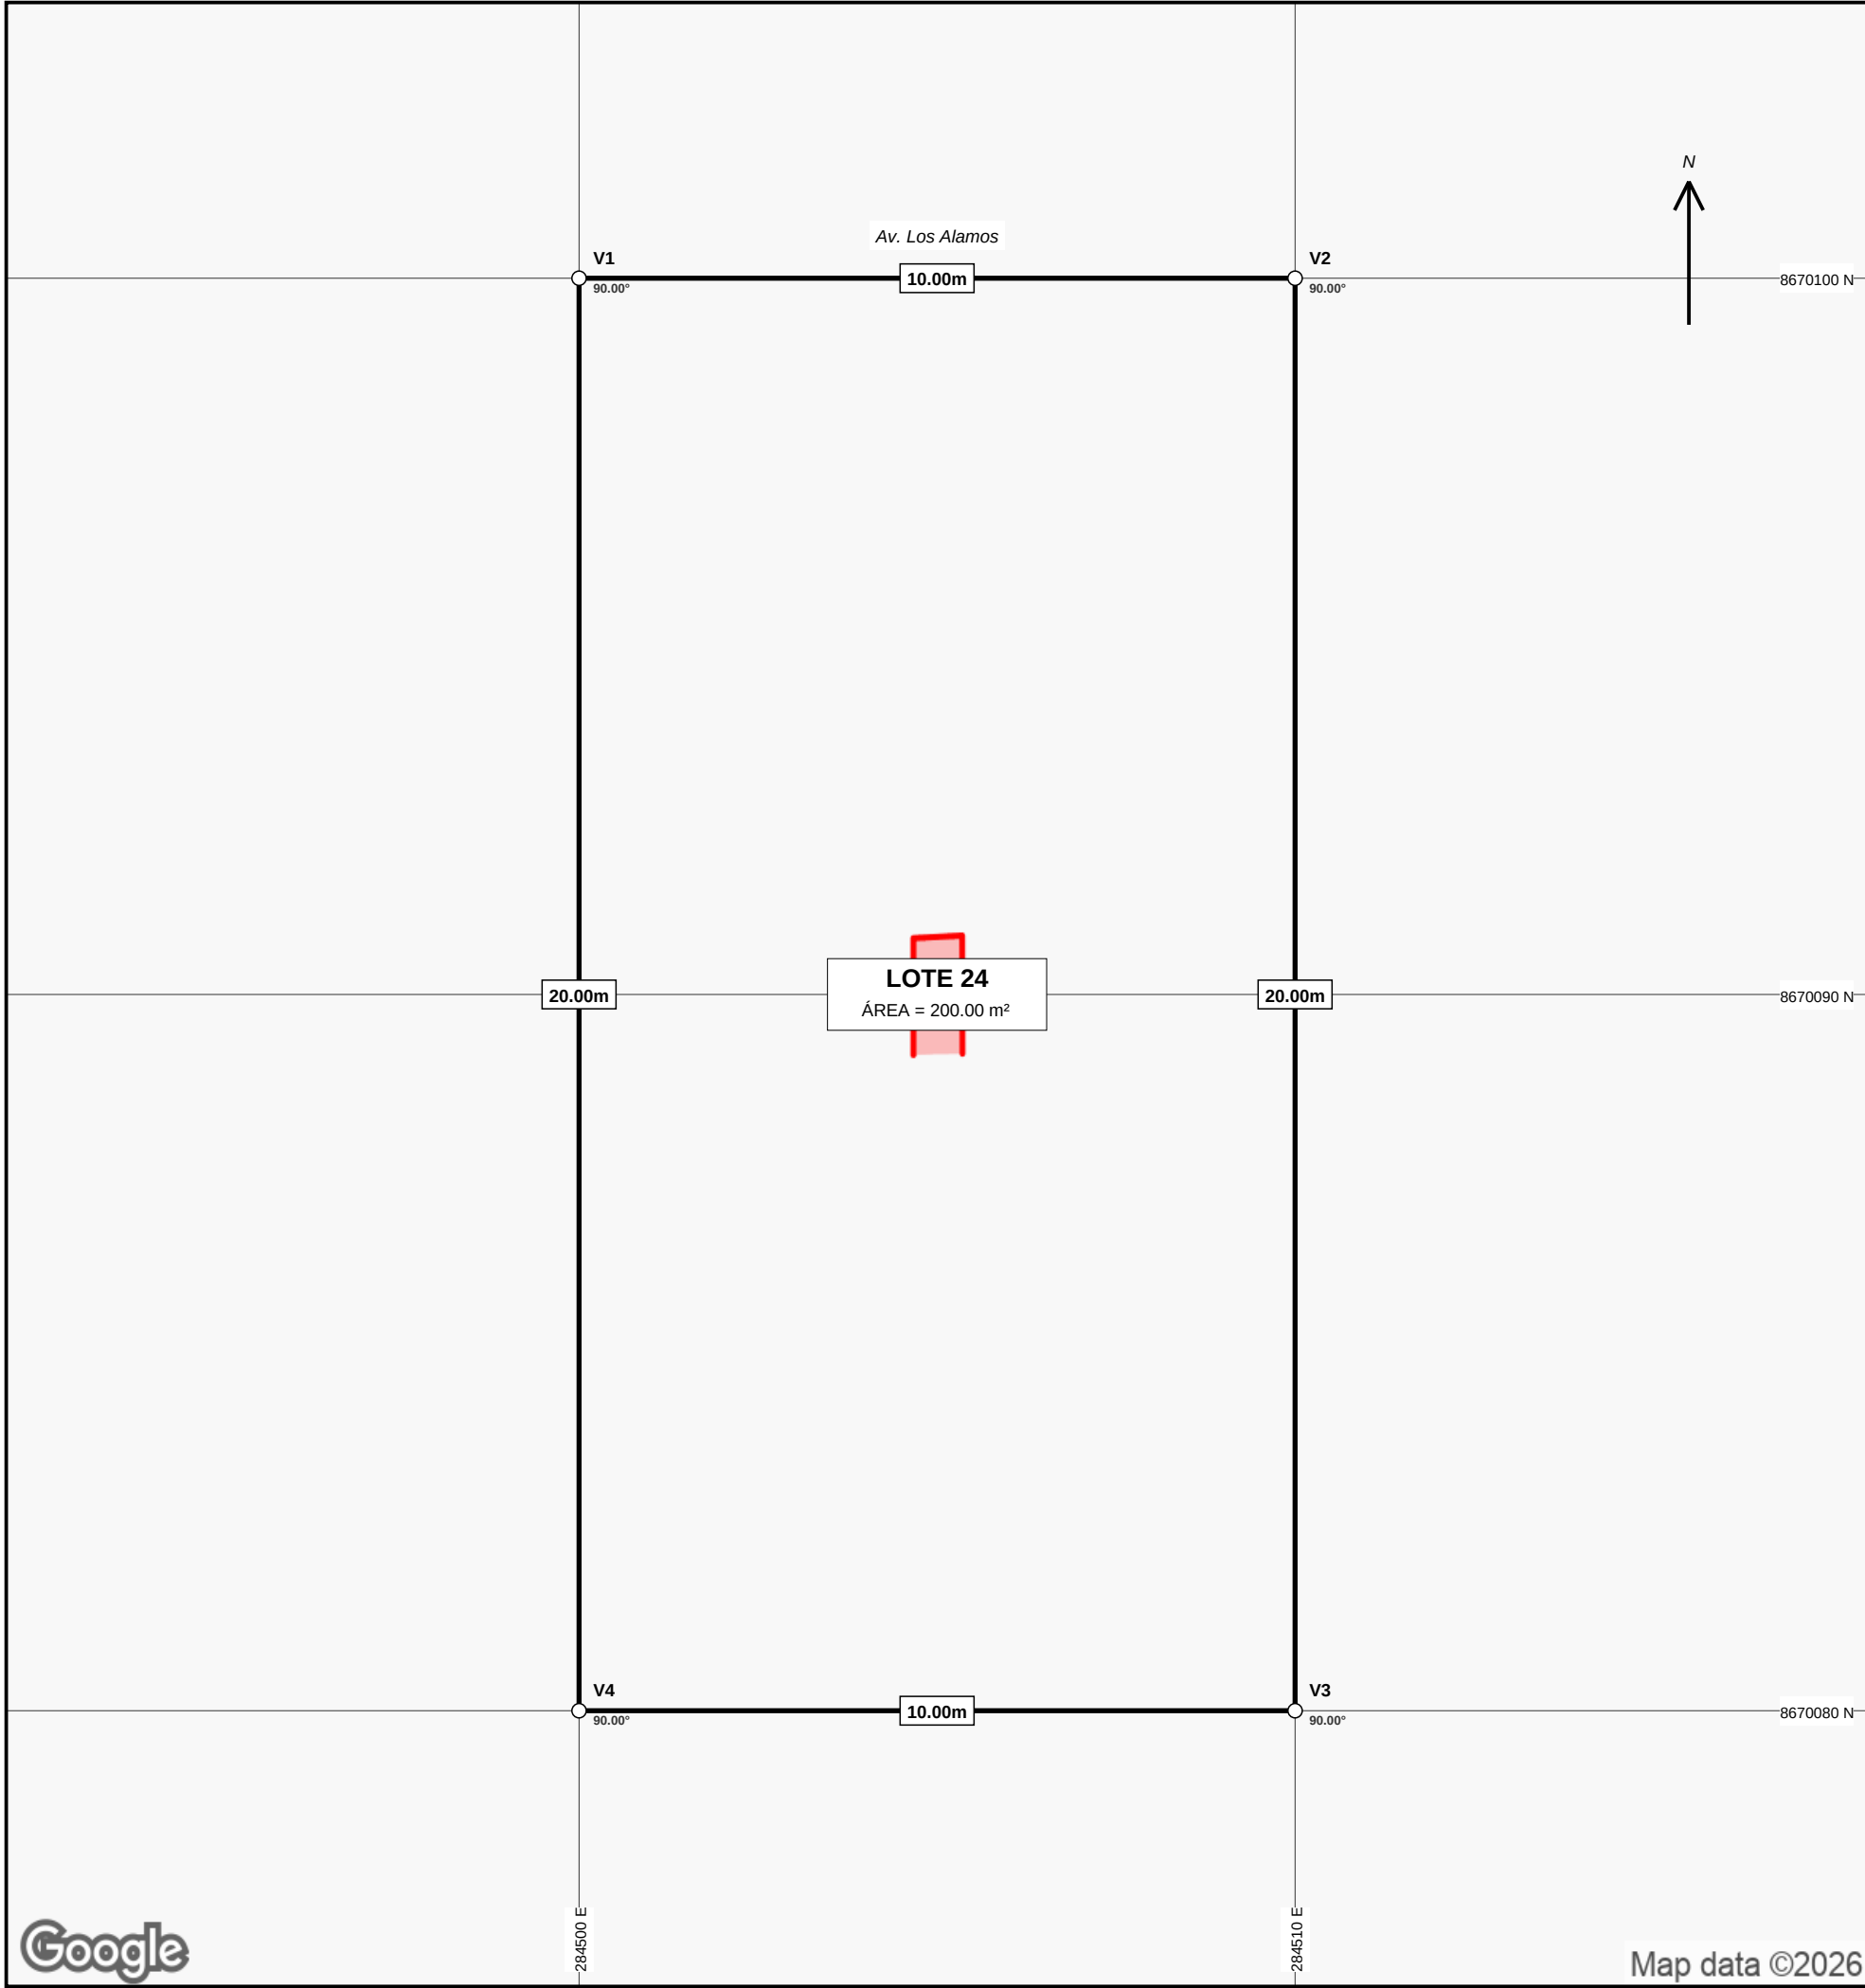

UBICACIÓN

Esquema Referencial

CUADRO DE DATOS TÉCNICOS (WGS84)

VÉRTICE	LADO	DIST.	ÁNGULO	ESTE (X)	NORTE (Y)
V1	V1-V2	10.00	90.00°	284500.00	8670100.00
V2	V2-V3	20.00	90.00°	284510.00	8670100.00
V3	V3-V4	10.00	90.00°	284510.00	8670080.00
V4	V4-V1	20.00	90.00°	284500.00	8670080.00

PLANO
PERIMÉTRICO

TERRA LIMA

PROYECTO: Etapa 1

CÓDIGO: E01MZC024P

PROPIETARIO: ---

UBICACIÓN: Mz. C Lote 24

ÁREA: 200.00 m²

PERÍMETRO: 60.00 ml

FECHA: 27/1/2026

ESCALA: 1/100

ESQUEMA DE LOCALIZACIÓN



DATOS GENERALES

Departamento:	Lima
Provincia:	Lima
Distrito:	San Juan de Lurigancho
Urbanización:	Los Cedros
Manzana:	C
Lote N°:	24
Zonificación:	RDM
Área Total:	200.00 m²

COORDENADAS CENTROIDE

SISTEMA WGS84 - ZONA 18S

ESTE (X): 284505.00 **NORTE (Y):** 8670090.00

Latitud: -76.979386° Longitud: -12.023339

MACRO LOCALIZACIÓN



PLANO UBICACIÓN

TERRA LIMA**PROPIETARIO:**

1000

DIRECCIÓN DEL PREDIO:

Av. Los Alamos S/N

PROYECTO:

Etapas 1

FECHA: 27/1/2026

ESC: 1/200



Map data ©2026